
INFORME DE VALUACIÓN COMERCIAL DE UN INMUEBLE

PRIMER CONSTRUYO

TASACIÓN N° INM 25963 - 25 BBVA - AAF

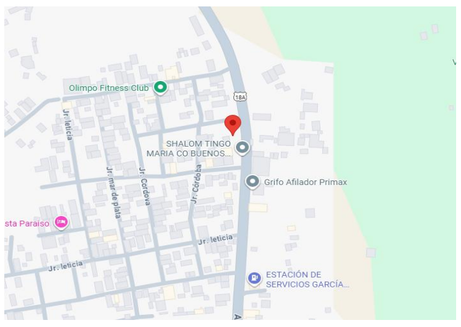

PLANO DE UBICACIÓN



FACHADA

Tipo de Tasación	Hipotecaria	Nueva	**N° de Solicitud**	738245	
Solicitante	BBVA PERÚ	OF. -	FUNC. -		
Cliente	JEENS RONERL MALPARTIDA PACHECO				
Propietario (s)	JEENS RONERL MALPARTIDA PACHECO				
Fecha de inspección	10/11/2025				
Ubicación según Partida Electrónica	Lotizacion Buenos Aires Mz E Lote 7 Sector Afilador				
Ubicación según el Predio Urbano	Documento no proporcionado.				
Ubicación Según la Inspección Ocular	Av. Afilador S/n Lotizacion Buenos Aires Mz E Lote 7 Sector Afilador				
Distrito	RUPA RUPA				
Provincia	LEONCIO PRADO	Departamento	HUANUCO		

Tipo de inmueble	Terreno	**Ocupante**	Desocupado	
Descripción	**TIPO DE USO (*)**	**%**	**TIPO DE USO (*)**	**%**
	Sin Uso	100%		
Zonificación	ZEU	**Material de construcción**	0%	
Año de construcción	2025	**Obra finalizada**	SÍ	NO X

*De acuerdo a expediente documental y tipo de construcción predominante

Area de terreno	350.00 m2	**Area construida**	380.00 m2
Declaratoria de fábrica	SÍ NO X	**Tipo de declaratoria**	TOTAL PARCIAL
Cargas	SÍ NO X	**Gravámenes**	SÍ NO X

VALORES TOTALES	MONEDA	VALOR TOTAL (Redondeado)	TERRENO	EDIF. EXISTENTE	EDIFIC. PROY.
VALOR COMERCIAL PROYECTADO	US$	245,000.00	81,250.00		163,648.49
	S/	826,140.00	273,975.00		551,822.70
VALOR DE REALIZACIÓN PROYECTADO	US$	196,000.00	65,000.00		130,918.79
	S/	660,912.00	219,180.00		441,458.16

VALORES INSCRITOS EN RR.PP.	MONEDA	VALOR TOTAL (Redondeado)	TERRENO	EDIF. EXISTENTE
VALOR COMERCIAL	US$	81,000.00	81,250.00	
	S/	273,132.00	273,975.00	
VALOR DE REALIZACIÓN	US$	65,000.00	65,000.00	
	S/	219,180.00	219,180.00	

VALORES NO INSCRITOS EN RR.PP.	MONEDA	VALOR TOTAL (Redondeado)	EDIFIC. EXISTENTE	EDIFIC. PROY.
VALOR COMERCIAL	US$	164,000.00		163,648.49
	S/	553,008.00		551,822.70
VALOR DE REALIZACIÓN	US$	131,000.00		130,918.79
	S/	441,732.00		441,458.16

VALORES DE RECONSTRUCCIÓN	MONEDA	VALOR TOTAL (VSN	EDIFIC. EXISTENTE	EDIFICACIÓN PROYECTADA	FECHA ESTIMADA DE FINALIZACIÓN
V. RECONSTRUCCIÓN (INCL. CONSTRUCCIONES DECLAR. Y NO DECLAR.)	US$	164,000.00		163,648.49	10 meses
	S/	553,008.00		551,822.70	

% Avance de Obra	0.00%	(De acuerdo a estimación pericial en base a la inspección ocular)
Tipo de cambio aplicado	3.372	Soles / Dólar

Observaciones

- El terreno cuenta con un fondo considerable con respecto a su único frente, por ello se aplica el Art. 19 del Capítulo III del Título 2 del Reglamento Nacional de Tasaciones vigente.
- El presente inmueble cuenta con una edificación inconclusa. Al tratarse del primer construyo, se estima un avance del 0%, debido a que no se cuenta con información suficiente para determinar si los muros existentes formarán parte de la edificación definitiva.
- De acuerdo con la solicitud del banco y el presupuesto presentado por el cliente, se identifica una discrepancia en los valores, ya que el monto consignado en el rubro de sanitario corresponde en realidad a instalaciones eléctricas. Asimismo, se observa que el presupuesto únicamente considera los rubros de estructura, arquitectura y sanitarias, omitiendo otros componentes de acuerdo al cuadro de valores de la solicitud.
- Se sustenta la ubicación gracias al suministro eléctrico, cuya información guarda relación con el recibo de luz.

Advertencias

Ninguna

	SI	NO	
Inmueble en zona de riesgo		X	El inmueble no se encuentra en zona de riesgo

Datos adicionales

Predio Agrícola	No	Zona de Alta Peligrosidad	No
Predio Rústico	No	Zona de Riesgo (Desastre Natural)	No

Fecha 14 de Noviembre de 2025

ING. RICARDO A. BRASCHI BEUNZA
PERITO VALUADOR – CIP.188871
BRASCHI TASACIONES S.A.C
REPEV S.B.S N°7001-2012

PERITO	*Ing. Ricardo Braschi Beunza*	*PERITO*	*Arq. José Alfredo Silva Muñoz*
REPEV	*6413-16*	*REPEV*	*5334-19*

ARQ. JOSÉ ALFREDO SILVA MUÑOZ
PERITO VALUADOR-CAP. 18133
BRASCHI TASACIONES S.A.C
REPEV S.B.S N° 7001-2012

Informe de Valuación N° **25963 - 25**

Fecha de Expedición 14/11/2025
Fecha de Caducidad 14/11/2026

MEMORIA DESCRIPTIVA

Objeto y Propósito Estimar el Valor Comercial del inmueble para fines de Garantía Hipotecaria

Alcance y Limitaciones Durante la visita SI se dieron las facilidades para la inspección ocular y toma de registro fotográfico al interior del inmueble.

Reglamentación Reglamento Nacional de Tasaciones del Perú - R.M. Nº 172 - 2016 - VIVIENDA y sus modificatorias, R.M. N° 424-2017-VIVIENDA y R.M. N°124-2020-VIVIENDA. Además se emplea la Resolución S.B.S N° 11356 - 2008 para la determinación del Valor de Realización en el Mercado.

Metodología Empleada Se utilizan los Métodos Directos (Comparación y/o Costos) así como los Indirectos cuando correspondan, establecidos en el Artículo 3, Inciso 3.1.5 del Título I del Reglamento Nacional de Tasaciones del Perú.

Documentación Proporcionada

X	Partida Registral		Predio Urb. / Rural	X	Planos		CRI
	Parámetros Urb.		Tasación anterior		Cuadro de acabados		Memoria Des.

X Otros (Especificar)

Titulación e Inscripción Terreno | Partida Electrónica | Nº 11033233 | Fecha 17/03/2022

2. DATOS GENERALES

Cliente JEENS RONERL MALPARTIDA PACHECO

Propietario(s) JEENS RONERL MALPARTIDA PACHECO

Fecha de Inspección 10/11/2025

Tipo de inmueble Terreno

Ocupante Desocupado

Georeferencias Latitud -9.320930 Longitud -75.993555 (*) Datos obtenidos Google Maps

Ubicación según Partida Electrónica	Lotizacion Buenos Aires Mz E Lote 7 Sector Afilador		
Distrito	RUPA RUPA		
Provincia	LEONCIO PRADO	Departamento	HUANUCO
Ubicación según el Predio Urbano	Documento no proporcionado.		
Distrito			
Provincia		Departamento	
Ubicación Según la Inspección Ocular	Av. Afilador S/n Lotizacion Buenos Aires Mz E Lote 7 Sector Afilador		
Distrito	RUPA RUPA		
Provincia	LEONCIO PRADO	Departamento	HUANUCO

3. CONDICIONES URBANISTICAS DEL ENTORNO

Caraterísticas del Sector y del Entorno

Tipo de Zona	Urbana	Demanda / Interés	Media
Uso Predominante	Vivienda	Zonificación	ZEU
Desarrollo	Estacionario	Altura de Edificación	Media
Nivel Socioeconómico	Estrato Medio	Velocidad de Cambio	Lenta
Tendencia del Desarrollo Urbano	Consolidado Homogeneo	Estado de Conservación	Bueno

Equipamiento del Entorno	Nivel de Equipamiento		Nivel de Equipamiento
Comercial	Abundante	Estacionamiento	Suficiente
Escolar	Suficiente	Áreas Verdes	Suficiente
Asistencial	Suficiente	Zonas Recreativas	Suficiente

Infraestructura de Servicio Urbano	Dispone	Calidad	Estado de Conservación
Vias Asfaltadas	Incompletas	Bajo	Bueno
Veredas	No tiene		
Alcantarillado	Completas	Bajo	Bueno
Agua Potable	Incompletas	Bajo	Bueno
Alumbrado	Completas	Bajo	Bueno

Vías Principales del Entorno Av. Universitaria / Jr. Los Colonos

4. CARACTERISTICAS DEL INMUEBLE

Terreno

Forma del Terreno				Topografía del Terreno				Ubicación del Terreno			
Regular		Irregular	X	Plana	X	Pendiente		Interior		Exterior	X

Construcciones

Material Predominante	Edad Efectiva (años)	Estado de Conservación

Descripción General

N° de pisos en el edificio	N° de sótanos y/o semisótanos	N° Unidades en el conjunto
		1

Piso(s) que ubican el Inmueble	Ascensor	Áreas Comunes
		No

Vista del Inmueble	Mantenimiento	Conexión de Servicios
Calle / Avenida	No cuenta con mantenimiento	Solo servicio eléctrico

Descripción y Distribución Detallada del Inmueble

Se trata de un Terreno que cuenta con frente a calle, de forma irregular, con topografía plana, con zonificación Zona Expansión Urbana (ZEU).
El predio se encuentra dentro de un entorno de estrato socioeconómico medio/bajo, que cuenta con pistas y veredas incompletas en buen estado, cuenta con instalaciones de energía eléctrica, agua y desagüe en regular estado, cerca de colegios, parques, supermercados, otros. La altura máxima en la cuadra es de 5 pisos. Los usos en el entorno inmediato son residenciales con predominancia del uso residencial.

Informe de Valuación N° **25963 - 25**

Fecha de Expedición 14/11/2025
Fecha de Caducidad 14/11/2026

MEMORIA DESCRIPTIVA

Orientación	Linderos	Medida (Metros)
Frente	Con la Carretera Tingo Maria - Huanuco	10.00
Derecha	Con el Lote 6	34.00
Izquierda	Con el Lote 24 y 25	36.00
Fondo	Con el Lote 30	10.00
		90.00

TERRENO

Unidad Inmobiliaria	Unidad Métrica	A.M. Prop. Horiz/ Vert.	% Participación	Área Privativa	Obtención del Área	Observación
Terreno	m2	350.00	85.71%	300.00	F. Reg/Part. Elect	
Exceso de area de Terreno	m2		14.29%	50.00	F. Reg/Part. Elect	
Total área de terreno				**350.00**		

Nota

CONSTRUCCION

Descripción	Unidad Métrica	Área Techada	Área sin Techar	Área Ocupada	Obtención del Área	Edificación Declarada
Piso 1	m2	380.00		380.00	Solicitud del Banco	No
Total áreas construidas		**380.00**	**0.00**	**380.00**		

Nota

CARACTERISTICAS PRINCIPALES DE LA CONSTRUCCION

Tipo de construcción : Definitiva ☐ Provisional ☐

Origen de la construcción* : Const. Profesional ☐ Autoconstrucción ☐
* Opinión del Suscrito

Estructura general

Cimentación	
Estructura	
Muros	
Techos	
Cobertura	
Inst. Eléctricas	
Inst. Gas	
Inst. Sanitarias	

ACABADOS

Puertas	Tipo			
	Material			
	Sistema			
Ventanas	Marco			
	Vidrio			
	Sistema			
Mamparas	Marco			
	Vidrio			
	Sistema			
Muebles de cocina	Tipo			
	Material			
	Tableros			
	Lavaderos			
Closets				
Pisos				
Revestimientos				
Cerrajería				

Obras Complementarias e Instalaciones Fijas						
	Aire Acondicionado	☐	Parrilla	☐	Cerco	☐
	Alarma	☐	Sistema Hidroneumático	☐	Cisterna	☐
	Ascensor	☐	Sistema Contra Incendio	☐	Iluminación Especial	☐
	Intercomunicador	☐	Tanque Elevado	☐	Piscina	☐

Otros y Comentarios

Informe de Valuación N° **25963 - 25**

Fecha de Expedición 14/11/2025
Fecha de Caducidad 14/11/2026

ANALISIS METODOLOGICO

METODO DE COSTOS O REPOSICION (OFERTA DE MERCADO PARA TERRENOS)


A. DATOS GENERALES DE REFERENCIAS DE MERCADO

	Descripción	Ubicación	Fuente (In situ, correo, página web, periódicos, etc)	Parámetros (pisos)	Contacto / Teléfono	Forma / Topografía	Zonificación	Distancia al Inmueble (m)	Fecha
1	Venta de Terreno en Sector Afilador en la Calle S/n, Tingo Maria. US$ 570,000.00 AT: 1,146.00 m2 AC: 420.00 m2 Coordenadas: -9.324850677677679, -75.9943452656166	Exterior	https://www.facebook.com/commerce/listing/1558072535380714/?ref=share_attachment	-	Corredor Inmobiliario 962582760	Irregular / Plano	ZEU	300.00	11-Nov-25
2	Venta de Terreno en Sector Afilador en la Calle S/n, Tingo Maria. US$ 103,795.97 AT: 340.00 m2 Coordenadas: -9.32633788100647, -75.99372957839066	Exterior	https://www.facebook.com/commerce/listing/1366018705230024/?ref=share_attachment	-	Corredor Inmobiliario 962582760	Irregular / Plano	ZEU	350.00	11-Nov-25
3	Venta de Terreno en Sector Afilador en la Jr.Los Descalzos con Jr Los Americanos, Tingo Maria. US$ 380,000.00 AT: 1,423.33.00 m2 Coordenadas: -9.325572295372758, -75.9948933413355	Esquina	https://www.facebook.com/commerce/listing/2057175988386290/?media_id=0&ref=share_attachment	-	Corredor Inmobiliario 962582760	Irregular / Plano	ZEU	390.00	11-Nov-25

B. HOMOLOGACIÓN DE REFERENCIAS DE MERCADO DE TERRENOS

	Valor del Inmueble Referencial (US$)	Área (m2)	Valor Unitario Terreno (US$/m2)	Factores de HOMOLOGACIÓN						Factor Resultante	Valor Unit. Terreno Homologado (US$/m2)
				Ub.	Ent.	Sup	Ser.	Zon.	F.N.		
1	323,040.00	1,146.00	281.88	1.00	1.00	1.02	1.00	1.00	0.90	0.92	259.33
2	103,795.97	340.00	305.28	1.00	1.00	1.00	1.00	1.00	0.90	0.89	271.70
3	380,000.00	1,423.33	266.98	0.95	1.00	1.03	1.00	1.00	0.90	0.87	232.27
	Valor Unitario Terreno Homologado Promedio [$/m²]		254.43	VUT Prom. Homologado ajustado[$/m²]							250.00

PLANO DE UBICACIÓN Y REFERENCIAS DE TERRENO

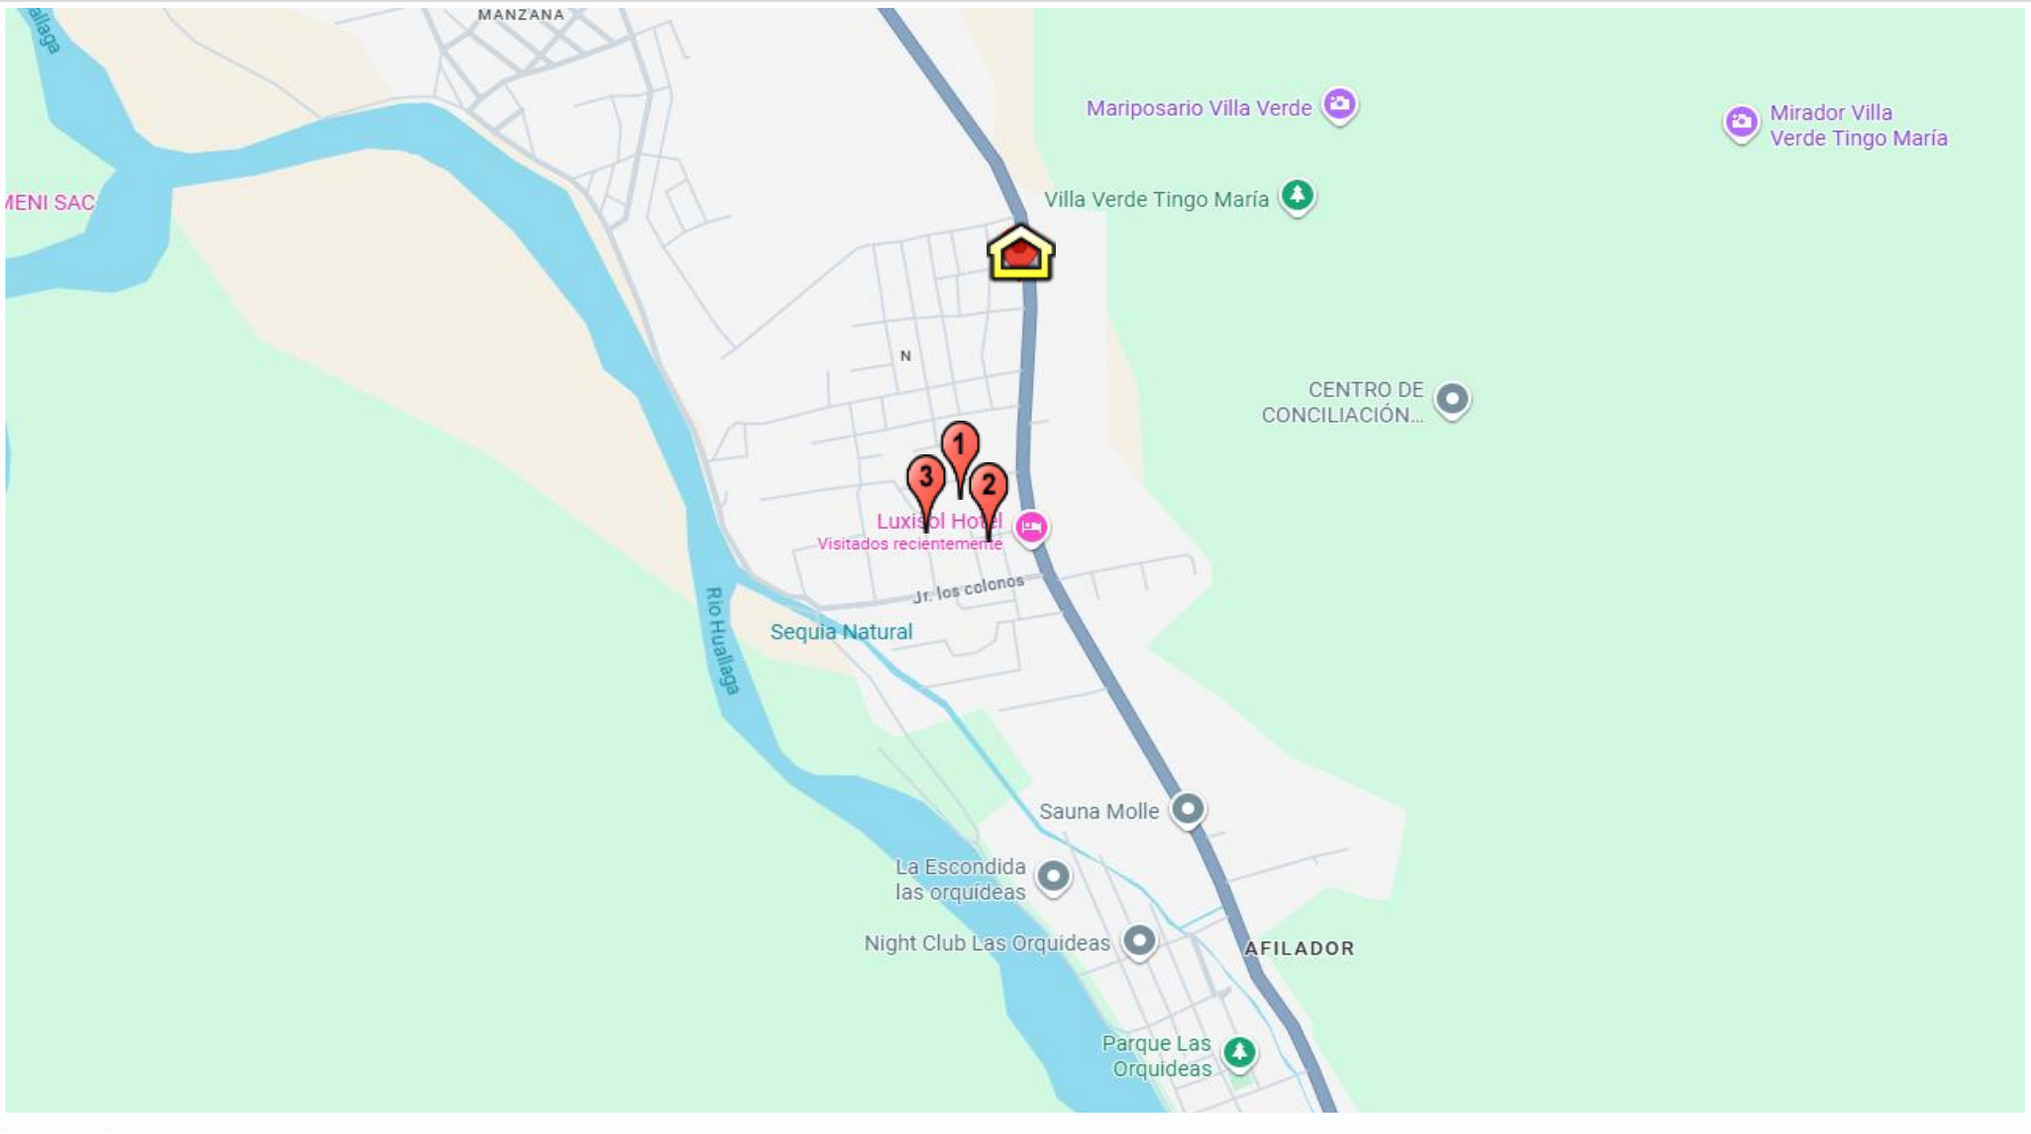

Informe de Valuación N° **25963 - 25**

Fecha de Expedición 14/11/2025
Fecha de Caducidad 14/11/2026

ANALISIS METODOLOGICO

METODO DIRECTO DE COSTOS O REPOSICION

A. VALOR DE TERRENO (VT)

De acuerdo a la Investigación de Mercado de Terrenos con características similares al inmueble tasado se obtiene;

Unidad Inmobiliaria	Área de terreno (m2)	% de Participación	V.U. de Terreno (US$/m2)	Factor de Ajuste		Valor de Terreno (US$)
Terreno	300.00	85.71%	250.00	1.00	1.00	75,000.00
Exceso de area de Terreno	50.00	14.29%	250.00	1.00	0.50	6,250.00
Subtotal Terreno (VT)	350.00		232.14			81,250.00

Nota: • Para calcular el Valor del Terreno se ha aplicado R.N. Capítulo III, Artículo 19, que indica que si el área de terreno es mayor al triple cuadrado del frente del terreno, se multiplica el triple del cuadrado del frente del terreno por el Valor de Terreno Urbano, y se suma el producto del exceso del área de terreno por el 50% del Valor de Terreno Urbano.

B. VALOR DE LAS EDIFICACIONES (VSNE Y VE)

De acuerdo a las características constructivas y a los acabados del inmueble observados en la inspección realizada se estima;

Región de la Edificación
Selva

	1	Muros y Columnas	2	Techos	3	Pisos	4	Puertas y Ventanas	5	Revest.	6	Baños	7	I.I.E.E. / I.I.S.S	Util. y GG S/	VUE S/	VUE US$
	Clas.	Costo/m2	Clas.	Costo/m2	Clas.	Costo/m2	Clas.	Costo/m2	Clas.	Costo/m2	Clas.	Costo/m2	Clas.	Costo/m2			
VUE1															0.00	0.00	**0.00**

Gastos Generales (GG) 14% (Obra Pequeña)
Utilidad (Util.) 10% Tipo de Cambio **S/. 3.372**

Cálculo del Valor Similar a Nuevo o Valor de Reconstrucción de las Edificaciones (VSNE) y el Valor de las Edificaciones (VE)

Descripción	Área (m2)	VUE (US$/m2)	Valor Similar a Nuevo (US$)	Material Predominante	Edad (años)	Estado de Conservación	FD (*)	FA	Valor de Edificación (US$)
Piso 1	380.00	430.65	163,648.49	Concreto	0	En proyecto	1.00	1.00	163,648.49
Subtotal Edificaciones (VSNE)	380.00	US$	163,648.49	Subtotal Edificaciones (VE)			US$		163,648.49

Nota sobre el Factor (FA):

C. VALOR DE ÁREAS COMUNES (VAC)

Según el Reglamento General de Tasaciones del Perú, para el valor de las Áreas Comunes, se asigna un % del valor de la edificación;

Descripción	% de Áreas Comunes	Valor Unitario de Áreas Comunes (US$/m2)	Valor de Reconstrucción Áreas Comunes (US$)	FD (*)	Valor de Áreas Comunes (US$)
Subtotal Áreas Comunes (VAC)		US$	0.00	US$	0.00

D. VALOR DE LAS INSTALACIONES Y OBRAS COMPLEMENTARIAS (VI + VOC)

Descripción	Cantidad	Unidad (u)	Valor Unitario (US$/u)	Valor de Reconstrucción (US$)	FD (*)	Valor de Inst. y Obras Complem. (US$)
Subtotal Instalaciones y Obras Complementarias (VI + VOC)			US$	0.00	US$	0.00

(*) Factor de Depreciación

E. VALOR TOTAL DEL PREDIO (VTP1) [Mediante el Método de Costos Directos = VT + VE + VAC + VI + VOC] US$ 244,898.49

F. VALOR DE RECONSTRUCCIÓN DEL INMUEBLE TASADO (VSN) [= VSNE + VSNAC + VSNVI + VSNVOC] US$ 163,648.49

Informe de Valuación N° **25963 - 25**

Fecha de Expedición 14/11/2025
Fecha de Caducidad 14/11/2026

RESULTADOS

1. RESUMEN GENERAL DE TASACION

A. RESULTADOS DE LOS MÉTODOS DIRECTOS

	VTP (US$)	VU (US$/m2)	VTP (S/)
Método de Costos o Reposición (Redondeado)	244,898.49	644.47	825,797.71
Método de Comparación o de Mercado (Redondeado)	No considerado		

B. RESULTADO DEL MÉTODO INDIRECTO

Método de la Renta o Capitalización	No considerado		

2. VALOR COMERCIAL DEL INMUEBLE

A. VALOR COMERCIAL (VC)

Para determinar la conclusión del Valor Comercial del inmueble motivo de la presente tasación, se han tenido en cuenta las siguientes consideraciones

a.

b.

c.

d. El método que mejor refleja el Valor Comercial es por **Método Directo de Costos (O de Reposición)**

Valor Comercial en Dólares (Moneda Extranjera)

DOSCIENTOS CUARENTA Y CINCO MIL CON 00/100 DÓLARES AMERICANOS

Valor Comercial

US$ 245,000.00

Valor Comercial en Soles (Moneda Local)

OCHOCIENTOS VEINTISEIS MIL CIENTO CUARENTA CON 00/100 SOLES

S/ 826,140.00

VALOR DE REALIZACION

A. VALOR DE REALIZACIÓN INMEDIATA (VRI)

El Valor de Realización Inmediata, es el Valor Neto del inmueble que se esperaría recuperar como consecuencia de la eventual venta del bien en el menor tiempo posible y en las condiciones actuales del inmueble y el mercado. Se obtiene descontando los castigos y cargos por los conceptos indicados a continuación;

Concepto de la Deducción	% de la Deducción	Importe (US$)
Gastos de Publicidad, Tasación para realización, Comisiones de ventas, Mantenimiento, considerando su venta a mediano plazo.	20.00%	49,000.00
Otras Deducciones (Sólo casos especiales)	0.00%	0.00
Total Deducciones	**20.00%**	**US$ 49,000.00**

En Dólares (Moneda Extranjera)

CIENTO NOVENTA Y SEIS MIL CON 00/100 DÓLARES AMERICANOS

Valor Realización Inmediata

US$ 196,000.00

En Soles (Moneda Local)

SEISCIENTOS SESENTA MIL NOVECIENTOS DOCE CON 00/100 SOLES

S/ 660,912.00

OBSERVACIONES DEL PERITO

La documentación recibida no corresponde necesariamente a un estudio completo de títulos, más es la documentación brindada para elaborar el informe, el perito trabaja sobre estos documentos y no se hace responsable de omisiones.

CONDICIONANTES Y ADVERTENCIAS

1. Las áreas de terreno, áreas construidas, áreas libres y áreas ocupadas fueron obtenidas de la documentación registral, documentación predial, planos, etc.; proporcionadas, no habiendo realizado el perito levantamiento de áreas ni medidas perimétricas.
2. La información utilizada ha sido proporcionada exclusivamente por la entidad propietaria, no habiéndose revisado documentos distintos. No se asume ninguna responsabilidad sobre el contenido de la información ni sobre conclusiones erradas que eventualmente podrían haberse derivado de su contenido.
3. La interpretación de los documentos y sus condiciones, específicamente aplicada a la pericia, se asume como razonablemente válida para efectos del presente informe, más no sustituye una asesoría legal especializada en la materia.
4. Se considera que la información y documentación técnica proporcionada proviene de fuentes realistas y confiables, por lo que no se asume responsabilidad por eventuales errores inducidos por el contenido de éstas.
5. Las conclusiones del informe son válidas a la fecha de emisión del mismo y durante el periodo de vigencia establecido, siempre que no varíen significativamente las condiciones del mercado y de los bienes, en cuyo caso deberá requerirse una actualización de la valuación.
6. La existencia de documentos adicionales no proporcionados, que puedan contener información diferente de la acreditada, puede invalidar las conclusiones del presente informe sin responsabilidad alguna de parte de los peritos.
7. El presente informe se emite considerando que no existen condiciones o intereses ocultos y que se cumple con todos los requisitos legales relativos a la propiedad, tenencia y transferencia de los derechos.
8. La cantidad y calidad de la documentación e información existente se ha considerado suficiente para acreditar las características generales del bien.
9. El objeto del presente informe de tasación es el de determinar el valor comercial del bien inmueble y no de determinar una asesoría legal, técnica estructural, ni de otro carácter.

RESPONSABLE

EMPRESA TASADORA	**BRASCHI TASACIONES SAC**
REGISTRO REPEV	**7001-2012**
RESPONSABLE DE INSPECCION OCULAR	**AYRTON CESAR ALBAN FLORES / ARQ. JOSE SILVA MUÑOZ**

ING. RICARDO A. BRASCHI BEUNZA
PERITO VALUADOR – CIP.188871
BRASCHI TASACIONES S.A.C
REPEV S.B.S N°7001-2012

ARQ. JOSÉ ALFREDO SILVA MUÑOZ
PERITO VALUADOR-CAP. 18133
BRASCHI TASACIONES S.A.C
REPEV S.B.S N° 7001-2012

PERITO	Ing. Ricardo Braschi Beunza
REPEV	6413-16

PERITO	Arq. José Alfredo Silva Muñoz
REPEV	5334-19

DOCUMENTACION GRAFICA

FACHADA



COLINDANTE DERECHO



SUMINISTRO DEL COLINDANTE DERECHO



COLINDANTE IZQUIERDO



SUMINISTRO DEL COLINDANTE IZQUIERDO



ENTORNO



DOCUMENTACION GRAFICA

ENTORNO



ENTORNO



INTERIOR DEL TERRENO



INTERIOR DEL TERRENO



INTERIOR DEL TERRENO



INTERIOR DEL TERRENO



DOCUMENTACION GRAFICA

INTERIOR DEL TERRENO




INTERIOR DEL TERRENO



INTERIOR DEL TERRENO



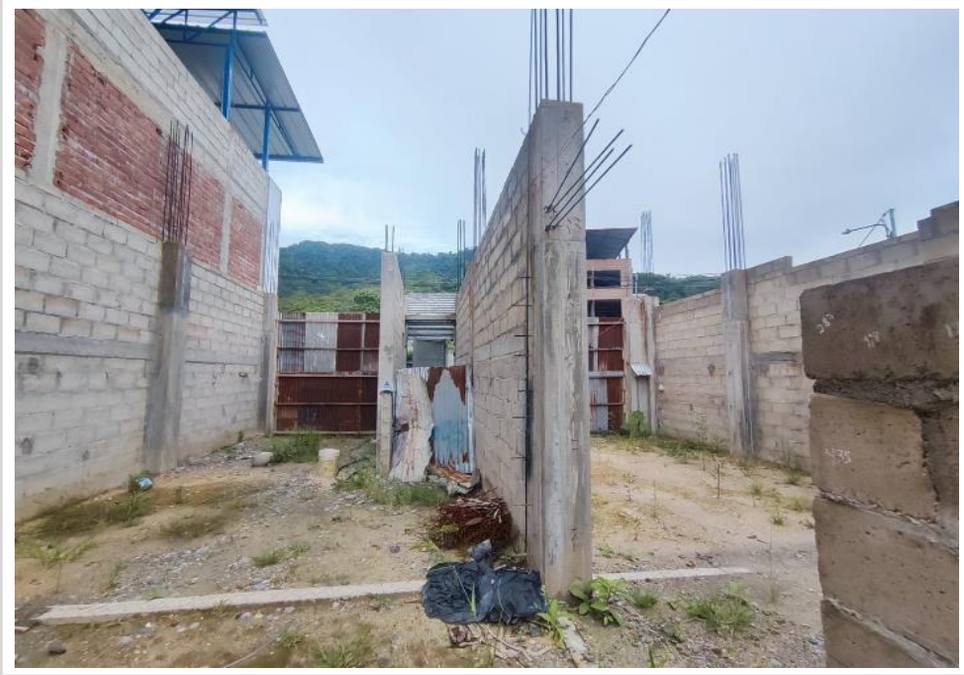

ANEXO

PARTIDA REGISTRAL

PUBLICIDAD : 1584861 Recibo Nº 2022-481-2536 CERTI. LITERAL - PREDIOS Partida Nº 11033233

Activa
Ve a Co

sunarp

ZONA REGISTRAL Nº VIII - SEDE HUANCAYO
OFICINA REGISTRAL TINGO MARIA
Nº Partida: 11033233

INSCRIPCION DE PROPIEDAD INMUEBLE
LOTIZACION BUENOS AIRES MZ E LOTE 7 SECTOR AFILADOR
RUPA RUPA

REGISTRO DE PROPIEDAD INMUEBLE
RUBRO :*PARTIDA DE INDEPENDIZACION (1ERA. DOMINIO)*
G00001

INDEPENDIZACION

A.- ANTECEDENTE REGISTRAL: *P.E Nº 02001841 DEL R.P.I.*

B.- DESCRIPCION DEL INMUEBLE:

LOTE Nº 7 DE LA MZ. "E".- *UBICADO EN LA LOTIZACION BUENOS AIRES DEL SECTOR AFILADOR, DISTRITO DE RUPA RUPA, PROVINCIA DE LEONCIO PRADO, DEPARTAMENTO DE HUANUCO.-*

LINDEROS MEDIDAS PERIMETRICAS:

POR EL FRENTE, *CON LA CARRETERA TINGO MARIA – HUANUCO CON* ***10.00 M.***
POR LA DERECHA ENTRANDO, *CON EL LOTE Nº 6 CON* ***34.00 M.***
POR LA IZQUIERDA ENTRANDO, *CON EL LOTE Nº 24 Y Nº 25 CON* ***36.00 M.***
POR EL FONDO, *CON EL LOTE Nº 30, CON* ***10.000 M.***

ÁREA: 350.00 M² ***PERÍMETRO: 90.00 M.***

C.- TITULOS DE DOMINIO

PROPIETARIO: ***LUIS GONZAGA VASQUEZ DIAZ*** *casado(a) D.N.I Nº 22966890.*
PROPIETARIA: ***SALOME FERNANDEZ DE VASQUEZ*** *casado(a) D.N.I Nº 22964463.*

LA INDEPENDIZACION SE HACE A FAVOR DE: ***LUIS GONZAGA VASQUEZ DIAZ Y SALOME FERNANDEZ DE VASQUEZ,*** *QUIENES SON TITULARES REGISTRALES DE LA PARTIDA MATRIZ Y DE CONFORMIDAD CON LO DISPUESTO EN EL ARTICULO 60 DEL R.I.R.P, Y POR RESOLUCION GERENCIAL Nº 218-2014 MPLP/GIDL DE FECHA 19/12/2014, SUSCRITA POR EL ING. KELWIN SABINO GARCIA, GERENTE DE INFRAESTRUCTURA Y DESARROLLO LOCAL DE LA MUNICIPALIDAD PROVINCIAL DE LEONCIO PRADO.-*

D.- GRAVAMENES: *NINGUNO.*
E.- CANCELACIONES: *NINGUNO.*
F.- REGISTRO PERSONAL: *NINGUNO.*

El título fue presentado el 22/12/2014 a las 02:13:00 PM horas, bajo el Nº 2014-00015382 del Tomo Diario 0033. Derechos cobrados S/.222.00 nuevos soles con Recibo(s) Número(s) 00000055-06 00001011-01.-LEONCIO PRADO, 03 de Febrero de 2015

ZONA REGISTRAL N°VIII
OFICINA REGISTRAL DE TINGO MARIA
Julio Cesar Figueroa Prudencio
REGISTRADOR PUBLICO

Isabel Alejandra Zavala
CERTIFICADOR
OFICINA REGISTRAL DE TINGO MARIA
Zona Registral Nº VIII - Sede Huancayo

Pág. Solicitadas : Todas IMPRESION : 17/03/2022 09:24:59 Página 1 de 7

Resolución del Superintendente Nacional de los Registros Públicos Nº 124-97-SUNARP

ANEXO

PARTIDA REGISTRAL

PUBLICIDAD : 1584861 Recibo N° 2022-481-2536 CERTI. LITERAL - PREDIOS Partida N° 11033233

sunarp
Superintendencia Nacional de los Registros Públicos

ZONA REGISTRAL N° VIII - SEDE HUANCAYO
OFICINA REGISTRAL TINGO MARIA
N° Partida: 11033233

INSCRIPCION DE PROPIEDAD INMUEBLE
LOTIZACION BUENOS AIRES MZ E LOTE 7 SECTOR AFILADOR
RUPA RUPA

REGISTRO DE PROPIEDAD INMUEBLE
RUERO :TITULOS DE DOMINIO
C00004

Donación

Donatario: **JEENS RONEL MALPARTIDA PACHECO** estado civil casado(a) e identificado con D.N.I N° 44893228.

Adquiere el dominio y propiedad del inmueble inscrito en la presente partida, por haberlo otorgado en calidad de donación sus anteriores propietarios: **ALEJANDRA ROJAS ESPINOZA,** valor del inmueble **S/. 6,000.00 (seis mil y 00/100 soles)**. - Asi consta de la escritura pública n.° 690 de fecha 24/05/2021, otorgado ante notario de la provincia de Leoncio Prado-Tingo Maria, Mario Anibal Arias Jaramillo.-

El titulo fue presentado el 25/05/2021 a las 08:45:01 AM horas, bajo el N° 2021-01338846 del Tomo Diario 0033. Derechos cobrados S/ 47.00 soles con Recibo(s) Número(s) 00040612-01.-LEONCIO PRADO, 27 de Mayo de 2021. Presentación electrónica.

ZONA REGISTRAL N° VIII
OFICINA REGISTRAL HUANCAYO-TINGO MARIA

Julio Cesar Figueroa Prudencio
REGISTRADOR PUBLICO


Isabel Algumer Zavala
CERTIFICADOR
REGISTRAL DE TINGO MARIA

Página Número 1

Resolución del Superintendente Nacional de los Registros Públicos N° 124-97-SUNARP

ANEXO

ZONIFICACIÓN

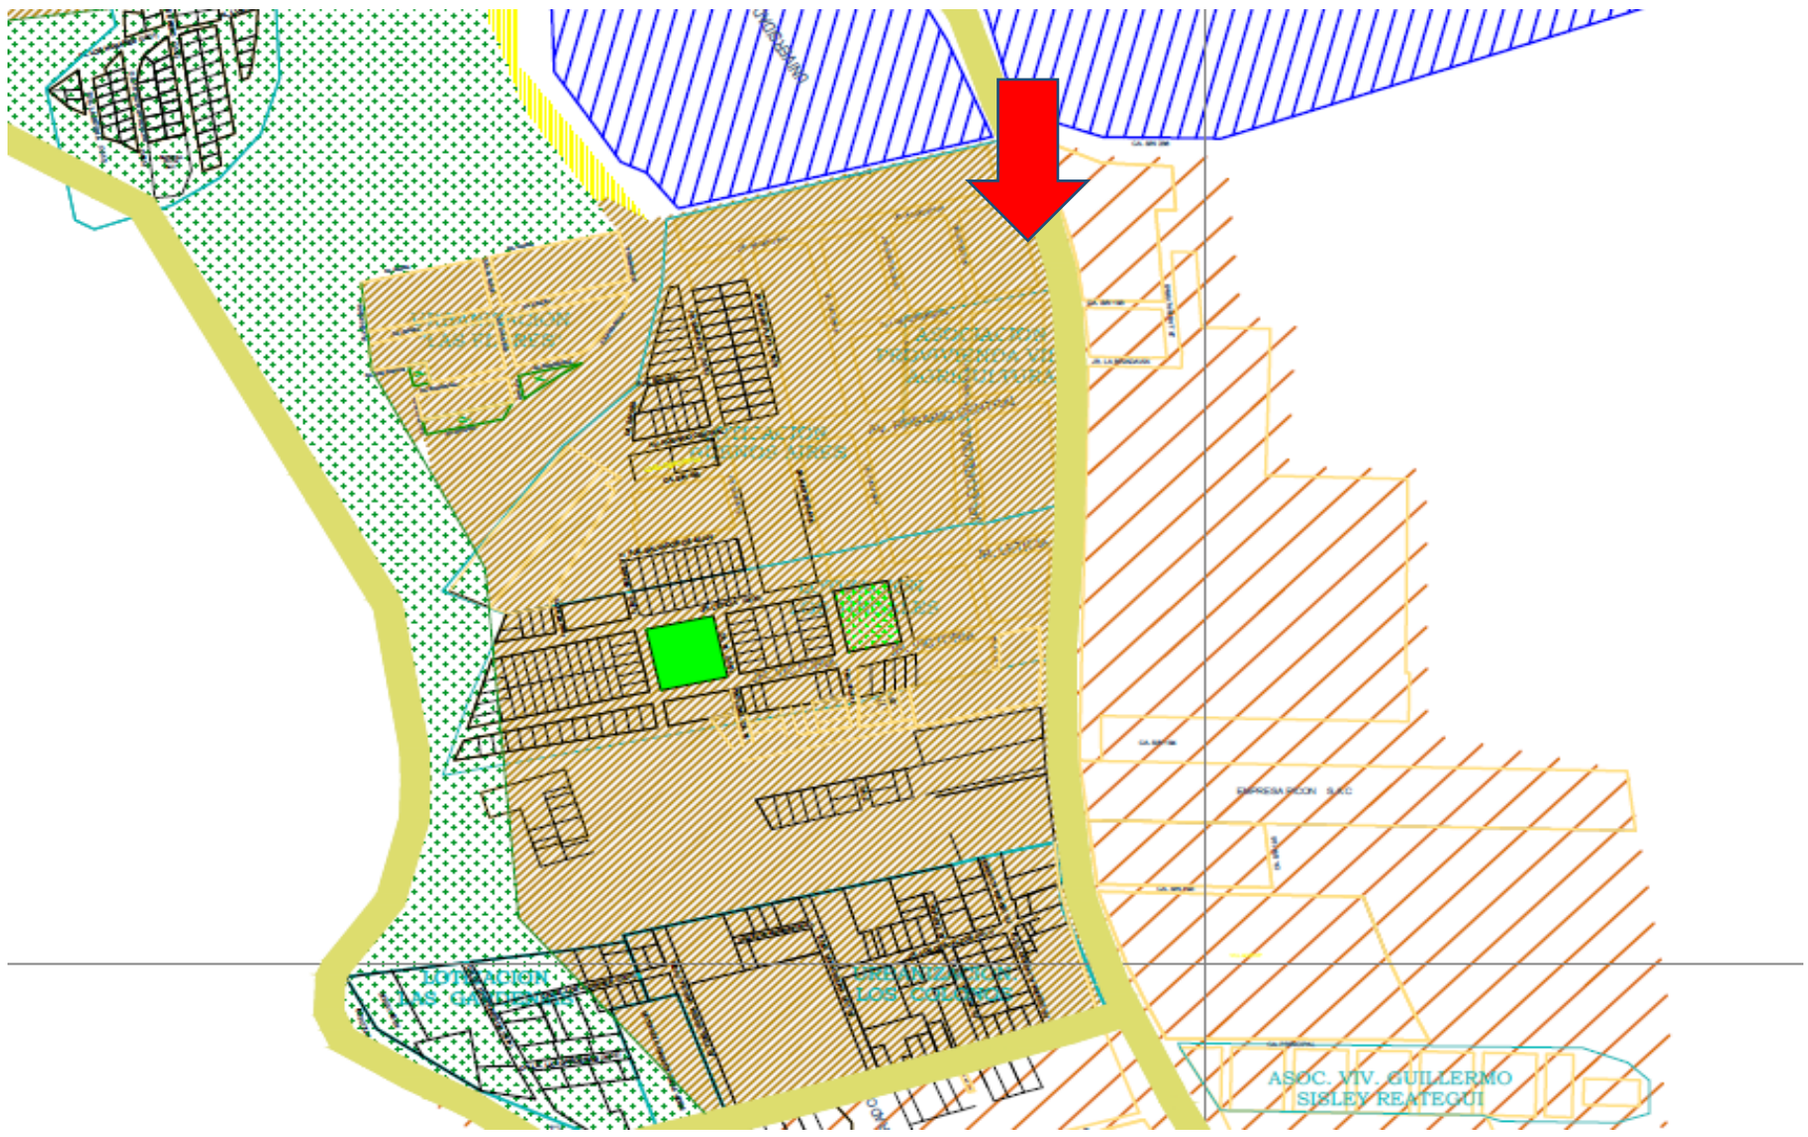


CLAVE

RDA	RESIDENCIAL DENSIDAD ALTA		TT	TERMINAL TERRESTRE
RDM	RESIDENCIAL DENSIDAD MEDIA		AA	AEROPUERTO
RDB	RESIDENCIAL DENSIDAD BAJA		MC	MERCADO CENTRAL
CC	COMERCIO CENTRAL		MZ	MERCADO ZONAL
CE	COMERCIO ESPECIALIZADO		PZ	PARQUE ZONAL
ZR	ZONA RECREACIONAL			
ZRE	ZONA DE REGLAMENTACION ESPECIAL			
ZHR	ZONA DE HABILITACION RECREACIONAL			
ZAI	ZONA AGRICOLA INTANGIBLE			
ZEE	ZONA DE EXPANSION URBANA			LIMITE DEL AREA URBANA
EE	EQUIPAMIENTO EDUCATIVO			VIADUCTO CARRETERA CENTRAL
ES	EQUIPAMIENTO DE SALUD			INTERCAMBIO VIAL
OU	OTROS USOS	OU		
Z-IL	INDUSTRIA LIVIANA			
ZPE	ZONA DE PROTECCION ECOLOGICA			

ANEXO

SUSTENTO DE UBICACIÓN

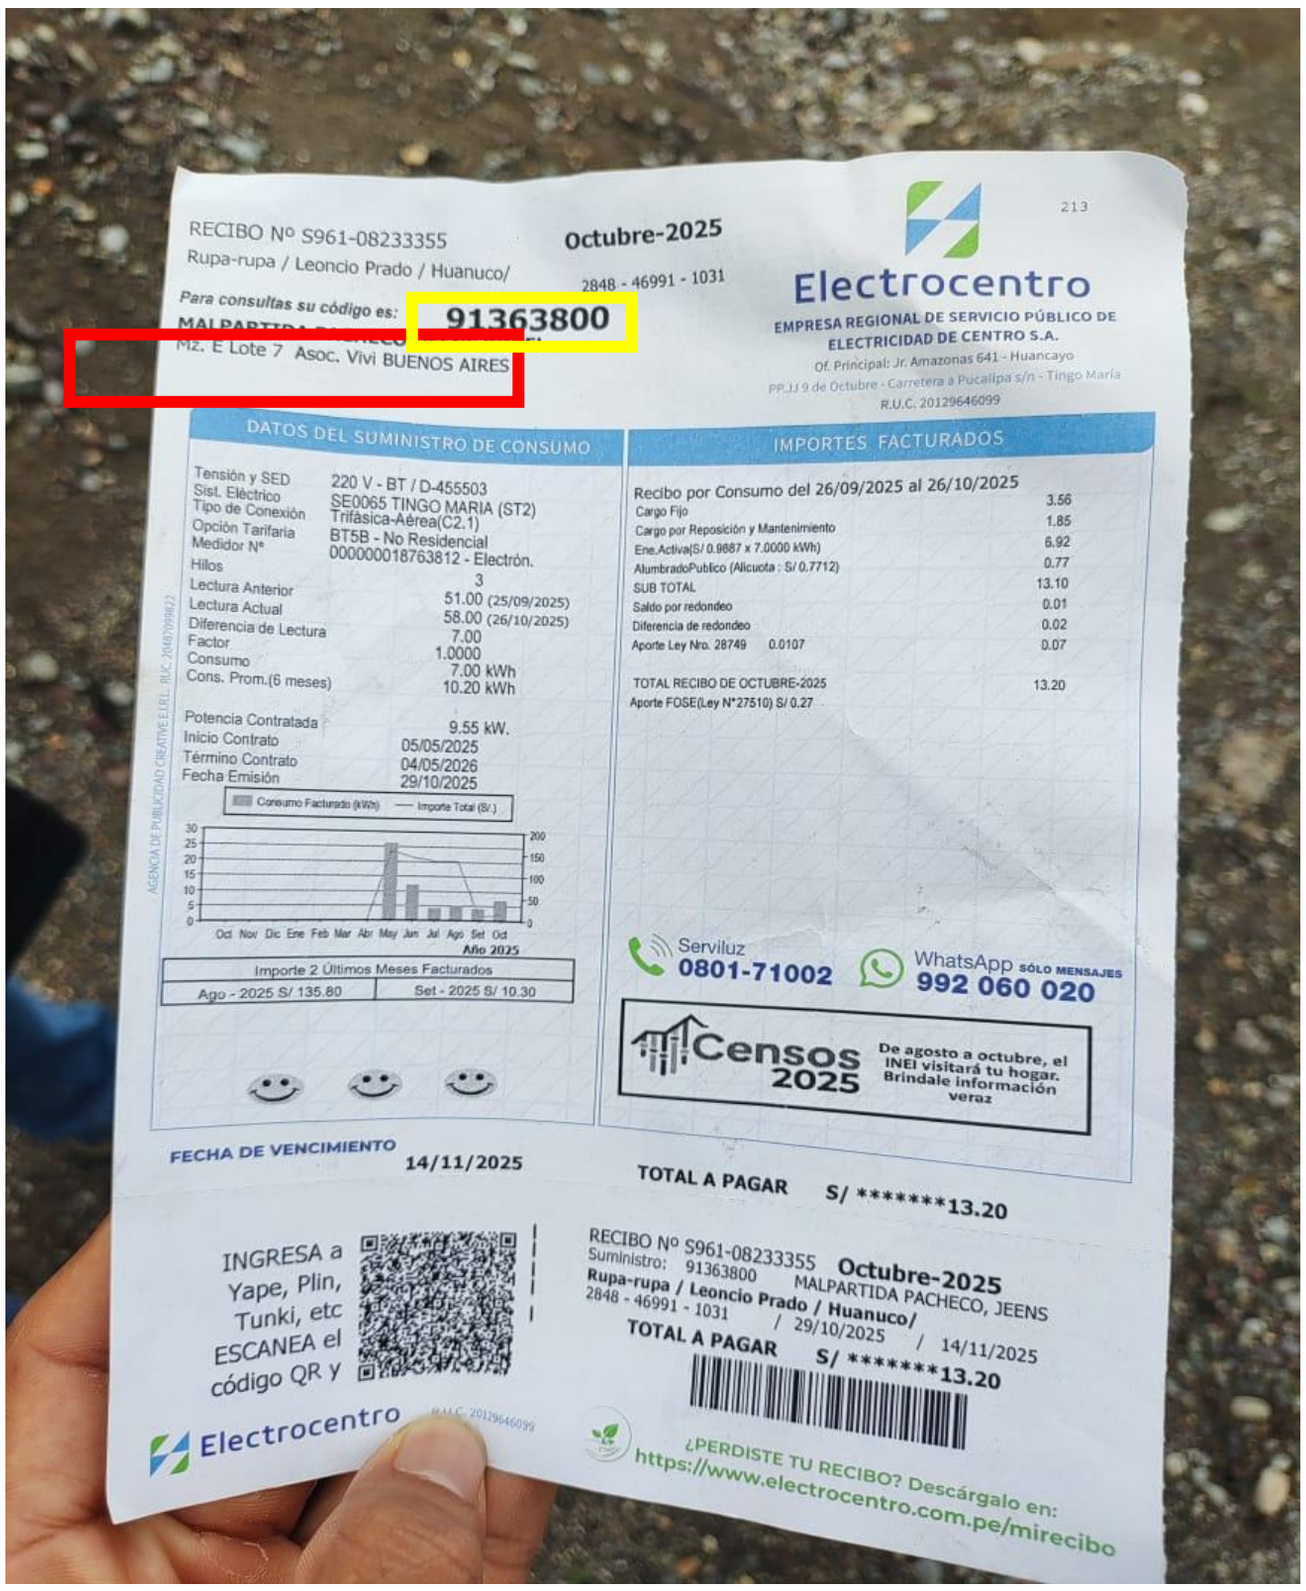






ZONA REGISTRAL Nº VIII - SEDE HUANCAYO
OFICINA REGISTRAL TINGO MARIA
Nº Partida: 11033233

sunarp
Superintendencia Nacional de los Registros Públicos

INSCRIPCION DE PROPIEDAD INMUEBLE
LOTIZACION BUENOS AIRES MZ E LOTE 7 SECTOR AFILADOR
RUPA RUPA

ANEXO

PLANO ARQUITECTONICO

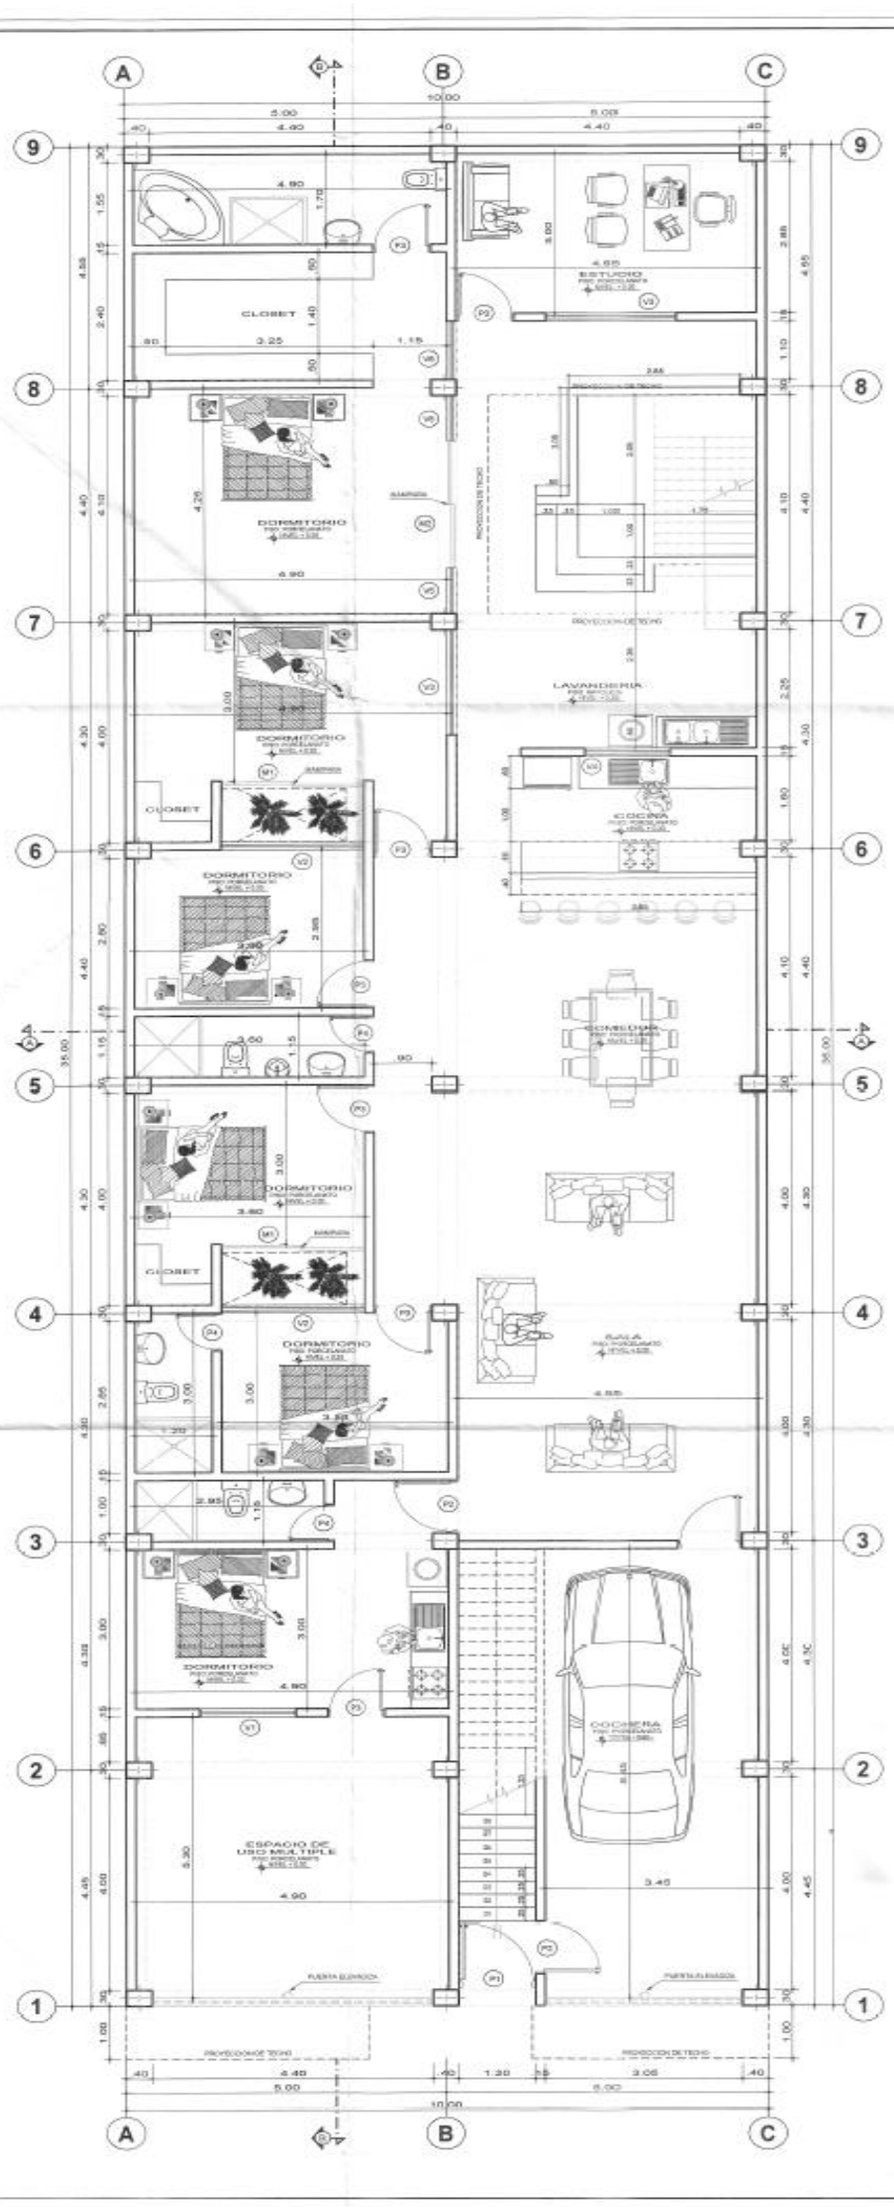

CUADRO DE VANOS PUERTAS

CODIGO	ALFEIZAR	ALTO	ANCHO	OBSERVACIONES
P1	–	3.00	1.20	Puerta de madera
P2	–	2.50	1.00	Puerta contraplacada
P3	–	2.50	0.80	Puerta contraplacada
P4	–	2.20	0.70	Puerta contraplacada

CUADRO DE VANOS VENTANAS

CODIGO	ALFEIZAR	ALTO	ANCHO	OBSERVACIONES
V1	1.00	1.85	1.10	Aluminio con vidrio
V2	1.00	1.85	2.20	Aluminio con vidrio
V3	1.00	1.85	2.80	Aluminio con vidrio
V4	1.00	1.85	1.30	Aluminio con vidrio
V5	—	3.00	0.55	Aluminio con vidrio
V6	1.00	1.85	1.10	Aluminio con vidrio
V7	1.85	1.00	1.00	Aluminio con vidrio
V8	1.85	1.00	1.10	Aluminio con vidrio
V9	1.40	1.00	1.95	Aluminio con vidrio
V10	2.00	0.55	0.70	Aluminio con vidrio
V11	1.85	1.00	1.00	Aluminio con vidrio
V12	1.85	1.00	1.20	Aluminio con vidrio
V13	1.85	1.00	1.85	Aluminio con vidrio
V14	1.85	1.00	2.30	Aluminio con vidrio
V15	1.85	1.00	1.00	Aluminio con vidrio
V16	1.85	1.00	1.00	Aluminio con vidrio

CUADRO DE VANOS MAMPARAS

CÓDIGO	ALFEIZAR	ALTO	ANCHO	OBSERVACIONES
M1	—	2.85	2.25	Aluminio con vidrio
M2	—	2.85	2.40	Aluminio con vidrio
M3	—	2.85	2.75	Aluminio con vidrio
M4	—	2.85	2.60	Aluminio con vidrio
M5	—	2.85	2.30	Aluminio con vidrio

CUADRO DE VANOS PORTON

CODIGO	ALFEIZAR	ALTO	ANCHO	OBSERVACIONES
PT1	–	3.50	4.40	Puerton de fierro y alambre
PT2	–	3.50	3.05	Puerton de fierro y alambre

PRIMERA PLANTA

ESC : 1/50

CONSTRUCTORA Y ASESORES

PROYECTO: VIVIENDA MULTIFAMILIAR

PROPIETARIOS: JEENS RONAL MALPARTIDA PACHECO

UBICACIÓN DEL PREDIO:
PAIS: PERU | DEPARTAMENTO: HUANUCO
PROVINCIA: LEONCIO PRADO | DISTRITO: RUPA - RUPA
DIRECCION: SECTOR AVICO, MZ "D" LOTE "F" - SECTOR AFILADOR

DISEÑO: VENEGAS GRANADOS, Alex Elio Ibrahimer Jaiross
Cel: 926781474 / Correo: venegas2296@gmail.com

ESPECIALIDAD: ARQUITECTURA
PLANO: DISTRIBUCION

ESCALA:	CODIGO:	NUMERO DE LAMINA:
1/50	A-1	01/17

FECHA: SETIEMBRE 2022

FIRMA Y SELLO:

ANEXO

PRESUPUESTO

HOMERO ALFONSO ZELADA TORRES
INGENIERO CIVIL-VERIFICADOR COMUN CIV N° 007426VCZRVIII
Proyectos – Ejecución – Obras Hidráulicas – Agua – Alcantarillado

VALORIZACIÓN DE EJECUCION DE OBRA

OBRA: CONSTRUCCION DE EDIFICACION PARA VIVIENDA
PROPIETARIO: JEENS RONEL MALPARTIDA PACHECO
FECHA SETIEMBRE DEL 2025

PRESUPUESTO DE OBRA: **551,822.70**

PARTIDA	DESCRIPCION	PRESUPUESTO	AVANCE		
			ACTUAL	ACUMULADO	SALDO
		Parcial S/.	Valorizado S/.	Valorizado S/.	Valorizado S/.
04.01.01	INODORO DE COLOR CON ACCESORIOS COMPLETOS	8,525.92		0.00	8,525.92
04.01.02	LAVATORIO DE COLOR 1 LLAVE C/ACCESORIOS	2,400.00		0.00	2,400.00
04.01.03	COLOCACION DE APARATOS SANITARIOS	4,007.68		0.00	4,007.68
04.02	**SISTEMA DE AGUA FRIA Y CONTRA INCENDIO**				
04.02.01	SALIDA DE AGUA FRIA CON TUBERIA DE PVC-SAP 1/2"	1,951.80		0.00	1,951.80
04.02.02	TUBERIA PVC SAP CLASE 10, 1/2"	952.20		0.00	952.20
04.02.03	TUBERIA PVC SAP CLASE 10, 3/4" - LINEA DE ALIMENTACION	1,421.20		0.00	1,421.20
04.02.04	CODO PVC SAP Ø1/2"X90°	651.60		0.00	651.60
04.02.05	TEE PVC SAP DE 3/4"	453.60		0.00	453.60
04.02.06	REDUCCION PVC SAP DE 3/4"x1/2"	225.92		0.00	225.92
04.02.07	VALVULA DE COMPUERTA Ø 1/2" DE BRONCE	1,630.24		0.00	1,630.24
04.03	**SISTEMA DE DESAGUE Y VENTILACION**				
04.03.01	SALIDA DE DESAGÜE PVC 2"	863.20		0.00	863.20
04.03.02	SALIDA DE DESAGÜE PVC 4"	1,125.92		0.00	1,125.92
04.03.03	TUBERIA PVC SAL DE 4"	5,126.40		0.00	5,126.40
04.03.04	TUBERIA PVC SAL DE 2"	1,293.50		0.00	1,293.50
04.03.05	CODO PVC SAL 2"X45°	421.44		0.00	421.44
04.03.06	YEE PVC SAL 4"	453.44		0.00	453.44
04.03.07	SUMIDERO DE BRONCE DE 2"	967.20		0.00	967.20
04.03.08	REGISTRO DE BRONCE DE 4"	1,172.96		0.00	1,172.96
04.03.09	CAJA DE REGISTRO 12" X 24" P/DESAGUE	498.62		0.00	498.62
	COSTO DIRECTO	**551,822.70**	**248,116.01**	**248,116.01**	**303,706.69**
	VALORIZACION EJECUTADA		**44.96%**	**44.96%**	**55.04%**

RESUMEN DE EJECUCION VALORIZADA

DESCRIPCIÓN	PARCIAL	
VALOR DEL AVANCE EJECUTADO	S/	248,116.01
VALOR DEL SALDO POR EJECUTAR	S/	303,706.69
TOTAL PRESUPUESTO	S/	551,822.70

IX.- DESCRIPCION TOPOGRAFICA:

El terreno es de superficie plana, de forma irregular, suelo resistente a la carga limitada, cuenta con instalaciones de las redes de agua, fluido eléctrico, sin desagüe y con vías de acceso debidamente pavimentadas.

Tingo María, setiembre del 2025

Homero Alfonso Zelada Torres
INGENIERO CIVIL
Reg. Cip. N° 117714

ANEXO

PRESUPUESTO

HOMERO ALFONSO ZELADA TORRES
INGENIERO CIVIL-VERIFICADOR COMUN CIV N° 007426VCZRVIII
Proyectos – Ejecución – Obras Hidráulicas – Agua – Alcantarillado

PRESUPUESTO DE OBRA

I.-PROPIETARIO: JEENS RONEL MALPARTIDA PACHECO

II.- UBICACIÓN DEL INMUEBLE:

LOTE N°	: 7
MANZANA	: E
LOTIZACION	: BUENOS AIRES
SECTOR	: AFILADOR
DISTRITO	: RUPA RUPA
PROVINCIA	: LEONCIO PRADO.
DEPARTAMENTO	: HUANUCO.

III.-OBJETIVO: VALORIZACION DE OBRA

IV.- ANTECEDENTES:

El Sr. JEENS RONEL MALPARTIDA PACHECO es propietario del lote de terreno ubicado en la Lotizacion Buenos Aires con frente a la Carretera Tingo Maria-Huanuco Mz. "E" lote N° 7 Sector Afilador del Distrito de Rupa Rupa, Provincia de Leoncio Prado, Departamento de Huánuco,adquirido por donación de su anterior propietaria Alejandra Rojas Espinoza,con fecha 4 de mayo del 2,021 e inscrito en la Oficina Registral de Tingo Maria con la Partida Electronica No. 11033233.

V.- AREA, LINDEROS Y MEDIDAS PERIMETRICAS:

- Por el frente, con la carretera Tingo María - Huánuco, con.....10.00 ml.
- Por la derecha entrando, con el lote N° 6, con.....34.00ml.
- Por la izquierda entrando, con el lote N° 24 y 25, con.....36.00 ml.
- Por el fondo, con el lote N° 30 con.....10.00 ml.

AREA: 350.00 M2 **PERIMETRO: 90.00 ML.**

VI.- CARACTERISTICAS DEL INMUEBLE:

Se trata de la construcción de la primera planta de una vivienda multifamiliar con las siguientes características:

- La primera planta cuenta con tres puertas de ingreso,dos son elevadizas uno para uso multiple y el otro como cochera y la tercera como ingreso principal,este ultimo conduce también a una escalera que lleva al segundo piso,hacia el fondo lado derecho es la sala-comedor cocina,área de lavandería,unducto de entilacion para la piscina y un cuarto de estudio,hacia el lado derecho cuenta con seis dormitorios,tres dormitorios con baño común y tres dormitorios con baño propio.

Av. Tito Jaime F. Nº 672 – Tingo María – Huánuco (062-561348) (962604315)
Av. José Granda Nº 2160 – SMP. – Lima 980835631 - 994848660 - RPM *996245
E-mail: const.hazt@hotmail.com

Homero Alfonso Zelada Torres
INGENIERO CIVIL
Reg. Cip. N° 117714

ANEXO

PRESUPUESTO

HOMERO ALFONSO ZELADA TORRES
INGENIERO CIVIL-VERIFICADOR COMUN CIV N° 007426VCZRVIII
Proyectos – Ejecución – Obras Hidráulicas – Agua – Alcantarillado

Presupuesto

Presupuesto **CONSTRUCCION DE EDIFICACION PRIMERA PLANTA**
Cliente **JEENS RONEL MALPARTIDA PACHECO**
Lugar **HUANUCO - LEONCIO PRADO - RUPA-RUPA - Mz E - Lote 7 - Buenos Aires - Sector Afilador**

Item	Descripción	Und.	Metrado	Precio S/.	Parcial S/.
01.04.05.02	ENCOFRADO Y DESENCOFRADO EN LOSA ALIGERADA	m2	347.51	55.37	19,241.63
01.04.05.03	ACERO fy=4200 kg/cm2 GRADO 60 EN LOSA ALIGERADA	kg	1,842.70	5.31	9,784.74
01.04.05.04	LADRILLO HUECO DE ARCILLA DE 15x30x30 cm	u	2,896.00	2.33	6,747.68
01.04.06	**ESCALERAS**				**4,398.47**
01.04.06.01	CONCRETO EN ESCALERA f'c=210 kg/cm2	m3	2.54	486.51	1,235.74
01.04.06.02	ENCOFRADO Y DESENCOFRADO EN ESCALERA	m2	17.78	105.38	1,873.66
01.04.06.03	ACERO EN ESCALERA fy = 4200 kg/cm2 GRADO 60	kg	243.68	5.29	1,289.07
01.04.07	**CISTERNA**				**5,165.68**
01.04.07.01	CONCRETO EN CISTERNA f'c=210 kg/cm2	m3	3.14	546.50	1,716.01
01.04.07.02	ENCOFRADO Y DESENCOFRADO EN CISTERNA	m2	31.20	74.54	2,325.65
01.04.07.03	ACERO fy=4200 kg/cm2 GRADO 60 EN CISTERNA	kg	211.68	5.31	1,124.02
02	**ARQUITECTURA**				**174,174.47**
02.01	**MUROS Y TABIQUES DE ALBAÑILERIA**				**37,499.39**
02.01.01	MURO DE SOGA LADRILLO DE ARCILLA COCIDA 9x13x23 CEMENTO ARENA 1:4 DE 1.5 cm	m2	622.81	60.21	37,499.39
02.02	**REVOQUES, ENLUCIDOS Y MOLDURAS**				**54,497.30**
02.02.01	TARRAJEO EN INTERIORES MORTERO C:A 1:5	m2	1,150.00	29.18	33,557.00
02.02.02	TARRAJEO EN IEXTERIORES MORTERO C:A 1:5, INC. BRUÑAS	m2	510.00	35.13	17,916.30
02.02.03	VESTIDURA DE DERRAMES	m	240.00	12.60	3,024.00
02.03	**PISOS Y PAVIMENTOS**				**21,859.60**
02.03.01	PISO CERAMICO DE 30 X 30 CM	m2	296.00	73.85	21,859.60
02.04	**CONTRAZOCALOS**				**14,753.93**
02.04.01	CONTRAZOCALO CEMENTO SIN COLOREAR H = 20 cm	m	312.00	12.11	3,778.32
02.04.02	ZOCALO DE CERAMICO DE 0.30 X 0.30	m2	95.20	115.29	10,975.61
02.05	**CARPINTERIA DE MADERA**				**18,057.40**
02.05.01	PUERTA DE MADERA CAOBA	m2	20.00	515.35	10,307.00
02.05.02	PUERTA CONTRAPLACADA (INC. MARCO)	m2	15.00	331.04	4,965.60
02.05.03	VENTANA DE MADERA CON HOJAS DE CAOBA	m2	20.00	139.24	2,784.80
02.06	**CERRAJERIA**				**4,858.40**
02.06.01	BISAGRA CAPUCHINA DE 3" X 3"	u	96.00	12.01	1,152.96
02.06.02	CERRADURA FORTE 3 GOLPES - EXTERIOR	u	16.00	120.09	1,921.44
02.06.03	CERRADURA DE INTERIORES TIPO BOLA	u	16.00	85.13	1,362.08
02.06.04	MANIJA DE BRONCE PARA PUERTAS	u	16.00	26.37	421.92
02.07	**VIDRIOS, CRISTALES Y SIMILARES**				**1,592.00**
02.07.01	VIDRIO BRONCE 6 MM	p2	200.00	7.96	1,592.00
02.08	**PINTURA**				**21,056.45**
02.08.01	PINTURA EN MUROS INTERIORES AL LATEX	m2	1,150.00	11.50	13,225.00
02.08.02	PINTURA EN MUROS EXTERIORES AL LATEX	m2	510.00	14.36	7,323.60
02.08.03	PINTURA BARNIZ EN PUERTAS DE MADERA	m2	35.00	14.51	507.85
03	**INSTALACIONES ELECTRICAS**				**18,765.04**
03.01	**SALIDAS**				**9,535.00**
03.01.01	SALIDA PARA CENTROS DE LUZ	pto	40.00	103.75	4,150.00
03.01.02	SALIDA PARA TOMACORRIENTE DOBLE PVC	pto	40.00	75.39	3,015.60
03.01.03	SALIDA PARA INTERRUPTOR DOBLE	pto	30.00	78.98	2,369.40
03.02	**TABLEROS Y/O CUCHILLAS**				**1,676.04**
03.02.01	TABLERO GENERAL DE DISTRIBUCION METALICO	u	2.00	475.15	950.30
03.02.02	INTERRUPTOR THERMOMAGNETICO EN TABLERO	u	2.00	362.87	725.74

Av. Tito Jaime F. Nº 672 – Tingo María – Huánuco (062-561348) (962604315)
Av. José Granda N° 2160 – SMP. – Lima 980835631 - 994848660 - RPM *996245
E-mail: const.hazt@hotmail.com

Homero Alfonso Zelada Torres
INGENIERO CIVIL
Reg. Cip. N° 117714

ANEXO

PRESUPUESTO

HOMERO ALFONSO ZELADA TORRES
INGENIERO CIVIL-VERIFICADOR COMUN CIV N° 007426VCZRVIII
Proyectos – Ejecución – Obras Hidráulicas – Agua – Alcantarillado

Presupuesto

Presupuesto **CONSTRUCCION DE EDIFICACION PRIMERA PLANTA**
Cliente **JEENS RONEL MALPARTIDA PACHECO**
Lugar **HUANUCO - LEONCIO PRADO - RUPA-RUPA - Mz E - Lote 7 - Buenos Aires - Sector Afilador**

Item	Descripción	Und.	Metrado	Precio S/.	Parcial S/.
03.03	**ARTEFACTOS**				**7,554.00**
03.03.01	ARTEFACTO 02 FLUORESCENTES 1 X 40 W INCLUYE EQUIPO Y PANTALLA	u	40.00	188.85	7,554.00
04	**INSTALACIONES SANITARIAS**				**34,142.84**
04.01	**APARATOS Y ACCESORIOS SANITARIOS**				**14,933.60**
04.01.01	INODORO DE COLOR CON ACCESORIOS COMPLETOS	u	16.00	532.87	8,525.92
04.01.02	LAVATORIO DE COLOR 1 LLAVE C/ACCESORIOS	u	16.00	150.00	2,400.00
04.01.03	COLOCACION DE APARATOS SANITARIOS	u	32.00	125.24	4,007.68
04.02	**SISTEMA DE AGUA FRIA Y CONTRA INCENDIO**				**7,286.56**
04.02.01	SALIDA DE AGUA FRIA CON TUBERIA DE PVC-SAP 1/2"	pto	20.00	97.59	1,951.80
04.02.02	TUBERIA PVC SAP CLASE 10, 1/2"	m	90.00	10.58	952.20
04.02.03	TUBERIA PVC SAP CLASE 10, 3/4" - LINEA DE ALIMENTACION	m	110.00	12.92	1,421.20
04.02.04	CODO PVC SAP Ø1/2"X90°	u	45.00	14.48	651.60
04.02.05	TEE PVC SAP DE 3/4"	u	30.00	15.12	453.60
04.02.06	REDUCCION PVC SAP DE 3/4"x1/2"	u	16.00	14.12	225.92
04.02.07	VALVULA DE COMPUERTA Ø 1/2" DE BRONCE	u	16.00	101.89	1,630.24
04.03	**SISTEMA DE DESAGUE Y VENTILACION**				**11,922.68**
04.03.01	SALIDA DE DESAGÜE PVC 2"	pto	16.00	53.95	863.20
04.03.02	SALIDA DE DESAGÜE PVC 4"	pto	16.00	70.37	1,125.92
04.03.03	TUBERIA PVC SAL DE 4"	m	90.00	56.96	5,126.40
04.03.04	TUBERIA PVC SAL DE 2"	m	50.00	25.87	1,293.50
04.03.05	CODO PVC SAL 2"X45°	u	16.00	26.34	421.44
04.03.06	YEE PVC SAL 4"	u	16.00	28.34	453.44
04.03.07	SUMIDERO DE BRONCE DE 2"	u	16.00	60.45	967.20
04.03.08	REGISTRO DE BRONCE DE 4"	u	16.00	73.31	1,172.96
04.03.09	CAJA DE REGISTRO 12" X 24" P/DESAGUE	u	2.00	249.31	498.62
	TOTAL PRESUPUESTO				**551,822.70**

Valor de la edificación = S/. 551,822.70

Homero Alfonso Zelada Torres
INGENIERO CIVIL
Reg. Cip. N° 117714

Av. Tito Jaime F. N° 672 – Tingo María – Huánuco (062-561348) (962604315)
Av. José Granda N° 2160 – SMP. – Lima 980835631 - 994848660 - RPM *996245
E-mail: const.hazt@hotmail.com

ANEXO

PRESUPUESTO

HOMERO ALFONSO ZELADA TORRES
INGENIERO CIVIL-VERIFICADOR COMUN CIV N° 007426VCZRVIII
Proyectos – Ejecución – Obras Hidráulicas – Agua – Alcantarillado

VIII.- AVANCE EJECUTADO Y SALDOS DE OBRA

VALORIZACIÓN DE EJECUCION DE OBRA

OBRA: CONSTRUCCION DE EDIFICACION PARA VIVIENDA
PROPIETARIO: JEENS RONEL MALPARTIDA PACHECO
FECHA SETIEMBRE DEL 2025

PRESUPUESTO DE OBRA: **551,822.70**

PARTIDA	DESCRIPCION	PRESUPUESTO	AVANCE		
			ACTUAL	ACUMULADO	SALDO
		Parcial S/.	Valorizado S/.	Valorizado S/.	Valorizado S/.
01	ESTRUCTURAS				
01.01	**TRABAJOS PRELIMINARES**				
01.01.01	LIMPIEZA DE TERRENO MANUAL	1,298.50	1,298.50	1,298.50	0.00
01.01.02	TRAZO, NIVELACION Y REPLANTEO	668.50	66.85	66.85	601.65
01.02	**MOVIMIENTO DE TIERRAS**				
01.02.01	EXCAVACION DE ZANJAS PARA ZAPATAS	9,138.15	9,138.15	9,138.15	0.00
01.02.02	EXCAVACION DE ZANJAS PARA CIMIENTOS	4,638.78	4,638.78	4,638.78	0.00
01.02.03	RELLENO COMPACTADO CON MATERIAL PROPIO	2,010.05	2,010.05	2,010.05	0.00
01.02.04	ELIMINACION DE MATERIAL EXCEDENTE (CARGUIO A MANO)	15,538.50	15,538.50	15,538.50	0.00
01.02.05	NIVELACION INTERIOR Y APISONADO PREVIO P/FALSO PISO	1,833.09	0.00	0.00	1,833.09
01.03	**OBRAS DE CONCRETO SIMPLE**				
01.03.01	SOLADO EN ZAPATA C:H / 1:10 E=4"	4,458.43	4,458.43	4,458.43	0.00
01.03.02	CIMIENTOS CORRIDOS MEZCLA 1:10 CEMENTO HORMIGON + 30% P.G.	12,462.64	12,462.64	12,462.64	0.00
01.03.03	FALSO PISO DE 4" DE CONCRETO 1:10	12,736.43	0.00	0.00	12,736.43
01.03.04	SOBRECIMIENTOS e=0.15m. MEZCLA 1:8 CEMENTO HORMIGON + 25% PM	8,982.16	5,988.11	5,988.11	2,994.05
01.03.05	ENCOFRADO Y DESENCOFRADO - SOBRECIMIENTO	10,273.91	6,849.08	6,849.08	3,424.83
01.04	**OBRAS DE CONCRETO ARMADO**				
01.04.01	**ZAPATAS**				
01.04.01.01	CONCRETO EN ZAPATAS f'c=210 kg/cm2	32,797.91	27,687.61	27,687.61	5,110.30
01.04.01.02	ACERO fy=4200 kg/cm2 EN ZAPATAS	10,227.06	9,165.06	9,165.06	1,062.00
01.04.02	**VIGAS DE CIMENTACION**				
01.04.02.01	CONCRETO EN VIGAS DE CIMENTACION f'c = 210 kg/cm2	6,685.31	5,347.39	5,347.39	1,337.92
01.04.02.02	ENCOFRADO Y DESENCOFRADO EN VIGAS DE CIMENTACION	6,951.56	5,561.25	5,561.25	1,390.31
01.04.02.03	ACERO fy=4200 kg/cm2 GRADO 60 EN VIGAS DE CIMENTACION	12,680.86	12,680.86	12,680.86	0.00
01.04.03	**COLUMNAS**				
01.04.03.01	CONCRETO f'c=210 kg/cm2 EN COLUMNAS	10,782.73	9,959.54	9,959.54	823.19
01.04.03.02	ENCOFRADO Y DESENCOFRADO DE COLUMNAS	13,622.40	12,582.52	12,582.52	1,039.88
01.04.03.03	ACERO fy=4200 kg/cm2 GRADO 60 EN COLUMNAS	17,954.38	16,762.40	16,762.40	1,191.99
01.04.04	**VIGAS**				
01.04.04.01	CONCRETO f'c=210 kg/cm2 EN VIGAS	13,350.71	9,191.61	9,191.61	4,159.10
01.04.04.02	ENCOFRADO Y DESENCOFRADO EN VIGAS	23,633.29	17,098.89	17,098.89	6,534.40
01.04.04.03	ACERO fy=4200 kg/cm2 GRADO 60 EN VIGAS	32,127.44	24,777.44	24,777.44	7,350.00
01.04.05	**LOSA ALIGERADA**				
01.04.05.01	CONCRETO f'c=210 kg/cm2 EN LOSA ALIGERADA	14,549.36	0.00	0.00	14,549.36
01.04.05.02	ENCOFRADO Y DESENCOFRADO EN LOSA ALIGERADA	19,241.63	0.00	0.00	19,241.63
01.04.05.03	ACERO fy=4200 kg/cm2 GRADO 60 EN LOSA ALIGERADA	9,784.74	0.00	0.00	9,784.74
01.04.05.04	LADRILLO HUECO DE ARCILLA DE 15x30x30 cm	6,747.68	0.00	0.00	6,747.68
01.04.06	**ESCALERAS**				
01.04.06.01	CONCRETO EN ESCALERA f'c=210 kg/cm2	1,235.74	1,235.74	1,235.74	0.00
01.04.06.02	ENCOFRADO Y DESENCOFRADO EN ESCALERA	1,873.66	1,873.66	1,873.66	0.00

Av. Tito Jaime F. Nº 672 – Tingo María – Huánuco (062-561348) (962604315)
Av. José Granda Nº 2160 – SMP. – Lima 980835631 - 994848660 - RPM *996245
E-mail: const.hazt@hotmail.com

Homero Alfonso Zelada Torres
INGENIERO CIVIL
Reg. Cip. Nº 117714

ANEXO

PRESUPUESTO

HOMERO ALFONSO ZELADA TORRES
INGENIERO CIVIL-VERIFICADOR COMUN CIV N° 007426VCZRVIII
Proyectos – Ejecución -- Obras Hidráulicas – Agua – Alcantarillado

VALORIZACIÓN DE EJECUCION DE OBRA

OBRA: CONSTRUCCION DE EDIFICACION PARA VIVIENDA
PROPIETARIO: JEENS RONEL MALPARTIDA PACHECO
FECHA SETIEMBRE DEL 2025

PRESUPUESTO DE OBRA: **551,822.70**

PARTIDA	DESCRIPCION	PRESUPUESTO	AVANCE		
			ACTUAL	ACUMULADO	SALDO
		Parcial S/.	Valorizado S/.	Valorizado S/.	Valorizado S/.
01.04.06.03	ACERO EN ESCALERA fy = 4200 kg/cm2 GRADO 60	1,289.07	1,289.07	1,289.07	0.00
01.04.07	**CISTERNA**				
01.04.07.01	CONCRETO EN CISTERNA f'c=210 kg/cm2	1,716.01	1,716.01	1,716.01	0.00
01.04.07.02	ENCOFRADO Y DESENCOFRADO EN CISTERNA	2,325.65	2,325.65	2,325.65	0.00
01.04.07.03	ACERO fy=4200 kg/cm2 GRADO 60 EN CISTERNA	1,124.02	1,124.02	1,124.02	0.00
02	**ARQUITECTURA**				
02.01	**MUROS Y TABIQUES DE ALBAÑILERIA**				
02.01.01	MURO DE SOGA LADRILLO DE ARCILLA COCIDA 9x13x23 CEMENTO ARENA 1:4 DE 1.5 cm	37,499.39	25,288.20	25,288.20	12,211.19
02.02	**REVOQUES, ENLUCIDOS Y MOLDURAS**				
02.02.01	TARRAJEO EN INTERIORES MORTERO C:A 1:5	33,557.00	0.00	0.00	33,557.00
02.02.02	TARRAJEO EN IEXTERIORES MORTERO C:A 1:5, INC. BRUÑAS	17,916.30	0.00	0.00	17,916.30
02.02.03	VESTIDURA DE DERRAMES	3,024.00	0.00	0.00	3,024.00
02.03	**PISOS Y PAVIMENTOS**				
02.03.01	PISO CERAMICO DE 30 X 30 CM	21,859.60	0.00	0.00	21,859.60
02.04	**CONTRAZOCALOS**				
02.04.01	CONTRAZOCALO CEMENTO SIN COLOREAR H = 20 cm	3,778.32	0.00	0.00	3,778.32
02.04.02	ZOCALO DE CERAMICO DE 0.30 X 0.30	10,975.61	0.00	0.00	10,975.61
02.05	**CARPINTERIA DE MADERA**				
02.05.01	PUERTA DE MADERA CAOBA	10,307.00	0.00	0.00	10,307.00
02.05.02	PUERTA CONTRAPLACADA (INC. MARCO)	4,965.60	0.00	0.00	4,965.60
02.05.03	VENTANA DE MADERA CON HOJAS DE CAOBA	2,784.80	0.00	0.00	2,784.80
02.06	**CERRAJERIA**				
02.06.01	BISAGRA CAPUCHINA DE 3" X 3"	1,152.96	0.00	0.00	1,152.96
02.06.02	CERRADURA FORTE 3 GOLPES - EXTERIOR	1,921.44	0.00	0.00	1,921.44
02.06.03	CERRADURA DE INTERIORES TIPO BOLA	1,362.08	0.00	0.00	1,362.08
02.06.04	MANIJA DE BRONCE PARA PUERTAS	421.92	0.00	0.00	421.92
02.07	**VIDRIOS, CRISTALES Y SIMILARES**				
02.07.01	VIDRIO BRONCE 6 MM	1,592.00	0.00	0.00	1,592.00
02.08	**PINTURA**				
02.08.01	PINTURA EN MUROS INTERIORES AL LATEX	13,225.00	0.00	0.00	13,225.00
02.08.02	PINTURA EN MUROS EXTERIORES AL LATEX	7,323.60	0.00	0.00	7,323.60
02.08.03	PINTURA BARNIZ EN PUERTAS DE MADERA	507.85	0.00	0.00	507.85
03	**INSTALACIONES ELECTRICAS**				
03.01	**SALIDAS**				
03.01.01	SALIDA PARA CENTROS DE LUZ	4,150.00		0.00	4,150.00
03.01.02	SALIDA PARA TOMACORRIENTE DOBLE PVC	3,015.60		0.00	3,015.60
03.01.03	SALIDA PARA INTERRUPTOR DOBLE	2,369.40		0.00	2,369.40
03.02	**TABLEROS Y/O CUCHILLAS**				
03.02.01	TABLERO GENERAL DE DISTRIBUCION METALICO	950.30		0.00	950.30
03.02.02	INTERRUPTOR THERMOMAGNETICO EN TABLERO	725.74		0.00	725.74
03.03	**ARTEFACTOS**				
03.03.01	ARTEFACTO 02 FLUORESCENTES 1 X 40 W INCLUYE EQUIPO Y PANTALLA	7,554.00		0.00	7,554.00
04	**INSTALACIONES SANITARIAS**				
04.01	**APARATOS Y ACCESORIOS SANITARIOS**				

Av. Tito Jaime F. Nº 672 – Tingo María – Huánuco (062-561348) (962604315)
Av. José Granda Nº 2160 – SMP. – Lima 980835631 - 994848660 - RPM *996245
E-mail: const.hazt@hotmail.com

Homero Alfonso Zelada Torres
INGENIERO CIVIL
Reg. Cip. N° 117714

ANEXO

LICENCIA DE EDIFICACION

"AÑO DEL BICENTENARIO DE LA CONSOLIDACIÓN DE NUESTRA INDEPENDENCIA Y DE LA CONMEMORACIÓN DE LAS HEROICAS BATALLAS DE JUNÍN Y AYACUCHO"

EXPEDIENTE N°	:	202417702 (18/06/2024).
FECHA DE EMISION	:	11/07/2024
FECHA DE VENCIMIENTO	:	11/07/2027

RESOLUCION DE LICENCIA DE EDIFICACION N°: 042 - 2024

ADMINISTRADO: SR. JEENS RONEL MALPARTIDA PACHECO **PROPIETARIOS:** X **SI** ☐ **NO**

DNI N° 44893228

LICENCIA DE: LICENCIA DE EDIFICACION – MODALIDAD "B"

USO: VIVIENDA UNIFAMILIAR **ZONIFICACION:** RDM **ALTURA:** --- ml / 3 pisos

UBICACIÓN DEL INMUEBLE:

Departamento	Provincia	Distrito						
HUANUCO	LEONCIO PRADO	RUPA RUPA						
Urbanización / A.H./Otro	Mz.	Lote	Sub lote	Av. / Jr. / Calle / Pasaje		N°		Int.
AA.HH. CESAR VALLEJO	B	24		PASAJE VIOLETA		-----		---

AREA TOTAL A CONSTRUIR : 166.83 m2

TOTAL N° PISOS: 1

N° Sótano (s)

Semisotano

Azotea

MUNICIPALIDAD PROVINCIAL DE LEONCIO PRADO
TINGO MARIA
Ing. Civil Katssel Macario Malpartida Pino
GERENTE DE INFRAESTRUCTURA Y ACONDICIONAMIENTO

RESPONSABLE DEL PROYECTO: ARQ. ALEX BRENHNER JUNIORS VENEGAS GRANADOS **REGISTRO CAP/CIP:** CAP Nº 29508

VALOR DE LA OBRA:	**S/.**	135,537.64		
DERECHO DE TRAMITE:	**S/.**	**91.50**	**RECIBO Nº:**	**00203392024**
DERECHO DE LICENCIA:	**S/.**	**813.22**	**RECIBO Nº:**	**00214722024**

OBSERVACIONES:

- ESTA LICENCIA NO AUTORIZA EL USO DE LA VIA PUBLICA PARA DEPOSITAR AGREGADOS, EL REFERIDO PERMISO DEBERA SER TRAMITADO, PREVIO AL INICIO DE LA OBRA, SUJETO A LAS SANCIONES DISPUESTAS EN LA NORMATIVA VIGENTE.

- LA DISTANCIAS MINIMAS DE SEGURIDAD HORIZONTAL Y VERTICAL SON DE 2.5M Y 4M RESPECTIVAMENTE, SEGUN LA TABLA 234-1 DEL CODIGO NACIONAL DE ELECTRICIDAD.

- LA OBRA A EDIFICARSE DEBERA AJUSTARSE AL PROYECTO PRESENTADO Y APROBADO, CUALQUIER MODIFICACION QUE SE INTRODUZCA SIN APROBACION MUNICIPAL DEJARA AUTOMATICAMENTE SIN EFECTO.

- COMUNIQUE OPORTUNAMENTE EL INICIO DE LA EJECUCION DE LA OBRA, ADJUNTANDO EL ANEXO H – INICIO DE OBRA: CASO CONTRARIO, SE ACTUARA DE ACUERDO CON EL CUADRO UNICO DE INFRACCIONES Y SANCIONES – CUIS.

-LA EXPEDICION DE LAS CITADAS LICENCIAS NO CONLLEVA A PRONUNCIAMIENTO ALGUNO ACERCA DE LA TITULARIDAD DE LOS DERECHOS REALES, SOBRE EL PREDIO O PREDIOS, OBJETO DE ELLA.

1. Cuando el administrado no sea el propietario, debe indicarse en observaciones los datos del propietario (nombre completo, documento de identidad)

2. A excepción de las obras preliminares, para el inicio de la ejecución de la(s) obra (s) autorizada(s) con la Licencia, el administrado debe presentar el Anexo H.

3. La obra a ejecutarse debe ajustarse al proyecto autorizado. Ante cualquier modificación sustancial que se efectúe sin autorización, la Municipalidad puede disponer la adopción de medidas provisionales de inmediata ejecución previstas en el numeral 6 del artículo 10 de la Ley N° 29090, Ley de Regulación de Habilitaciones Urbanas y de Edificaciones.

4. La Licencia tiene una vigencia de 36 meses prorrogable por única vez por 12 meses, debiendo ser solicitada dentro de los 30 días calendarios anteriores a su vencimiento.

N° de Solicitud Banco **1290029**

SOLICITUD CONSTRUYO

1. Nombre del cliente:

JEENS RONEL MALPARTIDA PACHECO

2. Dirección del inmueble o ubicación (indicar referencias):

AV. AFILADOR S/n MZ. E LT. 7 SECTOR AFILADOR RUPA RUPA - LEONCIO PRADO - HUANUCO

3. N° de Partida Electrónica / Copia Literal (documentación registral):

11033233

4. Cuadro de áreas (disgregar por pisos, áreas construidas existentes y nuevas) :

	ÁREAS TECHADAS (Existentes)	ÁREAS TECHADAS (Nuevas)
PRIMER PISO		380.00
SEGUNDO PISO		
TERCER PISO		
CUARTO PISO		
ÁREA TOTAL	**0.00**	**380.00**

5. Detalle del financiamiento (indicar si se va a financiar todos los niveles, solo en casco gris, los primeros dos pisos ,etc)

FINANCIADO PRIMER PISO

6. Descripción del proyecto:

CONSTRUCCION VIVIENDA DEL PRIMER PISO DIVIDIDO EN SALA, COMEDOR, COCHERA, BAÑO, LAVANDERIA

7. Presupuesto global por especialidades (Soles):

PARTIDAS DE LA CONSTRUCCIÓN	VALOR (S/.)
Estructura	324,740.35
Arquitectura	174,174.47
Instalaciones Sanitarias	18,765.04
Instalaciones Eléctricas	
Instalaciones Mecánicas	
Sub Total	517,679.86
Utilidad 7%	34,142.84
Gastos Generales	
IGV	
TOTAL	**551,822.70**

8. Fecha de finalización de obra estimada:

10 meses