
Layseca Asociados

N° de Solicitud Banco	**1364852**
N° de Servicio Tasadora	**60347-2026**
Fecha de Expedición	30-Abr-2026
Fecha de Caducidad	30-Abr-2027

BANCO BBVA PERU

1ER CONSTRUYO

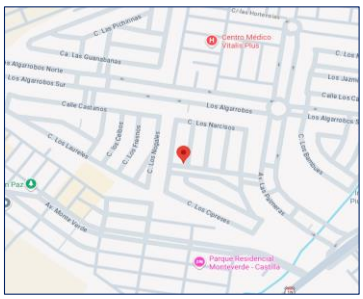





Tipo de Tasación	Hipotecaria	Nueva		**N° de Garantía**	
Solicitante	BBVA CONTINENTAL	OF.	MDO. MODELO PIURA	FUNC.	STEFANIA CHAPILLIQUEN
Cliente	SAAVEDRA FEIJOO HEIDY MELISSA				
Propietario (s)	ESPINOZA RAMOS HUGO FERNANDA Y SAAVEDRA FEIJOO HEIDY MELISSA				
Fecha de inspección	29/04/2026				
Dirección Registral	Mz. A11 Lote 19 Urb. Las Palmeras I Etapa, Distrito de Castilla, Provincia de Piura y Departamento de Piura.				
Dirección Municipal	No se contó con documentación.				
Dirección según inspección ocular	Mz. A11 Lote 19 Urb. Las Palmeras I Etapa, Distrito de Castilla, Provincia de Piura y Departamento de Piura.				
Tipo de inmueble	Casa Habitación	**Ocupante**	Desocupado		

Descripción	TIPO DE USO (*)	%	TIPO DE USO (*)	%
	Desocupado	100%		

Zonificación	RDM	**Material de construcción**	Ladrillo		
Año de construcción	2026	**Obra finalizada**	SÍ		NO	X
	*De acuerdo a expediente documental y tipo de construcción predominante				
Área de terreno	192.00 m2	**Área construida**	235.00 m2		
Declaratoria de fábrica	SÍ		NO	X	**Tipo de declaratoria**	TOTAL		PARCIAL	
Cargas	SÍ		NO	X	**Gravámenes**	SÍ		NO	X
Zona de Alta Peligrosidad	SÍ		NO	X	**Zona de Riesgo (Desastre natural)**	SÍ		NO	X
Predio Agrícola	SÍ		NO	X	**Predio Rústico**	SÍ		NO	X

VALORES TOTALES	MONEDA	VALOR TOTAL (REDONDEADO)	TERRENO	EDIFICACION PROYECTADA
VALOR COMERCIAL PROYECTADO	US$	170,000.00	38,400.00	131,600.00
	S/	592,620.00	133,862.40	458,757.60
VALOR DE REALIZACIÓN PROYECTADO	US$	136,000.00	30,720.00	105,280.00
	S/	474,096.00	107,089.92	367,006.08

VALORES INSCRITOS EN RR.PP.	MONEDA	VALOR TOTAL	TERRENO	EDIFICACIÓN
VALOR COMERCIAL	US$	38,400.00	38,400.00	
	S/	133,862.40	133,862.40	
VALOR DE REALIZACIÓN	US$	30,720.00	30,720.00	
	S/	107,089.92	107,089.92	

VALORES NO INSCRITOS EN RR.PP.	MONEDA	VALOR TOTAL	AVANCE DE OBRA	% AVANCE DE OBRA
VALOR COMERCIAL	US$			0.00%
	S/			

VALORES DE RECONSTRUCCIÓN	MONEDA	VALOR TOTAL (VSN PROYECTADO)	VALOR DE RECONSTRUCCIÓN (VSN DEL AVANCE)	(VSN PENDIENTE)	FECHA ESTIMADA DE FINALIZACIÓN
V. RECONSTRUCCIÓN (INCL. CONSTRUCCIONES DECLAR. Y NO DECLAR.)	US$	131,944.73		131,944.73	5 meses despues del primer desembolso
	S/	459,959.33		459,959.33	

Tipo de cambio aplicado 3.486 Soles / Dólar

Observaciones

- Se sustenta la ubicación del inmueble con Visor Base Gráfica de Sunarp, ver anexos.
- Para el presente informe se ha contado con el presupuesto por partida y solicitud de construyo aprobado por el banco, en soles, por lo que se utilizó el Tipo de Cambio del mes proporcionado por el banco.
- El Valor Unitario de Edificación se ha obtenido de dividir el Valor Total en soles del presupuesto alcanzado, además, se ha considerado que este presupuesto ya está aprobado por el banco.
- El área techada de la Edificación, así como las características de los acabados se han obtenido de la memoria descriptiva proporcionada.
- El tiempo de ejecución de obra es de 140 días, apartir del inicio de obra (no indicado).

Advertencias Ninguna.

	Si	No	
Inmueble en zona de riesgo		X	Ubicado en zona urbana, con habilitación urbana completa.

Valor comercial Tasación Anterior US$ ____ S/ ____ FECHA ____ PERITO ____

PERITO	Ing. Manuel Barboza Oviedo
REPEV	N° 02668-2022
CIP	N° 258213

LAYSECA ASOCIADOS SAC
REPEV Nº 2741-2013

PERITO	Arq. Josselyn Sánchez Diaz
REPEV	N° 3041-2024
CAP	N° 29128

Layseca Asociados

N° de Solicitud Banco	**1364852**
N° de Servicio Tasadora	**60347-2026**
Fecha de Expedición	30-Abr-2026
Fecha de caducidad	30-Abr-2027

MEMORIA DESCRIPTIVA

1. ANTECEDENTES

Objeto y Propósito: Estimar el Valor Comercial del inmueble para fines de Garantía Hipotecaria

Alcance y Limitaciones: Durante la visita SI se dieron las facilidades para la inspección ocular y toma de registro fotográfico al interior del inmueble.

Reglamentación: Reglamento Nacional de Tasaciones - R.M. Nº 172-2016-VIVIENDA, Resolución Ministerial N° 424-2017-VIVIENDA (modificación), Resolución Ministerial N° 124-2020-VIVIENDA y Resolución S.B.S N° 11356-2008 para la determinación del valor de realización.

Metodología Empleada: Se utilizan los Métodos Directos (Comparación, Costos) o Indirectos establecidos en el Artículo 3. Inciso 3.1.5 del Título I del Reglamento Nacional de Tasaciones del Perú.

Documentación Proporcionada

X	Partida Registral		Predio Urbano	X	Planos		CRI
	Parámetros Urb.		Tasación anterior		Cuadro de acabados	X	Memoria Des.
X	Otros		Presupuesto				

Titulación e Inscripción	**Principal**	Partida Electrónica	Nº	11163129	Fecha	09/04/2026	Oficina Registral	Piura

2. DATOS GENERALES

Cliente: SAAVEDRA FEIJOO HEIDY MELISSA

Propietario(s): ESPINOZA RAMOS HUGO FERNANDA Y SAAVEDRA FEIJOO HEIDY MELISSA

Fecha de Inspección: 29/04/2026

Ocupante: Desocupado

Georeferencias: Latitud -5.227776° Longitud -80.636854° (*) Datos obtenidos Google Maps

Ubicación según Partida Electrónica: Mz. A11 Lote 19 Urb. Las Palmeras I Etapa, Distrito de Castilla, Provincia de Piura y Departamento de Piura.

Ubicación según el Predio Urbano: No se contó con documentación.

Ubicación Según la Inspección Ocular: Mz. A11 Lote 19 Urb. Las Palmeras I Etapa, Distrito de Castilla, Provincia de Piura y Departamento de Piura.

3. CONDICIONES URBANISTICAS DEL ENTORNO

Características del Sector y del Entorno

Tipo de Zona	Urbana	Demanda / Interés	Media
Uso Predominante	Vivienda	Zonificación	RDM
Desarrollo	Estacionario	Altura de Edificación	Media
Nivel Socioeconómico	Estrato Medio	Velocidad de Cambio	Media
Tendencia del Desarrollo Urbano	Consolidado Homogeneo	Estado de Conservación	Regular

Equipamiento del Entorno

	Nivel de Equipamiento		Nivel de Equipamiento
Comercial	Suficiente	Estacionamiento	Suficiente
Escolar	Suficiente	Áreas Verdes	Suficiente
Asistencial	Suficiente	Zonas Recreativas	Suficiente

Infraestructura de Servicio Urbano

	Dispone	Calidad	Estado de Conservación
Vías Asfaltadas	Completas	Medio	Bueno
Veredas	Completas	Medio	Bueno
Alcantarillado	Completas	Medio	Bueno
Agua Potable	Completas	Medio	Bueno
Alumbrado	Completas	Medio	Bueno

Vías Principales del Entorno: Av. Las Palmeras

4. CARACTERISTICAS DEL INMUEBLE

Terreno

Forma				**Topografía**				**Posición**			
Regular	X	Irregular		Plana	X	Pendiente		Interior		Exterior	X

Construcciones

Material Predominante	**Edad Efectiva (años)**	**Estado de Conservación**
Ladrillo	0	En Construcción

Descripción General

N° de Pisos/ Sótanos del edificio	**Áreas Comunes**	**N° Unidades en el conjunto**
3 / 0	No	1
Nivel ocupado en el edificio.	**Ascensor**	**Conexión de Servicios**
Todos	No	Sí, todos
Obras Complementarias	**Mantenimiento**	**Vista**
No	No cuenta con mantenimiento	Exterior

Descripción y Distribución Detallada del Inmueble

Sobre un terreno de forma regular y topografía plana, ubicado en la Urb. Las Palmeras - I Etapa, se construirá una vivienda unifamiliar de 03 pisos más azotea. El inmueble se ubica en un entorno homogéneo de uso residencial con zonificación Residencial de Densidad Alta (RDM), en un estrato socioeconómico medio, la urbanización cuenta con servicios básicos como redes de energía eléctrica, redes de agua y desagüe, telefonía fija e internet. La urbanización se encuentra cerca de colegios, locales comerciales, parques, entre otros.

La distribución de la vivienda según memoria descriptiva será la siguiente:

Primer piso: Ingreso, hall, garaje, escalera, SS.HH. (hommbres y mujeres), depósito, terraza, kitchen, patio, terraza, jardín, parrilla+barra.

Segundo piso: escalera hacia hall, recibo, SS.HH., sala, comedor, cocina, estudio, balcón.

Tercer Piso: escalera hacia pasadizo, dormitorio 1 con clóset emp., baño común, dormitorio 2 con clóset emp., dormitorio principal con W.C., baño propio y balcón.

Layseca Asociados

N° de Solicitud Banco	**1364852**
N° de Servicio Tasadora	**60347-2026**
Fecha de Expedición	30-Abr-2026
Fecha de Caducidad	30-Abr-2027

MEMORIA DESCRIPTIVA

Unidad Inmobiliaria	Linderos	Medida (Metros)
Por el Frente:	Colinda con Alameda Los Claveles.	8.00
Por la Derecha:	Colinda con Calle Los Cedros.	24.00
Por la Izquierda:	Colinda con Lote 20.	24.00
Por el Fondo:	Colinda con Lote 18.	8.00
		64.00

TERRENO

Unidad Inmobiliaria	Unidad Métrica	A.M. Prop. Horiz/ Vert.	% Participación	Área Privativa	Obtención del Área	Observación
Terreno	m2	192.00	100%	192.00	F. Reg/Part. Elect	
Total área de terreno				**192.00**		

Nota

CONSTRUCCION

Descripción	Unidad Métrica	Área Techada	Área sin Techar	Área Ocupada	Obtención del Área	Edificación Declarada
Primer Piso	m2	79.50		79.50	Solicitud Construyo	No
Segundo Piso	m2	79.50		79.50	Solicitud Construyo	No
Tercer Piso	m2	76.00		76.00	Solicitud Construyo	No
Total áreas construidas		**235.00**	**0.00**	**235.00**		

Nota

CARACTERISTICAS PRINCIPALES DE LA CONSTRUCCION

Calidad de la construcción

Muy Buena	X
Buena	
Regular	
Mala	

Tipo de construcción

Definitiva	X
Parcial	
Provisional	
Autoconstrucción	

Estructura general

Cimentación	Zapatas con Cimientos Corridos de Concreto Ciclópeo
Estructura	Sistema Mixto, Placas y Pórticos de C°A°
Muros	Albañilería (Ladrillo)
Techos	Losa Aligerada de C°A° Unidireccional
Cobertura	Sin Cobertura
Inst. Eléctricas	Corriente Monofásica empotrada
Inst. Gas	Sin Instalación
Inst. Sanitarias	Tuberías de agua fría, caliente y desagüe

ACABADOS

Puertas	Tipo	Maciza	Contraplacada	
	Material	Madera	Madera	
	Sistema	Batiente	Batiente	
Ventanas	Marco	No indica		
	Vidrio	No indica		
	Sistema	Corrediza		
Mamparas	Marco	Aluminio		
	Vidrio	Templado		
	Sistema	Corrediza		
Muebles de cocina	Tipo	No indica		
	Material	No indica		
	Tableros	No indica		
	Lavaderos	No indica		
Baños	Tipo	One Piece		
	Color	Blanco		
	Grifería	Nacional		
Closets		No indica		
Pisos		Porcelanato		
Revestimientos		Tarrajeo y Pintura		
Cerrajería		Cerradura tipo Yale o Similar		

Obras Complementarias e Instalaciones Fijas

Aire Acondicionado		Cerco	X
Alarma		Cisterna	X
Ascensor		Iluminación Especial	
Intercomunicador		Piscina	
Sistema Hidroneumático		Tanque Elevado	

Otros y Comentarios

Layseca Asociados

N° de Solicitud Banco	**1364852**
N° de Servicio Tasadora	**60347-2026**
Fecha de Expedición	30-Abr-2026
Fecha de Caducidad	30-Abr-2027

ANALISIS METODOLOGICO

METODO DE COSTOS O REPOSICION (OFERTA DE MERCADO PARA TERRENOS)


A. DATOS GENERALES DE REFERENCIAS DE MERCADO

	Ubicación / Descripción	Fuente Página Web	Teléfono	Nombre Contacto	Forma / Topografía	Zonif.	Distancia al bien (m)	Fecha
1	Terreno ubicado en la Urb. Las Palmeras de Centenario, Distrito de Castilla.	https://gethouse.pe/inmuebles/se-vende-terreno-en-esquina-y-frente-a-parque-urb-centenario-etapa-1/19-153-1529-3-0-2	965038266	Roberto Chung Antón	Regular / Plana	RDM	82	30-Abr-26
2	Terreno ubicado en la Urb. Las Palmeras de Centenario, Distrito de Castilla.	https://www.remax.pe/v1/user/caulestia@remax-newhome.com/propiedad-terreno-en-venta-castilla-piura-piura-1179679/	956063529	Cecilia Aulestia	Regular / Plana	RDM	102	30-Abr-26
3	Terreno ubicado en la Urb. Las Palmeras de Centenario, Distrito de Castilla.	https://www.remax.pe/v1/user/caulestia@remax-newhome.com/propiedad-terreno-en-venta-castilla-piura-piura-1170770/	956063529	Cecilia Aulestia	Regular / Plana	RDM	386	30-Abr-26
4	Terreno ubicado en la Urb. Las Palmeras de Centenario, Distrito de Castilla.	https://www.remax.pe/v1/user/mtorres@remax-newhome.com/propiedad-terreno-en-venta-castilla-piura-piura-1160285/	961593911	Mery Berzabet Torres Labán	Regular / Plana	RDM	91	30-Abr-26
5	Terreno ubicado en la Urb. Las Palmeras de Centenario, Distrito de Castilla.	https://www.adondevivir.com/propiedades/clasificado/vecltein-ocasion-lote-en-venta-119.93-m-sup2--calle-las-	942985899	INMOBILIARIA RE/MAX PLATINUM	Regular / Plana	RDM	438	30-Abr-26

B. HOMOLOGACIÓN DE REFERENCIAS DE MERCADO DE TERRENOS

	Valor del Inmueble Referencial (US$)	Área (m2)	Valor Unitario Terreno (US$/m2)	Factores de HOMOLOGACIÓN						Factor Resultante	Valor Unit. Terreno Homologado (US$/m2)
				Ub.	Ent.	Sup.	Ser.	Zon.	F.N.		
1	39,000.00	192.00	203.13	1.00	1.00	1.00	1.00	1.00	0.95	0.95	192.97
2	26,162.00	105.00	249.16	1.00	1.00	0.96	1.00	1.00	0.95	0.91	226.74
3	26,162.00	130.10	201.09	1.05	1.00	0.97	1.00	1.00	0.95	0.97	195.06
4	22,093.00	108.75	203.15	1.05	1.00	0.96	1.00	1.00	0.95	0.96	195.03
5	24,855.00	119.93	207.25	1.05	1.00	0.97	1.00	1.00	0.95	0.97	201.03
	Valor Unitario Terreno Homologado Promedio [$/m²]		**202.17**	VUT Prom. Homologado ajustado[$/m²]							**200.00**

PLANO DE UBICACIÓN Y REFERENCIAS DE TERRENO

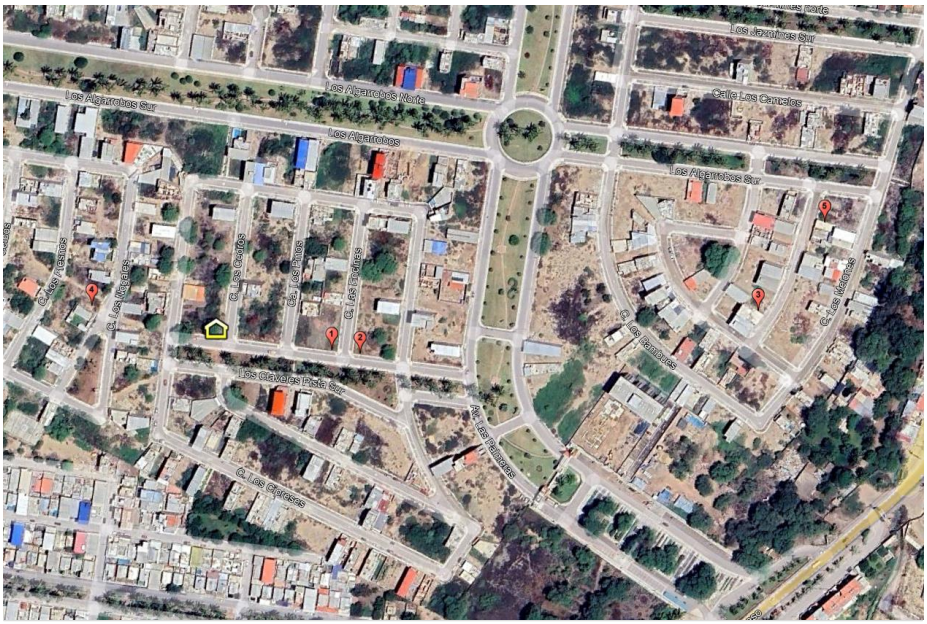
Los Algarrobos Sur
Los Algarrobos Norte
Los Algarrobos
Calle Los Cansios
Las Algarrobas Sur
Los Jazmines Sur
Los Claveles Poste Sur
Av. Las Primaveras
Jr. Los Rosales
Jr. Los Tulipanes
Jr. Los Rosales
Jr. Los Claveles
Jr. Los Claveles
Jr. Los Claveles

Layseca Asociados

N° de Solicitud Banco	**1364852**
N° de Servicio Tasadora	**60347-2026**
Fecha de Expedición	30-Abr-2026
Fecha de Caducidad	30-Abr-2027

ANALISIS METODOLOGICO

METODO DIRECTO DE COSTOS O REPOSICION

A. VALOR DE TERRENO (VT)

De acuerdo a la Investigación de Mercado de Terrenos con características similares al inmueble tasado se obtiene;

Unidad Inmobiliaria	Área de terreno (m2)	% de Participación	V.U. de Terreno (US$/m2)	Valor de Terreno (US$/m2)
Terreno	192.00	100.0%	200.00	38,400.00
Subtotal Terreno (VT)	**192.00**			**38,400.00**

B. VALOR DE LAS EDIFICACIONES (VSNE Y VE)

De acuerdo a las características constructivas y a los acabados del inmueble observados en la inspección realizada se estima;

Región de la Edificación
Costa

Código	Partida	VUE1		VUE2		VUE3		VUE4		VUE5		VUE6	
		Clas.	Costo/m2	Clas.	Costo/m2	Clas.	Costo/m2	Clas.	Costo/m2	Clas.	Costo/m2	Clas.	Costo/m2
1	Muros y Columnas												
2	Techos												
3	Pisos												
4	Puertas y Ventanas												
5	Revestimientos												
6	Baños												
7	Instalaciones Eléctricas y Sanitarias												
	Costo Unitario de Edificación (S/)		**0.00**		**0.00**		**0.00**		**0.00**		**0.00**		**0.00**

Gastos Generales **14%** (Obra Pequeña)

Utilidad **10%** Tipo de Cambio **S/. 3.486**

Valor Unitario de Edificación (S/)	**0.00**	**0.00**	**0.00**	**0.00**	**0.00**	**0.00**
Valor Unitario de Edificación redondeado (US$)	**0.00**	**0.00**	**0.00**	**0.00**	**0.00**	**0.00**

Cálculo del Valor Similar a Nuevo o Valor de Reconstrucción de las Edificaciones (VSNE) y el Valor de las Edificaciones (VE)

Descripción	Área (m2)	VUE (US$/m2)	Valor Similar a Nuevo (US$)	Material Predominante	Edad (años)	Estado de Conservación	FD (*)	Valor de Edificación (US$)
Primer Piso	79.50	561.47	44,636.62	Ladrillo	0	En Construcción	1.00	44,636.62
Segundo Piso	79.50	561.47	44,636.62	Ladrillo	0	En Construcción	1.00	44,636.62
Tercer Piso	76.00	561.47	42,671.49	Ladrillo	0	En Construcción	1.00	42,671.49
Subtotal Edificaciones (VSNE)	**235.00**	US$	**131,944.73**	Subtotal Edificaciones (VE)		US$		**131,944.73**

C. VALOR DE ÁREAS COMUNES (VAC)

Según el Reglamento General de Tasaciones del Perú, para el valor de las Áreas Comunes, se asigna un % del valor de la edificación;

Descripción	% de Áreas Comunes	Valor Unitario de Áreas Comunes (US$/m2)	Valor de Reconstrucción Áreas Comunes (US$)	FD (*)	Valor de Áreas Comunes (US$)
		0.00			
Subtotal Áreas Comunes (VAC)		US$	**0.00**	US$	**0.00**

D. VALOR DE LAS INSTALACIONES Y OBRAS COMPLEMENTARIAS (VI + VOC)

Descripción	Cantidad	Unidad (u)	Valor Unitario (US$/u)	Valor de Reconstrucción (US$)	FD (*)	Valor de Inst. y Obras Complem. (US$)
Subtotal Instalaciones y Obras Complementarias (VI + VOC)			US$	**0.00**	US$	**0.00**

(*) Factor de Depreciación

E. VALOR TOTAL DEL PREDIO (VTP1) [Mediante el Método de Costos Directos = VT + VE + VAC + VI + VOC]	US$	**170,344.73**
F. VALOR DE RECONSTRUCCIÓN DEL INMUEBLE TASADO (VSN) [= VSNE + VSNAC + VSNVI + VSNVOC]	US$	**131,944.73**

Layseca Asociados

N° de Solicitud Banco	**1364852**
N° de Servicio Tasadora	**60347-2026**
Fecha de Expedición	30-Abr-2026
Fecha de Caducidad	30-Abr-2027

RESULTADOS

1. RESUMEN GENERAL DE TASACION

A. RESULTADOS DE LOS MÉTODOS DIRECTOS

	VTP (US$)	VU (US$/m2)	VTP (S/)
Método de Costos o Reposición	170,344.73	724.87	593,821.73
Método de Comparación o de Mercado	No considerado		

B. RESULTADO DEL MÉTODO INDIRECTO

Método de la Renta o Capitalización	No considerado		

2. VALOR COMERCIAL DEL INMUEBLE

A. VALOR COMERCIAL (VC)

Para determinar la conclusión del Valor Comercial del inmueble motivo de la presente tasación, se han tenido en cuenta las siguientes consideraciones

a.

b.

c.

d. El método que mejor refleja el Valor Comercial es por **Método Directo de Costos (O de Reposición)**

	Valor Comercial
Valor Comercial en Dólares (Moneda Extranjera)	
CIENTO SETENTA MIL CON 00/100 DÓLARES AMERICANOS	**US$ 170,000.00**
Valor Comercial en Soles (Moneda Local)	
QUINIENTOS NOVENTA Y DOS MIL SEISCIENTOS VEINTE CON 00/100 SOLES	**S/ 592,620.00**

VALOR DE REALIZACION

A. VALOR DE REALIZACIÓN INMEDIATA (VRI)

El Valor de Realización Inmediata, es el Valor Neto del inmueble que se esperaría recuperar como consecuencia de la eventual venta del bien en el menor tiempo posible y en las condiciones actuales del inmueble y el mercado. Se obtiene descontando los castigos y cargos por los conceptos indicados a continuación;

	Concepto de la Deducción	% de la Deducción	Importe (US$)
A	Gastos de Publicidad.	2.00%	3,400.00
B	Gastos de tasación del inmueble para la Realización.	0.20%	340.00
C	Comisiones de Ventas.	5.00%	8,500.00
D	Mantenimiento.	2.00%	3,400.00
E	Factor por la venta del inmueble (Realización) en un plazo de 60 días.	10.80%	18,360.00
F	Otras Deducciones (Sólo casos especiales)	0.00%	0.00
	Total Deducciones	**20.00%**	**US$ 34,000.00**

	Valor Realización Inmediata
En Dólares (Moneda Extranjera)	
CIENTO TREINTA Y SEIS MIL CON 00/100 DÓLARES AMERICANOS	**US$ 136,000.00**
En Soles (Moneda Local)	
CUATROCIENTOS SETENTA Y CUATRO MIL NOVENTA Y SEIS CON 00/100 SOLES	**S/ 474,096.00**

RESPONSABLE

EMPRESA TASADORA	**LAYSECA ASOCIADOS S.A.C.**
REGISTRO REPEV	**N° 2741-2013**
PERITO RESPONSABLE DE INSPECCION OCULAR	**Arq. José Luis Castro Pacherres**

LAYSECA ASOCIADOS SAC
REPEV Nº 2741-2013

PERITO	Ing. Manuel Barboza Oviedo	PERITO	Arq. Josselyn Sánchez Diaz
PROFESION	Ingeniero Civil	PROFESION	Arquitecta
REPEV	N° 02668-2022	REPEV	N° 3041-2024
CIP	N° 258213	CAP	N° 29128

OBSERVACIONES DEL PERITO

- Se sustenta la ubicación del inmueble con Visor Base Gráfica de Sunarp, ver anexos.
- Para el presente informe se ha contado con el presupuesto por partida y solicitud de construyo aprobado por el banco, en soles, por lo que se utilizó el Tipo de Cambio del mes proporcionado por el banco.
- El Valor Unitario de Edificación se ha obtenido de dividir el Valor Total en soles del presupuesto alcanzado, además, se ha considerado que este presupuesto ya está aprobado por el banco.
- El área techada de la Edificación, así como las características de los acabados se han obtenido de la memoria descriptiva proporcionada.
- El tiempo de ejecución de obra es de 140 días, apartir del inicio de obra (no indicado).

CONDICIONANTES Y ADVERTENCIAS

a. Las áreas de terreno, áreas construidas, áreas libres, áreas ocupadas y perímetro del predio fueron obtenidas de la documentación registral, documentación municipal y planos, proporcionados por el propietario. Layseca Asociados S.A.C. no ha realizado mediciones en el predio ni revisada documentación distinta a la proporcionada por el propietario.

b. Layseca Asociados S.A.C. no asume responsabilidad sobre la veracidad, confiabilidad, exactitud, fidelidad, plenitud y precisión de la información proporcionada por el propietario, ni sobre las conclusiones erradas que eventualmente podrían haberse derivado de ella. La existencia de documentos adicionales no proporcionados, que puedan contener información diferente de la proporcionada, puede invalidar las conclusiones del presente informe sin responsabilidad alguna de Layseca Asociados S.A.C.

c. Este informe ha sido elaborado sobre la base de lo apreciado visiblemente durante la inspección ocular del predio. Layseca Asociados S.A.C. no asume responsabilidad por vicios ocultos en el predio ni por la calidad posesoria de las personas que se encuentren dentro del predio.

d. La interpretación de los documentos y sus condiciones, específicamente aplicada a la pericia, no constituye asesoría legal ni comercial especializada en la materia.

e. Las conclusiones del informe son válidas en su fecha de emisión y durante el periodo de vigencia establecido, siempre que no varíen significativamente las condiciones del mercado y de los bienes, en cuyo caso deberá requerirse una actualización de la valuación.

Layseca Asociados

N° de Solicitud Banco	**1364852**
N° de Servicio Tasadora	**60347-2026**
Fecha de Expedición	30-Abr-2026
Fecha de Caducidad	30-Abr-2027

DOCUMENTACION GRAFICA



ENTORNO: ALAMEDA LOS CLAVELES



ENTORNO: CALLE LOS CEDROS



ENTORNO: LETRERO DE CALLES



VISTA ESQUINA DEL INMUEBLE



FACHADA FRONTAL DEL INMUEBLE



FACHADA LATERAL DEL INMUEBLE



INTERIOR DEL INMUEBLE



INTERIOR DEL INMUEBLE

PUBLICIDAD : 2391684 Recibo Nº 2026-1060-1488 Partida Nº 11163129 CERTI. LITERAL - PREDIOS

sunarp
Superintendencia Nacional de los Registros Públicos

ZONA REGISTRAL Nº I - SEDE PIURA
OFICINA REGISTRAL PIURA
Nº Partida: 11163129

INSCRIPCION DE REGISTRO DE PREDIOS
MZ A11 LOTE 19 URB LAS PALMERAS I ETAPA
CASTILLA

REGISTRO DE LA PROPIEDAD INMUEBLE
RUBRO: PARTIDA DE INDEPENDIZACIÓN POR RECEPCIÓN DE OBRAS
G00001

RUBRO: ANTECEDENTE DOMINIAL
A00001: Independizada de la partida Nº 11153025.

RUBRO: DESCRIPCIÓN DEL INMUEBLE
B00001:
Lote Nº 19 de la manzana A11 de la Urbanización Las Palmeras I Etapa, ubicado en el distrito de Castilla, provincia y departamento de Piura.
Cuenta con las siguientes características:
Área: 192.00 m²
Linderos y medidas perimétricas:

Por el frente	colinda con Alameda Los Claveles, con 08.00 ml.
Por la derecha	colinda con Calle Los Cedros, con 24.00 ml.
Por la izquierda	colinda con Lote 20, con 24.00 ml.
Por el fondo	colinda con Lote 18, con 08.00 ml.

RUBRO: TÍTULOS DE DOMINIO
C00001:
Se independiza a favor de **INVERSIONES CENTENARIO S.A.A.** inscrita en la partida N° 02003856 del Registro de Personas Jurídicas de Lima, de conformidad con lo dispuesto en los artículos 40 y 41 del Reglamento de Inscripciones del Registro de Predios; y, en mérito al Formulario Único de Habilitación Urbana – FUHU (Recepción de Obras), con expediente N° 06065 de fecha 23/02/2016, debidamente visado por la Gerencia de Desarrollo Urbano Rural y la Sub Gerencia de Catastro y Control Urbano de la Municipalidad Distrital de Castilla; a la Resolución Gerencial de Recepción de Obras de Habilitación Urbana Nº 1187-2015-GDUR-MDC de fecha 28/12/2015, Resolución Gerencial de Recepción de Obras de Habilitación Urbana Nº 002-2016-SGCyCU-MDC de fecha 02/03/2016 y Resolución Gerencial de Recepción de Obras de Habilitación Urbana Nº 0325-2016-SGCyCU-MDC de fecha 06/04/2016, expedidas por la Gerencia de Desarrollo Urbano Rural y la Sub Gerencia de Catastro y Control Urbano de la Municipalidad Distrital de Castilla; a la memoria descriptiva y planos, visados por la Gerencia de Desarrollo Urbano Rural y la Sub Gerencia de Catastro y Control Urbano de la Municipalidad Distrital de Castilla que acompañan la referida resolución; y, a los informes técnicos Nº 1249-2016-ORP-SCR-ZRN°I-UREG/SUNARP de fecha 17/03/2016 y Nº 0187-2016-ORP-SCR-ZRN°I-UREG/SUNARP de fecha 13/01/2016, emitidos por el Ing. Federico Trelles García, coordinador responsable del área de catastro.

RUBRO: CARGAS Y GRAVÁMENES
D00001: ***Traslado del asiento D00001 de la partida Nº 11153025 (trasladado del asiento D00008 de la partida Nº 11093836)***
HIPOTECA.- El propietario del inmueble, *el deudor*, constituye **HIPOTECA** a favor del **BANCO CONTINENTAL**, hasta por la suma de **US$. 7'500,000.00 dólares americanos** o su equivalente en nuevos soles, con el objeto de garantizar el pago de la operación puntual de mediano plano como préstamo comercial por la suma de US$. 7'500,000.00 dólares americanos; asumida por el deudor frente al Banco en virtud del contrato de préstamo suscrito entre ambos con fecha 14 de marzo de 2011 (en adelante el contrato de crédito), igualmente garantiza toda deuda u obligación de el deudor a favor del Banco por intereses compensatorios y moratorios y las penalidades, comisiones, gastos, seguros e impuestos que fueran procedentes con relación a la operación puntual de mediano plazo referida en el numeral precedente, de conformidad con el artículo 1107° del Código Civil, asimismo garantiza en las mismas condiciones cualquier renovación, reestructuración o refinanciación de las obligaciones garantizadas en el numeral 2.1 de la presente cláusula; y demás deudas y obligaciones que se detallan en el contrato presentado. El inmueble se

Abog. Víctor Angel Miranda Rivera
REGISTRADOR PUBLICO CERTIFICADOR
Zona Registral Nº I - Sede Piura

Certificado Literal
No hay títulos pendientes de Inscripción
Ni Suspensión al Dorso
Ni Tachas ni Observaciones Pendientes

PUBLICIDAD : 2391684 Recibo Nº 2026-1060-1488 Partida Nº 11163129 CERTI. LITERAL - PREDIOS

sunarp
Superintendencia Nacional de los Registros Públicos

ZONA REGISTRAL Nº I - SEDE PIURA
OFICINA REGISTRAL PIURA
Nº Partida: 11163129

INSCRIPCION DE REGISTRO DE PREDIOS
MZ A11 LOTE 19 URB LAS PALMERAS I ETAPA
CASTILLA

REGISTRO DE PROPIEDAD INMUEBLE
RUBRO: TITULOS DE DOMINIO
C00002

COMPRAVENTA:

HUGO FERNANDO ESPINOZA RAMOS, soltero, identificado con DNI Nº 41843274 y **HEIDY MELISSA SAAVEDRA FEIJOO**, soltera, identificada con DNI Nº 43040266, han adquirido la propiedad del predio inscrito en la presente partida, en mérito a la compraventa celebrada con su anterior propietaria, Inversiones Centenario SAA, por el precio de S/ 77,952.00 soles, totalmente cancelados. Así consta en la Escritura Pública N° 128 JFS otorgada con fecha 17 de enero del 2018 ante el Notario Público de Piura, abogado Juan Manuel Quinde Rázuri.

El título fue presentado el 02/03/2018 a las 03:13:43 PM horas, bajo el N° 2018-00500832 del Tomo Diario 0237. Derechos cobrados S/ 268.00 soles con Recibo(s) Número(s) 00009096-50 00010027-50.-PIURA, 08 de marzo de 2018.

ANA KARINA KAMAHARA ATARAMA
REGISTRADOR PUBLICO
ZONA REGISTRAL Nº I - SEDE PIURA

Abog. Víctor Angel Miñan Rivera
ABOGADO CERTIFICADOR
Zona Registral Nº I - Sede Piura

Certificado Literal
Sin Inscripción Posterior
No hay Títulos Suspendidos y/o Pendientes
A Horas : 8:00 AM

MEMORIA DESCRIPTIVA: ARQUITECTURA

I. DATOS GENERALES:

1.-OBRA	:	CONSTRUCCION DE VIVIENDA UNIFAMILIAR
2.-PROPIETARIO	:	SR. HUGO FERNANDO ESPINOZA RAMOS
		SRA. HEIDY MELISSA SAAVEDRA FEIJOÓ
3.-FECHA	:	JUNIO DE 2025.
4.-OBJETIVO	:	LICENCIA PARA EJECUCION DE OBRA
5.-UBICACIÓN	:	El terreno se encuentra ubicado en:
*AVENIDA	:	"LOS CLAVELES"
*CALLE	:	"LOS CEDROS"
*MANZANA	:	"A-11"
*LOTE	:	19
*URBANIZACIÓN	:	LAS PALMERAS
*ETAPA	:	1º ETAPA
*DISTRITO	:	CASTILLA
*PROVINCIA	:	PIURA
*REGIÓN	:	PIURA

II. LINDEROS Y MEDIDAS PERIMETRICAS:

-Por el Frente	:	Colinda con Alameda Los Claveles, con 8.00ml.
-Por la Derecha	:	Colinda con Calle Los Cedros, con 24.00ml.
-Por la Izquierda	:	Colinda con el Lote 20, con 24.00ml.
-Por el Fondo	:	Colinda con Lote 18, con 8.00ml.

-Encierra un área total de **192.00 metros cuadrados.**

-Delimitado por un Perímetro total de **64.00 metros lineales.**

III. DESCRIPCIÓN DEL PROYECTO:

El proyecto trata de una edificación nueva, para uso Residencial, de vivienda Unifamiliar, la cual se plantea de acuerdo al siguiente detalle:

-En el 1° nivel se ha proyectado el área recreativa de la vivienda

-En el 2° nivel se ha planteado el área social de la vivienda.

-En el 3° nivel se ha planteado el área íntima de la vivienda.

-En el 4° nivel o Azotea se ha planteado el área de servicio de la vivienda.

ARQ. VICENTE PATIÑO CUEVA
REG. CAP. N° 10529

El diseño se ha planteado de acuerdo a los parámetros urbanísticos de dicha zona regulada en el PDU de la Municipalidad Distrital de Castilla (Ver plano de ubicación U-01); los 03 niveles y la azotea, están destinados al uso Residencial de vivienda y la distribución de ambientes por piso es la siguiente:

Cuarto piso – Azotea Proyectado. -

El Cuarto piso – azotea se ha proyectado para el uso residencial en tipología de vivienda unifamiliar y consta de los siguientes espacios:

-Pasillo
-Dormitorio de servicio
-Lavandería
-Servicio Higiénico
-Terraza + azotea

Todos estos espacios conforman un área techada en el primer nivel de 35.24 m2.

IV. RESUMEN DE ÁREAS:

-El área proyectada techada del primer nivel, es de	:	79.50m2
-El área proyectada techada del segundo nivel, es de	:	79.50m2
-El área proyectada techada del tercer nivel, es de	:	76.00m2
-El área proyectada techada de la azotea, es de	:	35.24m2
-EL área proyectada techada total, es de	:	270.24m2
-EL área del lote, es de	:	192.00m2
-El área libre, es de	:	112.50m2
-El área a construir con licencia de obra, es de	:	270.24m2

V. CARACTERISTICAS DE LA EDIFICACION:

La presente edificación para uso de vivienda unifamiliar, se ha proyectado en 3 niveles y azotea mediante una escalera integrada, y acceso al techo mediante una escalera de gato para mantenimiento de tanques elevados y se ha considerado su construcción con las siguientes características:

ARQ. VICENTE PATIÑO CUEVA
REG. CAP. N° 10529

1. ESTRUCTURAS Y ARQUITECTURA:

A) ESTRUCTURAS CIMIENTOS:

La edificación del proyecto vivienda unifamiliar y de uso colectivo, está basada en una estructura mixta de: Cimentación con Zapatas conectadas con vigas de Cimentación con concreto armado de resistencia f'c=210 Kg. /cm2, Cimientos corridos de concreto ciclópeo (cemento – hormigón 1:10+30% de piedra grande), sobrecimientos armados de resistencia f'c=210 Kg. /cm2; todos los elementos que se construyan directamente sobre el terreno irán asentadas sobre un solado de cemento hormigón 1:12 y las sobre excavaciones se llenarán con concreto 1:10 de acuerdo al RNE.

B) COLUMNAS Y PLACAS, Y ESCALERAS:

Las columnas, placas estructurales y escaleras serán de sección variada como se indica en los planos, con una altura especificada en los planos; su material es de concreto armado f'c= 210 Kg/cm^2 y el acero con f'y=4,200 Kg/cm^2 de especificación. Estas columnas nacen desde el primer piso y están amarradas por vigas peraltadas y chatas formando un sistema de pórticos de concreto armado de f'c=210 kg/cm2 y

H) PINTURA:

Pintura lavable en muros interiores de todos los ambientes; pintura anticorrosiva y esmalte en la carpintería metálica y con pintura barniz en puertas de madera maciza y contra placadas.

I) BAÑOS:

Los servicios higiénicos se acondicionarán con aparatos sanitarios blancos; piso de porcelanato o cerámico nacional de color de 40x40 y zócalos de porcelanato o cerámico nacional de 20x30, con grifería nacional y sus respectivos accesorios sanitarios (jabonera, toallero, ganchos y otros).

VI. RELACION DE PLANOS

- A-1: PLANTAS DE DISTRIBUCIÓN: 1°, 2° Y 3° PISO
- A-2: PLANTA DE AZOTEA Y TECHOS
- A-3: CORTES
- A-4: ELEVACIONES

ARQ. VICENTE PATIÑO CUEVA
REG. CAP. N° 10529

Piura, 10 de enero del 2025.

Cotización KCC -004-2026- HCHA

Cliente: Sr. Hugo Espinoza Ramos.

Asunto: Cotización para la Construcción de Vivienda Unifamiliar en Urb. Las Palmeras – Castil Piura.

Referencia:

De nuestra consideración:

En atención a su amable invitación tenemos a bien alcanzarle la Cotización por Las Siguientes Partid

1. Costo:

Item	Descripción	Unid	Cant	Preci	Parcial	Sub Total
1	CONSTRUCCIÓN DEL CASCO GRIS DE VIVIENDA EN URB. LAS PALMERAS.					
1.1	CONTRUCCIÓN PROVISIONAL Y					S/ 2,409.26
1.1.1						S/ 2,409.26
1.1.1.1	MOVILIZACIÓN DE EQUIPOS Y	glb	1	S/ 800.00	S/ 800.00	
1.1.1.2	ALMACÉN Y/O CASETA DE GUARDIANÍA	gbl	1	S/ 450.00	S/ 450.00	
1.1.1.3	TRAZO NIVELACION Y REPLANTEO	m²	417	S/ 2.78	S/ 1,159.26	
OE.2	1° NIVEL					S/ 199,637.57
OE.2.1	MOVIMIENTO DE TIERRAS					S/ 14,095.73
OE.2.1.1	EXCAVACIÓN MANUAL PARA ZAPATA	m³	13.09	S/ 35.10	S/ 459.46	
OE.2.1.2	EXCAVACIÓN MANUAL PARA CIMIENTOS	m³	70.24	S/ 35.10	S/ 2,465.42	
OE.2.1.3	EXCAVACIÓN MANUAL PARA VIGA	m³	10.27	S/ 35.10	S/ 360.48	
OE.2.1.4	EXCAVACION MANUAL PARA CISTERNA	m³	12.5	S/ 35.10	S/ 438.75	
OE.2.1.5	RELLENO Y COMPACTADO CON AFIRMADO 1 CAPA DE E=0.20 m	m²	233.09	S/ 28.00	S/ 6,526.52	
OE.2.1.6	ELIMINACIÓN DE MATERIAL PRODUCTO DE LA EXCAVACIÓN	m³	109.86	S/ 35.00	S/ 3,845.10	
OE.2.2	OBRAS DE CONCRETO SIMPLE					S/ 18,590.74
OE.2.2.1	CIMIENTO CORRIDO					S/ 18,590.74
OE.2.2.1.1	SOLADO MEZCLA C:H 1:15	m³	4.15	S/ 260.00	S/ 1,079.00	
OE.2.2.1.2	CIMIENTOS CORRIDOS MEZCLA 1:10 C:H +	m³	46	S/ 380.69	S/	
OE.2.3	OBRAS DE CONCRETO ARMADO					S/ 98,566.48
OE.2.3.1	ZAPATAS					S/ 12,164.89
OE.2.3.1.1	SOLADO MEZCLA C:H 1:17	m³	2.21	S/ 260.00	S/ 574.60	
OE.2.3.1.2	ACERO DE REFUERZO F'Y=4200 Kg/cm2	kg	521	S/ 7.00	S/ 3,647.00	
OE.2.3.1.3	CONCRETO EN ZAPATAS, F'C=210 Kg/cm2	m³	13.09	S/ 600.00	S/ 7,854.00	
OE.2.3.1.4	CURADO CON ADITIVO QUIMICO	m²	25.51	S/ 3.50	S/ 89.29	
OE.2.3.2	VIGA DE CIMENTACIÓN (V-01)					S/ 4,890.97
OE.2.3.2.1	SOLADO MEZCLA C:H 1:17	m³	0.68	S/ 260.00	S/ 176.80	
OE.2.3.2.2	ACERO DE REFUERZO F'Y=4200 Kg/cm2	kg	412	S/ 7.00	S/ 2,884.00	
OE.2.3.2.3	CONCRETO , F'C=210 Kg/cm2	m³	3	S/ 600.00	S/ 1,800.00	
OE.2.3.2.4	CURADO CON ADITIVO QUIMICO	m²	8.62	S/ 3.50	S/ 30.17	

OE.2.3.3	COLUMNAS (ACERO + ENCOFRADO Y DESENCONFRADO+ VACEADO)				
OE.2.3.3.1	COLUMNA TIPO C-1 (0.40x 0.20 m) - INCLUYE EL ENCOFRADO + ACERO + VACEADO + CURADO	und	5	S/ 820.00	S/ 4,100.00
OE.2.3.3.2	COLUMNA TIPO C-2 (0.40+0.40x 0.15 m) - INCLUYE EL ENCOFRADO + ACERO + VACEADO + CURADO	und	3	S/ 1,100.00	S/ 3,300.00
OE.2.3.3.3	COLUMNA TIPO C-3 (0.50x 0.15 m) - INCLUYE EL ENCOFRADO + ACERO + VACEADO + CURADO	und	5	S/ 640.00	S/ 3,200.00
OE.2.3.3.4	COLUMNA TIPO C-4 (0.30x 0.15 m) - INCLUYE EL ENCOFRADO + ACERO + VACEADO + CURADO	und	6	S/ 420.00	S/ 2,520.00
OE.2.3.3.5	COLUMNA TIPO C-5 (0.30x 0.15 m) - INCLUYE EL ENCOFRADO + ACERO + VACEADO + CURADO	und	11	S/ 355.00	S/ 3,905.00
OE.2.3.3.6	COLUMNA TIPO C-6 (0.25x 0.15 m) - INCLUYE EL ENCOFRADO + ACERO + VACEADO + CURADO	und	5	S/ 325.00	S/ 1,625.00
OE.2.3.3.7	PLACA 1 (1.00 + 0.15 + 0.15x 0.15 m) - INCLUYE EL ENCOFRADO + ACERO + VACEADO + CURADO	und	1	S/ 1,380.00	S/ 1,380.00
OE.2.3.3.8	PLACA 2 (0.50x 0.15 m) - INCLUYE EL ENCOFRADO + ACERO + VACEADO + CURADO	und	3	S/ 650.00	S/ 1,950.00
OE.2.3.3.9	PLACA 3 (0.75 x 0.15 m) - INCLUYE EL ENCOFRADO + ACERO + VACEADO + CURADO	und	2	S/ 950.00	S/ 1,900.00
OE.2.3.4	SOBRECIMIENTO h=(v ariable segun Plano E-01)				
OE.2.3.4.	ENCOFRADO Y DESENCOFRADO DE	m²	132	S/ 46.05	S/ 6,078.60
OE.2.3.4.	ACERO DE REFUERZO F'Y=4200 Kg/cm2	kg	689	S/ 7.00	S/ 4,823.00
OE.2.3.4.	CONCRETO PARA SOBRECIMIENTO, F'C=175 Kg/cm2	m³	8.95	S/ 480.00	S/ 4,296.00
OE.2.3.4.4	CURADO CON ADITIVO QUIMICO	m²	132	S/ 3.80	S/ 5
OE.2.3.5	CISTERNA DE 2000 LTS.				
OE.2.3.5.	ENCOFRADO Y DESENCOFRADO	m²	38	S/ 70.00	S/ 2,660.00
OE.2.3.5.	CONCRETO , F'C=210 Kg/cm2	m³	6.79	S/ 600.00	S/ 4,074.00
OE.2.3.5.	ACERO DE REFUERZO F'Y=4200 Kg/cm2	kg	380	S/ 7.00	S/ 2,660.00
OE.2.3.5.4	CURADO DE MUROS CON ADITIVO QUIMICO	m²	38	S/ 3.80	S
OE.2.3.5.5	IMPERMIABILIZANTE LIQUIDO	blt	45	S/ 6.95	S/ 31
OE.2.3.6	LOSA ALIGERADA				
OE.2.3.6.	ENCOFRADO Y DESENCOFRADO EN LOSA	m²	82	S/ 46.05	S/ 3,776.10
OE.2.3.6.2	ACERO DE REFUERZO F'Y=4200 Kg/cm2	kg	1843	S/ 7.00	S/ 1
OE.2.3.6.	CONCRETO, F'C=210 Kg/cm2	m³	12.81	S/ 600.00	S/ 7,686.00
OE.2.3.6.4	CURADO DE LOSA ALIGERADA CON ADITIVO QUIMICO	m²	154.58	S/ 3.80	
OE.2.3.6.	LADRILLO DE TECHO N° 15	m²	670	S/ 3.85	S/ 2,579.50
OE.2.3.7	ESCALERA				
OE.2.3.7.1	ENCOFRADO Y DESENCOFRADO EN ESCALERA	m²	12.66	S/ 46.05	
OE.2.3.7.	ACERO DE REFUERZO F'Y=4200Kg/cm2	kg	183	S/ 7.00	S/ 1,281.00
OE.2.3.7.3	CONCRETO, F'C=210 Kg/cm2	m³	1.56	S/ 600.00	S/ 93
OE.2.3.7.	CURADO DE ESCALERA CON ADITIVO QUIMICO	m²	12.66	S/ 3.80	S/
OE.2.3.8	ALEROS DE FACHADA				
OE.2.3.8.1	ENCOFRADO Y DESENCOFRADO EN ESCALERA	m²	8.48	S/ 46.05	
OE.2.3.8.2	ACERO DE REFUERZO F'Y=4200Kg/cm2	kg	85	S/ 6.37	S/ 5
OE.2.3.8.3	CONCRETO, F'C=210 Kg/cm2	m³	1.23	S/ 600.00	S/ 73
OE.2.3.8.	CURADO DE ESCALERA CON ADITIVO QUIMICO	m²	8.48	S/ 3.80	S/

Layseca Asociados

N° de Solicitud Banco	**1364852**
N° de Servicio Tasadora	**60347-2026**
Fecha de Expedición	30-Abr-2026
Fecha de Caducidad	30-Abr-2027

ANEXO IV

RESUMEN PRESUPUESTO GENERAL DE OBRA

OE.2.4	ARQUITECTURA				
OE.2.4.1	MUROS Y TABIQUES DE ALBAÑILERIA				
OE.2.4.1.	LADRILLO DE SOGA E=0.15	m²	172	S/ 80.00	S/
OE.2.4.2	REVOQUES ENLUCIDOS Y MOLDURAS				
OE.2.4.2.	TARRAJEO DE CIELO RASO	m²	82	S/ 37.60	S/
OE.2.4.2.	TARRAJEO DE MUROS INTERIORES	m²	284	S/ 37.60	S/
OE.2.4.2.	TARRAJEO DE MUROS EXTERIORES	m²	210.78	S/ 37.60	S/
OE.2.4.2.	TARRAJEO DE SOBRECIMIENTO	m²	42	S/ 16.21	S/ 680.82
OE.2.4.2.	TARRAJEO DE COLUMNAS	m²	24	S/ 37.60	S/ 902.40
OE.2.4.2.	TARRAJEO DE ESCALERA	m²	13.66	S/ 37.60	S/ 513.62
OE.2.4.2.	VESTIDURA DE DERRAMES	m	135	S/ 16.21	S/
OE.2.4.3	PISOS Y PAVIMENTOS				
OE.2.4.3.	FALSO PISO DE F'C=175 kg/cm2 E=0.10 m	m²	142	S/ 38.57	S/
OE.2.4.3.	CONTRAPISO F'C=175 kg/cm2 E=0.05m	m²	142	S/ 33.58	S/
OE.2.5	INSTALACIONES ELECTRICAS				
OE.2.5.1	CANALIZADORES, CONDUCTORES O TUBERIAS				
OE.2.5.1.	INSTALACIÓN DE TUBERIA PVC-SAP 20MM	m	525	S/ 4.80	S/
OE.2.5.1.	INSTALACIÓN DE CURVA DE 3/4"	m	476	S/ 1.20	S/ 571.20
OE.2.5.1.	INSTALACIÓN DE TUBERIA PVC-SAP 35MM	m	85	S/ 7.60	S/ 646.00
OE.2.5.1.	INSTALACIÓN DE CURVA DE 1 1/4"	und	45	S/ 2.30	S/ 103.50
OE.2.5.1. 5	INSTALACIÓN DE CAJAS RECTANGULAR DE PASE O SALIDA 100 X 50	und	68	S/ 18.00	S/ 1,224.00
OE.2.5.1. 6	INSTALACIÓN DE CAJAS OCTAGONALES PARA SALIDA DE LUZ EN	und	24	S/ 18.00	S/ 432.00
OE.2.5.1. 7	INSTALACIÓN DE CAJAS DE PASE 200 x 200 x 100 mm PARA	und	11	S/ 44.00	S/ 484.00
OE.2.5.1.	INSTALACIÓN DE CAJAS DE PASE 400 x 400 x 100	und	2	S/ 88.00	S/ 176.00
OE.2.5.1.	INSTALACIÓN DE TABLERO GENERAL DE 12	und	1	S/ 55.00	S/ 55.00
OE.2.5.1.	INSTALACIÓN DE TABLERO D-1 DE 12 POLOS	und	1	S/ 55.00	S/ 55.00
OE.2.5.1.	INSTALACIÓN DE TABLERO D-1 DE 24 POLOS	und	1	S/ 110.00	S/ 110.00
OE.2.5.2	SISTEMA DE PUESTA A TIERRA				
OE.2.5.2.	INSTALACION DE POZO A TIERRA	und	1	S/	S/
OE.2.6	INSTALACIONES SANITARIAS				
OE.2.6.1	SISTEMA DE AGUA FRIA				
OE.2.6.1.	REDES DE DISTRIBUCION Y ALIMENTACION				
OE.2.6.1.	TUBERIA PVC SAP DE 1/2" - A/F	m	24.5	S/ 21.00	S/ 514.50
OE.2.6.1.	TUBERIA PVC SAP DE 3/4" - A/F	m	64	S/ 25.00	S/
OE.2.6.1.	TUBERIA PVC SAP CLASE 10 DE 1"	m	6	S/ 28.00	S/ 168.00
OE.2.6.1.	VALVULA PARA AGUA FRIA				
OE.2.6.1.	VALVULA COMPUERTA DE Br DE 1/2" A/F	und	6	S/ 64.00	S/ 384.00
OE.2.6.1.	VALVULA COMPUERTA DE Br DE 3/4"	und	2	S/ 110.00	S/ 220.00
OE.2.6.1.	ACCESORIOS DE RED AGUA FRIA				
OE.2.6.1.	SALIDA DE PUNTO DE A/F DE 1/2"	und	12	S/ 30.00	S/ 360.00
OE.2.6.1.	SALIDA DE PUNTO DE AGUA/F DE 3/4"	und	2	S/ 32.00	S/ 64.00
OE.2.6.1.	SALIDA DE PUNTO DE AGUA DE 1"	und	1	S/ 36.00	S/ 36.00
OE.2.6.1.	INSTALACIÓN DE TANQUE ELEVADO DE 1100 LT	und	1	S/ 800.00	S/ 800.00
OE.2.6.1.	INSTALACIÓN DE BOMBA PERIFESRICA DE 1 HP.	und	1	S/ 480.00	S/ 480.00
OE.2.6.2	DEAGÜE Y VENTILACION				
OE.2.6.2.1	DESAGUE				
OE.2.6.2.1	SALIDA DE VENTILACIÓN DESAGUE EN PVC DE 2"	pto	3	S/ 48.00	S/ 144.00
OE.2.6.2.1	SALIDA DE DESAGUE EN PVC DE 2"	pto	6	S/ 32.00	S/ 192.00
OE.2.6.2.1	SALIDA DE SUMIDERO DESAGUE EN PVC DE 2"	pto	6	S/ 32.00	S/ 192.00
OE.2.6.2.1	TENDIDO DE TUBERIA DE DESAGUE DE 2"	m	38	S/ 18.00	S/ 684.00
OE.2.6.2.1	SALIDA DE DESAGUE EN PVC DE 4"	pto	2	S/ 48.00	S/ 96.00
OE.2.6.2.1	SALIDA REGISTRO ROSCADO DE 4"	pto	4	S/ 56.00	S/ 224.00
OE.2.6.2.1	TENDIDO DE TUBERIA DE DESAGUE DE 4"	m	77	S/ 24.00	S/ 1,848.00

OE.2.1.2	LOSA ALIGERADA					S/ 26,942.60
OE.2.1.2	ENCOFRADO Y DESENCOFRADO EN LOSA ALIGERADA	m²	82	S/ 46.05	S/	
OE.2.1.2	ACERO DE REFUERZO F'Y=4200 Kg/cm2	kg	1843	S/ 7.00	S/	
OE.2.1.2	CONCRETO, F'C=210 Kg/cm2	m³	12.81	S/ 600.00	S/ 7,686.00	
OE.2.1.2	LADRILLO DE TECHO N° 15	und	670	S/ 3.85	S/ 2,579.50	
OE.2.1.3	ESCALERA					S/ 2,848.10
OE.2.1.3	ENCOFRADO Y DESENCOFRADO EN ESCALERA	m²	12.66	S/ 46.05	S/	
OE.2.1.3	ACERO DE REFUERZO F'Y=4200Kg/cm2	kg	183	S/ 7.00	S/ 1,281.00	
OE.2.1.3	CONCRETO, F'C=210 Kg/cm2	m³	1.56	S/ 600.00	S/ 936.00	
OE.2.1.3	CURADO DE ESCALERA CON ADITIVO QUIMICO	m²	12.66	S/ 3.80	S/	
OE.2.2	ARQUITECTURA					S/ 30,627.43
OE.2.2.1	MUROS Y TABIQUES DE ALBAÑILERIA					
OE.2.2.1	LADRILLO DE SOGA E=0.15	m²	149	S/ 80.00	S/ 11,920.00	
OE.2.2.2	REVOQUES ENLUCIDOS Y MOLDURAS					
OE.2.2.2	TARRAJEO DE CIELO RASO	m²	82	S/ 37.60	S/ 3,083.20	
OE.2.2.2	TARRAJEO DE MUROS INTERIORES	m²	198	S/ 37.60	S/ 7,444.80	
OE.2.2.2	TARRAJEO DE MUROS EXTERIORES	m²	82	S/ 37.60	S/ 3,083.20	
OE.2.2.2	TARRAJEO DE COLUMNAS	m²	12	S/ 37.60	S/ 451.20	
OE.2.2.2	TARRAJEO DE ESCALERA	m²	13.66	S/ 37.60	S/ 513.62	
OE.2.2.2	VESTIDURA DE DERRAMES	m	85	S/ 16.21	S/ 1,377.85	
OE.2.2.3	PISOS Y PAVIMENTOS					
OE.2.2.3	CONTRAPISO F'C=175 kg/cm2 E=0.05m	m²	82	S/ 33.58	S/ 2,753.56	
OE.2.3	INSTALACIONES ELECTRICAS					
OE.2.3.1	CANALIZADORES, CONDUCTORES O TUBERIAS					
OE.2.3.1	INSTALACIÓN DE TUBERIA PVC-SAP 20MM	m	275	S/ 4.80	S/	
OE.2.3.1	INSTALACIÓN DE CURVA DE 3/4"	m	226	S/ 1.20	S/ 271.20	
OE.2.3.1	INSTALACIÓN DE TUBERIA PVC-SAP 35MM	m	35	S/ 7.60	S/	
OE.2.3.1	INSTALACIÓN DE CURVA DE 1 1/4"	und	16	S/ 2.30	S/ 36.80	
OE.2.3.1.5	INSTALACIÓN DE CAJAS RECTANGULAR DE PASE O SALIDA 100 X 50 mm	und	35	S/ 18.00	S/ 630.00	
OE.2.3.1.6	INSTALACIÓN DE CAJAS OCTAGONALES PARA SALIDA DE LUZ EN TECHO	und	33	S/ 18.00	S/ 594.00	
OE.2.3.1.7	INSTALACIÓN DE CAJAS DE PASE 200 x 200 x 100 mm PARA DISTRIBUCIÓN DE ACOMETIDA	und	6	S/ 44.00	S/ 264.00	
OE.2.3.1	INSTALACIÓN DE TABLERO D-2 DE 24 POLOS	und	1	S/ 110.00	S/	
OE.2.4	INSTALACIONES SANITARIAS					
OE.2.4.1	SISTEMA DE AGUA FRIA					
OE.2.4.1	REDES DE DISTRIBUCION Y ALIMENTACION					
OE.2.4.1	TUBERIA PVC SAP DE 1/2" - A/F	m	12	S/ 21.00	S/ 252.00	
OE.2.4.1	TUBERIA PVC SAP DE 3/4" - A/F	m	21	S/ 25.00	S/ 525.00	
OE.2.4.1	VALVULA PARA AGUA FRIA					
OE.2.4.1	VALVULA COMPUERTA DE Br DE 1/2" A/F	und	2	S/ 64.00	S/ 128.00	
OE.2.4.1	VALVULA COMPUERTA DE Br DE 3/4"	und	1	S/ 110.00	S/ 110.00	
OE.2.4.1	ACCESORIOS DE RED AGUA FRIA					
OE.2.4.1	SALIDA DE PUNTO DE A/F DE 1/2"	und	3	S/ 30.00	S/ 90.00	

OE.2.4.2	DEAGÜE Y VENTILACION					S/ 1,356.00
OE.2.4.2.1	DESAGUE					S/ 1,356.00
OE.2.4.2.1	SALIDA DE VENTILACIÓN DESAGUE EN PVC DE 2"	pto	3	S/ 48.00	S/ 144.00	
OE.2.4.2.1	SALIDA DE DESAGUE EN PVC DE 2"	pto	2	S/ 32.00	S/ 64.00	
OE.2.4.2.1	SALIDA DE SUMIDERO DESAGUE EN PVC DE 2"	pto	3	S/ 32.00	S/ 96.00	
OE.2.4.2.1	TENDIDO DE TUBERIA DE DESAGUE DE 2"	m	8	S/ 18.00	S/ 144.00	
OE.2.4.2.1	SALIDA DE DESAGUE EN PVC DE 4"	pto	1	S/ 48.00	S/ 48.00	
OE.2.4.2.1	SALIDA REGISTRO ROSCADO DE 4"	pto	1	S/ 56.00	S/ 56.00	
OE.2.4.2.1	TENDIDO DE TUBERIA DE DESAGUE DE 4"	m	16	S/ 24.00	S/ 384.00	
OE.2.4.2.1	TENDIDO DE TUBERIA DE DESAGUE DE 3"	m	15	S/ 28.00	S/ 420.00	
OE.2	AZOTEA					S/ 50,882.21
OE.2.1	OBRAS DE CONCRETO ARMADO					S/ 25,502.60
OE.2.1.1	COLUMNAS (ACERO + ENCOFRADO Y DESENCONFRADO + VACEADO)					S/ 11,680.00
OE.2.1.1.1	COLUMNA TIPO C-1 (0.40x 0.20 m) - INCLUYE EL ENCOFRADO +	und	3	S/ 720.00	S/ 2,160.00	
OE.2.1.1.2	COLUMNA TIPO C-2 (0.40+0.40x 0.15 m) - INCLUYE EL ENCOFRADO +	und	3	S/ 960.00	S/ 2,880.00	
OE.2.1.1.3	COLUMNA TIPO C-4 (0.30x 0.15 m) - INCLUYE EL ENCOFRADO +	und	3	S/ 420.00	S/ 1,260.00	
OE.2.1.1.4	PLACA 1 (1.00 + 0.15 + 0.15x 0.15 m) - INCLUYE EL ENCOFRADO +	und	1	S/ 1,280.00	S/ 1,280.00	
OE.2.1.1.5	PLACA 2 (0.50x 0.15 m) - INCLUYE EL ENCOFRADO + ACERO +	und	4	S/ 600.00	S/ 2,400.00	
OE.2.1.1.6	PLACA 3 (0.75 x 0.15 m) - INCLUYE EL ENCOFRADO + ACERO +	und	2	S/ 850.00	S/ 1,700.00	
OE.2.1.2	LOSA ALIGERADA					S/ 13,822.60
OE.2.1.2.1	ENCOFRADO Y DESENCOFRADO EN LOSA ALIGERADA	m²	42	S/ 46.05	S/ 1,934.10	
OE.2.1.2.2	ACERO DE REFUERZO F'Y=4200 Kg/cm2	kg	953	S/ 7.00	S/ 6,671.00	
OE.2.1.2.3	CONCRETO, F'C=210 Kg/cm2	m³	6.45	S/ 600.00	S/ 3,870.00	
OE.2.1.2.4	LADRILLO DE TECHO N° 15	und	350	S/ 3.85	S/ 1,347.50	
OE.2.2	ARQUITECTURA					S/ 19,426.61
OE.2.2.1	MUROS Y TABIQUES DE ALBAÑILERIA					S/ 7,840.00
OE.2.2.1.1	LADRILLO DE SOGA E=0.15	m²	98	S/ 80.00	S/ 7,840.00	
OE.2.2.2	REVOQUES ENLUCIDOS Y MOLDURAS					S/ 10,176.25
OE.2.2.2.1	TARRAJEO DE CIELO RASO	m²	42	S/ 37.60	S/ 1,579.20	
OE.2.2.2.2	TARRAJEO DE MUROS INTERIORES	m²	98	S/ 37.60	S/ 3,684.80	
OE.2.2.2.3	TARRAJEO DE MUROS EXTERIORES	m²	82	S/ 37.60	S/ 3,083.20	
OE.2.2.2.4	TARRAJEO DE COLUMNAS	m²	12	S/ 37.60	S/ 451.20	
OE.2.2.2.5	VESTIDURA DE DERRAMES	m	85	S/ 16.21	S/ 1,377.85	
OE.2.2.3	PISOS Y PAVIMENTOS					S/ 1,410.36
OE.2.2.3.1	CONTRAPISO F'C=175 kg/cm2 E=0.05m	m²	42	S/ 33.58	S/ 1,410.36	
OE.2.3	INSTALACIONES ELECTRICAS					S/ 3,492.00
OE.2.3.1	CANALIZADORES, CONDUCTORES O TUBERIAS					S/ 3,492.00
OE.2.3.1.1	INSTALACIÓN DE TUBERIA PVC-SAP 20MM	m	275	S/ 4.80	S/ 1,320.00	
OE.2.3.1.2	INSTALACIÓN DE CURVA DE 3/4"	m	226	S/ 1.20	S/ 271.20	
OE.2.3.1.3	INSTALACIÓN DE TUBERIA PVC-SAP 35MM	m	35	S/ 7.60	S/ 266.00	
OE.2.3.1.4	INSTALACIÓN DE CURVA DE 1 1/4"	und	16	S/ 2.30	S/ 36.80	
OE.2.3.1.5	INSTALACIÓN DE CAJAS RECTANGULAR DE PASE O SALIDA 100 X 50	und	35	S/ 18.00	S/ 630.00	
OE.2.3.1.6	INSTALACIÓN DE CAJAS OCTAGONALES PARA SALIDA DE LUZ EN	und	33	S/ 18.00	S/ 594.00	
OE.2.3.1.7	INSTALACIÓN DE CAJAS DE PASE 200 x 200 x 100 mm PARA	und	6	S/ 44.00	S/ 264.00	
OE.2.3.1.8	INSTALACIÓN DE TABLERO D-2 DE 24 POLOS	und	1	S/ 110.00	S/ 110.00	
OE.2.4	INSTALACIONES SANITARIAS					S/ 2,461.00
OE.2.4.1	SISTEMA DE AGUA FRIA					S/ 1,105.00
OE.2.4.1.	REDES DE DISTRIBUCION Y ALIMENTACION					S/ 777.00
OE.2.4.1.	TUBERIA PVC SAP DE 1/2" - A/F	m	12	S/	S/ 252.00	
OE.2.4.1.	TUBERIA PVC SAP DE 3/4" - A/F	m	21	S/	S/ 525.00	

OE.2.4.1. VALVULA PARA AGUA FRIA					S/ 238.00
OE.2.4.1. VALVULA COMPUERTA DE Br DE 1/2" A/F	und	2	S/	S/ 128.00	
OE.2.4.1. VALVULA COMPUERTA DE Br DE 3/4"	und	1	S/	S/ 110.00	
OE.2.4.1. ACCESORIOS DE RED AGUA FRIA					S/ 90.00
OE.2.4.1. SALIDA DE PUNTO DE A/F DE 1/2"	und	3	S/	S/ 90.00	
OE.2.4.2 DEAGÜE Y VENTILACION					S/ 1,356.00
OE.2.4.2. DESAGUE					S/ 1,356.00
OE.2.4.2. SALIDA DE VENTILACIÓN DESAGUE EN PVC DE 2"	pto	3	S/	S/ 144.00	
OE.2.4.2. SALIDA DE DESAGUE EN PVC DE 2"	pto	2	S/	S/ 64.00	
OE.2.4.2. SALIDA DE SUMIDERO DESAGUE EN PVC DE 2"	pto	3	S/	S/ 96.00	
OE.2.4.2. TENDIDO DE TUBERIA DE DESAGUE DE 2"	m	8	S/	S/ 144.00	
OE.2.4.2. SALIDA DE DESAGUE EN PVC DE 4"	pto	1	S/	S/ 48.00	
OE.2.4.2. SALIDA REGISTRO ROSCADO DE 4"	pto	1	S/	S/ 56.00	
OE.2.4.2. TENDIDO DE TUBERIA DE DESAGUE DE 4"	m	16	S/	S/ 384.00	
OE.2.4.2. TENDIDO DE TUBERIA DE DESAGUE DE 3"	m	15	S/	S/ 420.00	

Costo Directo		S/ 413,344.20
Gastos Generales	0.00%	S/ -
Utilidad	10.00%	S/ 41,334.42
TOTAL :		**S/ 454,678.62**

SON: CUATROCIENTOS CINCUENTA Y CUATRO MIL SEIS CIENTOS SETENTA Y OCHO CON 62/100

2. ACERCA DE LOS GASTOS GENERALES QUE NO ESTAN INCLUIDOS:

- Vigilancia Nocturna.
- tramite y obtención de la Licencia de Construcción. (no Incluye la impresión del expediente).
- tramite del ingreso y Compra del medidor a EPPS GRAU.
- tramite de solicitud de punto de energía a ENOSA para la construcción.
- Supervisión de Obra y entrega de reporte de avance semanales.

3. TERMINOS COMERCIALES:

* Forma de Pago: 15% de Adelanto – 85% por valorización Semanales.
* Tiempo de Ejecución: 140 Dias.
* El Precio de Esta Cotización **NO INCLUYE EL IGV**.
* El Presupuesto incluye Materiales, mano de obra y equipos.
* Oferta Valida: Solo 30 Días.

KCC INGENIERIA Y CONSTRUCCION SAC.
Teléfono: 970361507

Correo Electrónico: Kccingenieriayconstruccionsac@hotmail.com
BBVA Continental Soles:
Cuenta De Ahorros: 0011-0554-0200263688
Cuenta Interbancaria: 011-5540-0020026368830

A La Espera De Sus Gratas Órdenes.

ING. KEVIN ANATHOLY CORNEJO CARNERO
GERENTE GENERAL
KCC INGENIERIA Y CONSTRUCCIÓN SAC

Layseca Asociados

N° de Solicitud Banco	**1364852**
N° de Servicio Tasadora	**60347-2026**
Fecha de Expedición	30-Abr-2026
Fecha de Caducidad	30-Abr-2027

ANEXO IV

SOLICITUD DE CONSTRUYO

BBVA

Solicitud Construyo

1. Nombre del cliente: Heidy Melissa Saavedra Feijoo / Hugo Fernando Espinoza Ramos

2. Dirección del inmueble o ubicación (Indicar referencias):
MZA A11 LT 19 URB LAS PALMERAS
I ETAPA - CASTILLA

3. Nº de Partida Electrónica / Copia Literal (documentación registral):

4. Cuadro de áreas (disgregar por pisos, áreas construidas existentes y nuevas):

	ÁREAS TECHADAS (Existentes)	ÁREAS TECHADAS (Nuevas)
PRIMER PISO		79.50 m²
SEGUNDO PISO		79.50 m²
TERCER PISO		76.00 m²
CUARTO PISO		
ÁREA TOTAL		235 m²

5. Detalle del financiamiento (indicar si se va a financiar todos los niveles, solo en casco gris, los primeros dos pisos, etc.)
FINANCIAMIENTO DE PROYECTO UNIFAMILIAR CASCO GRIS MAS ACABADOS HASTA EL TERCER PISO

6. Descripción del proyecto:
Proyecto unifamiliar de 3 pisos, primer piso jardin con cochera como zona de estacionamiento. Segundo piso cocina sala comedor baño y un estudio. Tercer piso dormitorios con baños.

7. Presupuesto global por especialidades (Soles):

PARTIDAS DE LA CONSTRUCCIÓN	VALOR (S/.)
Estructura	S/ 204 009.85
Arquitectura	S/ 130 638.89
Instalaciones Sanitarias	S/ 18 063.50
Instalaciones Eléctricas	S/ 18 202.70
Instalaciones Mecánicas	S/ 0
Sub Total	S/ 370 934.94
Utilidad	S/ 11 128.05
Gastos Generales	S/ 11 128.05
IGV	S/ 66 768.29
TOTAL	S/ 459 959.33

8. Fecha de finalización de obra estimada:
CINCO MESES DESPUES DEL PRIMER DESEMBOLSO


Stefania Chapilliquen Castillo
Ejecutivo Personas
Oficina Real Plaza Piura

DNI 43040266

Heidy Melissa Saavedra Feijoo

ANEXO IV

PLANOS

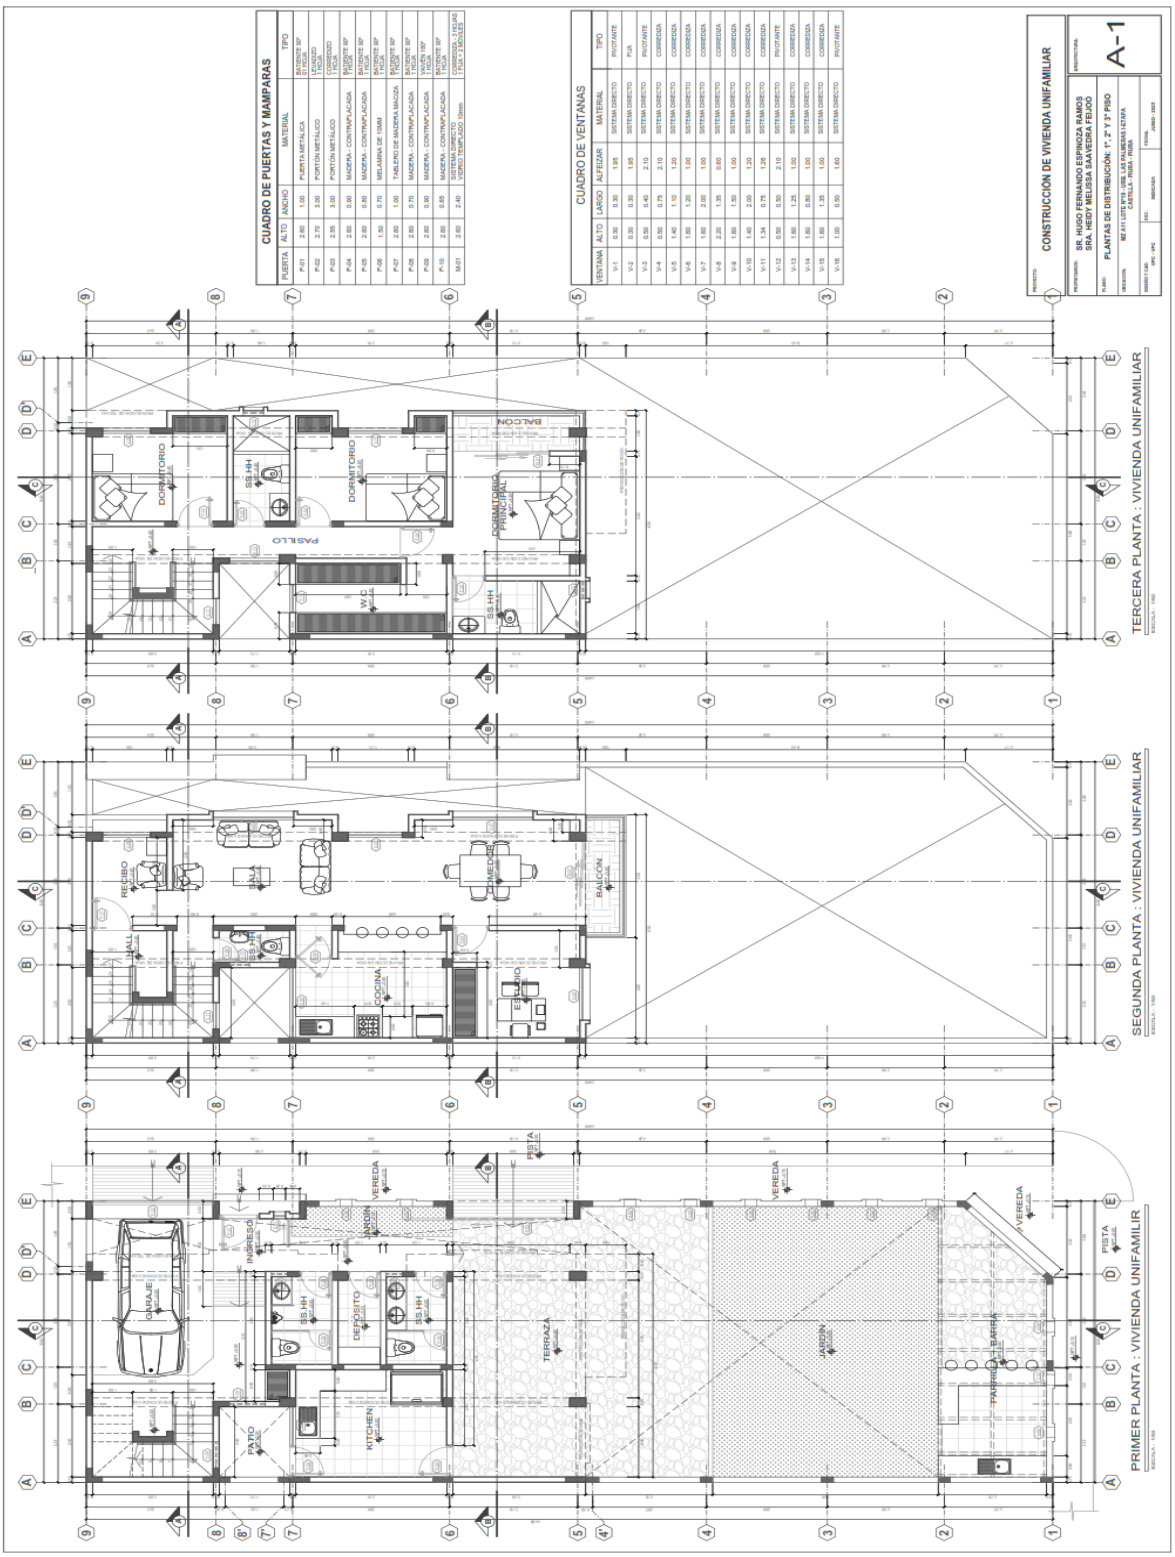


Layseca Asociados

N° de Solicitud Banco	**1364852**
N° de Servicio Tasadora	**60347-2026**
Fecha de Expedición	30-Abr-2026
Fecha de Caducidad	30-Abr-2027

ANEXO IV

PLANOS

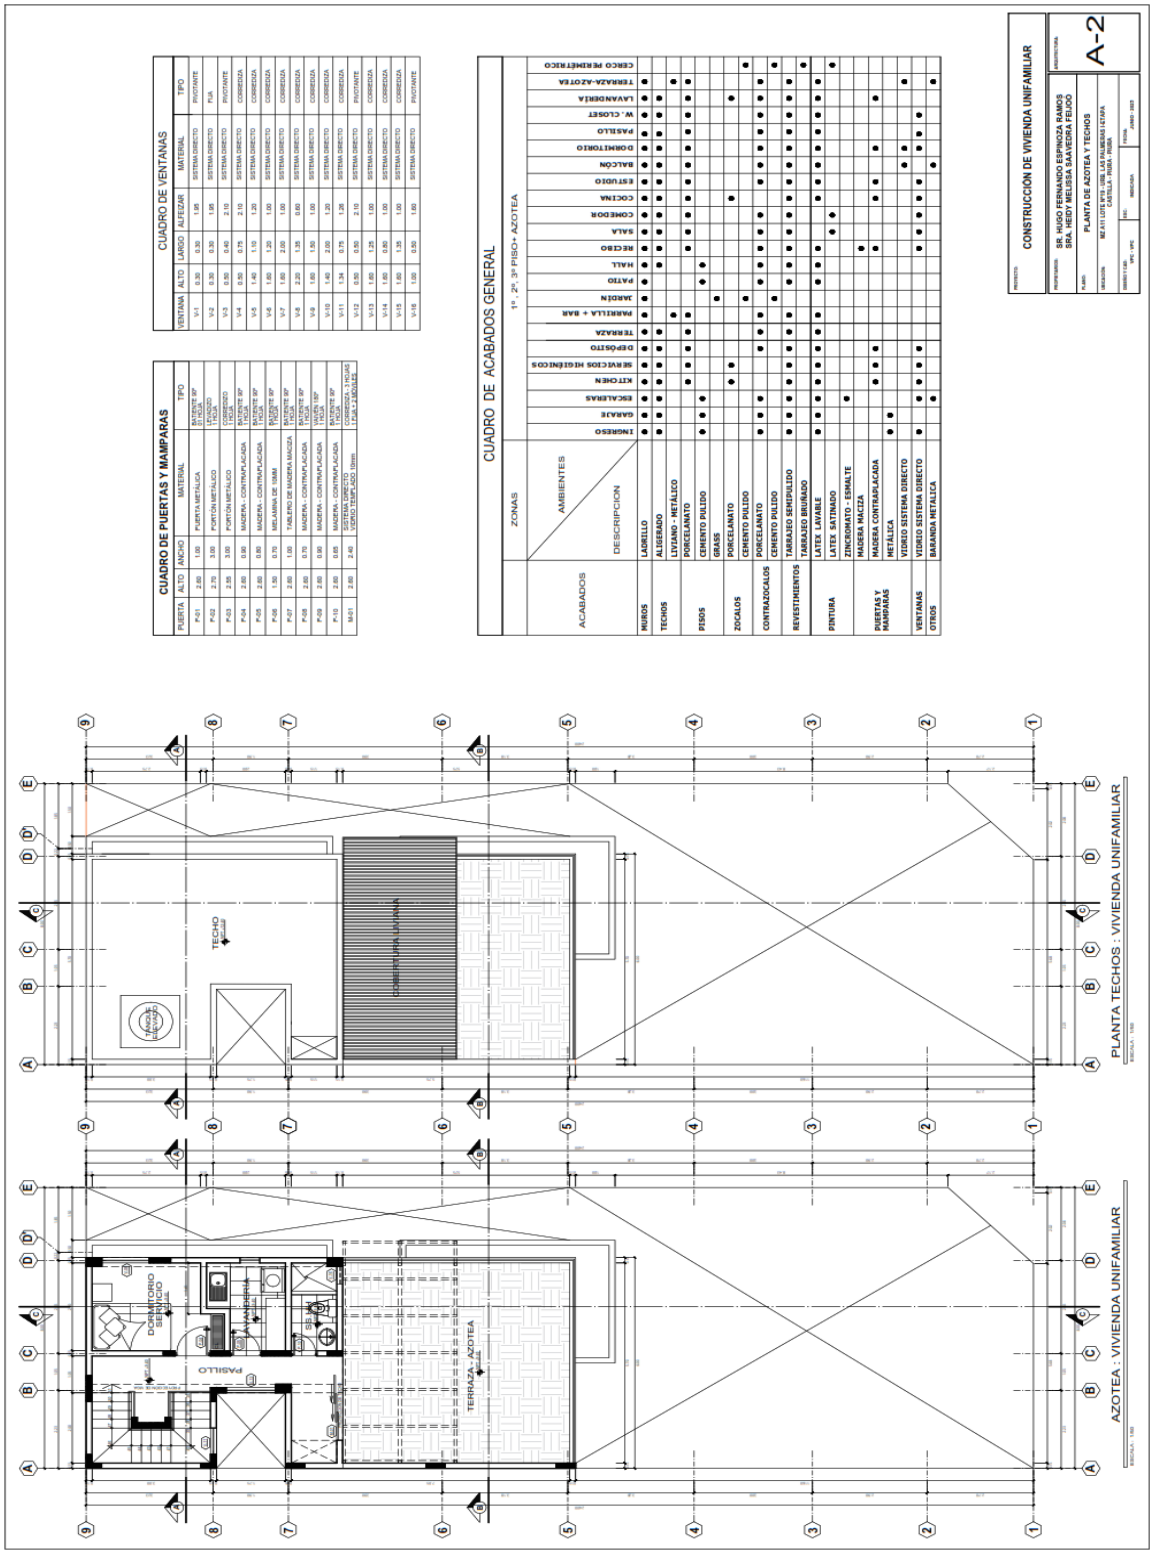


Layseca Asociados


N° de Solicitud Banco	**1364852**
N° de Servicio Tasadora	**60347-2026**
Fecha de Expedición	30-Abr-2026
Fecha de Caducidad	30-Abr-2027

ANEXO II

PLANO DE ZONIFICACIÓN Y VALIDACIÓN DE LOCALIZACIÓN (VISTA GOOGLE MAPS)

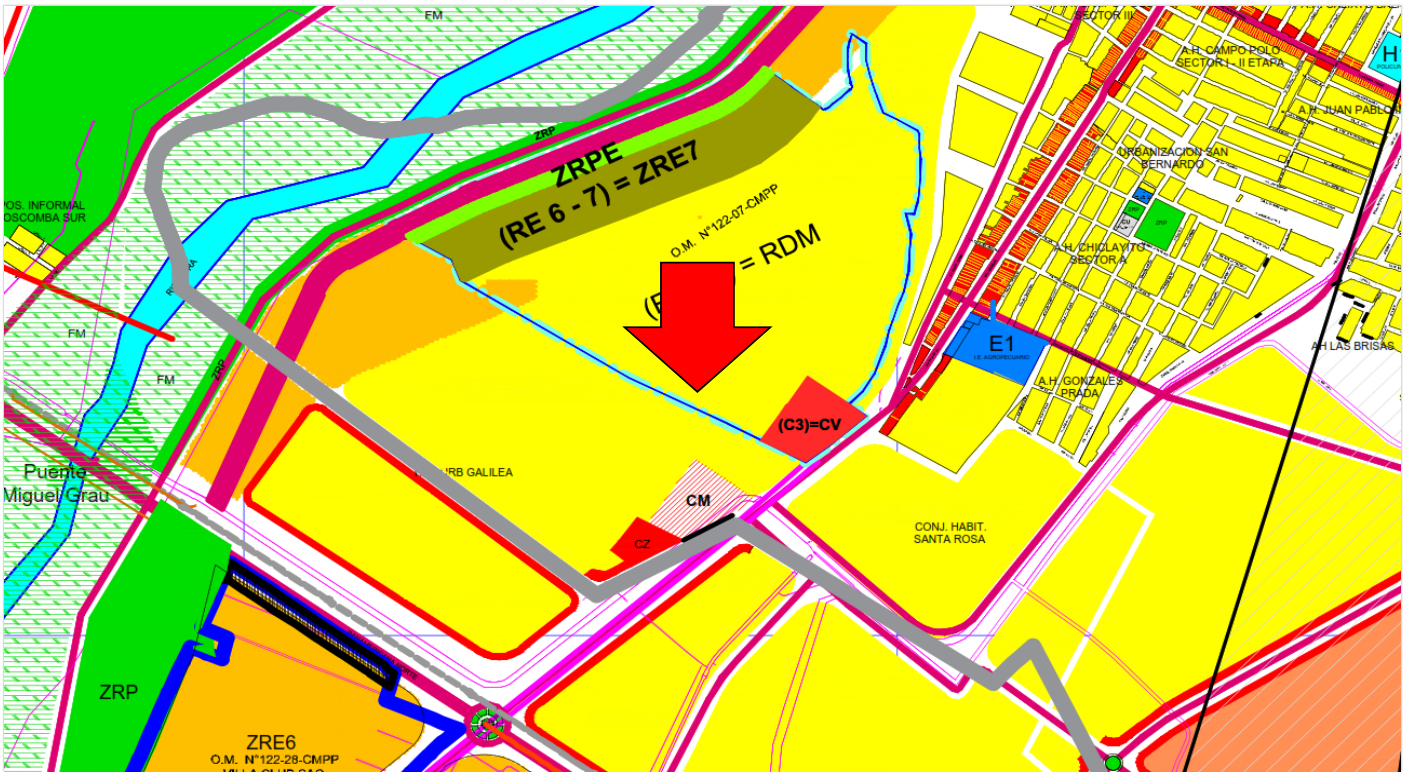

PLANO DE ZONIFICACIÓN

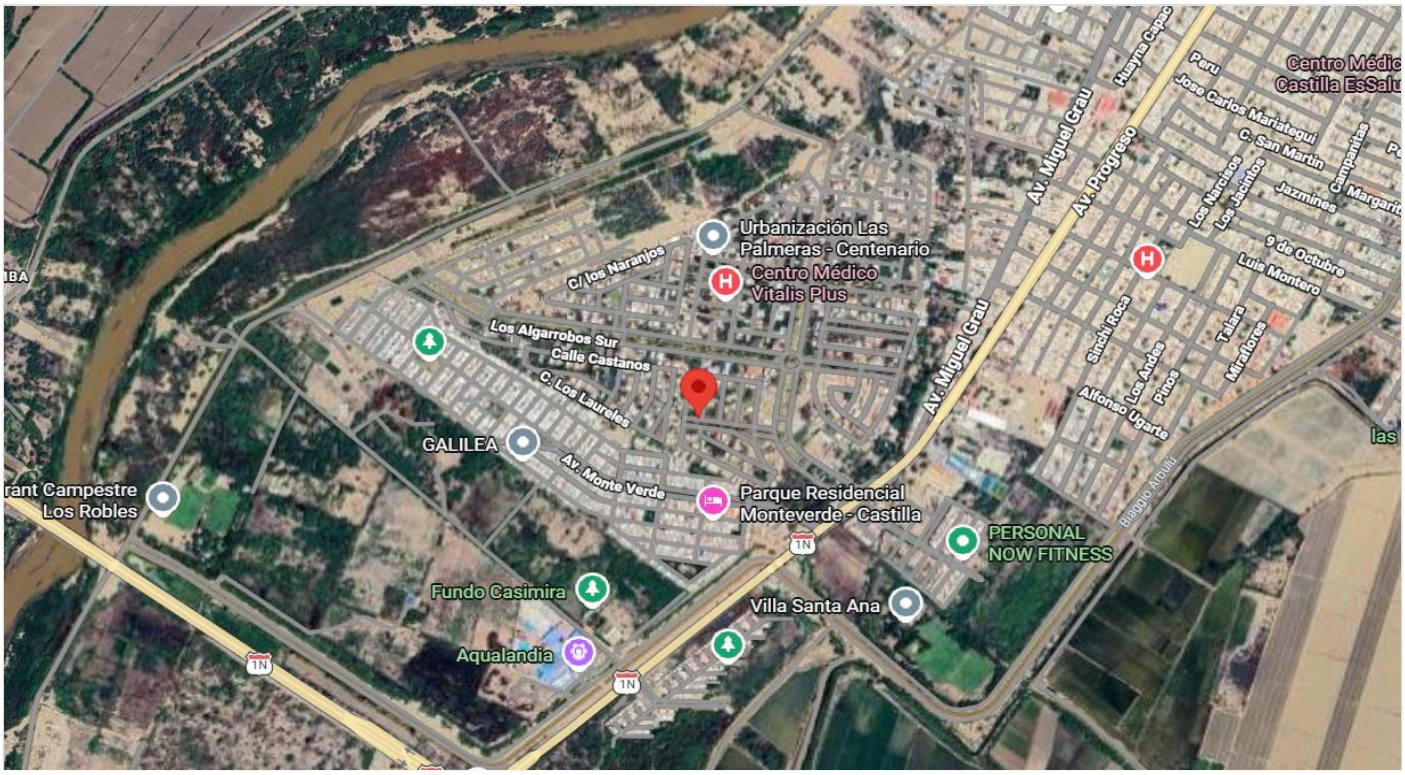


VALIDACIÓN DE LOCALIZACIÓN (VISTA GOOGLE MAPS)

Layseca Asociados


N° de Solicitud Banco	**1364852**
N° de Servicio Tasadora	**60347-2026**
Fecha de Expedición	30-Abr-2026
Fecha de Caducidad	30-Abr-2027

ANEXO III

UBICACIÓN REFERENCIAL SEGÚN BASE GRÁFICA REGISTRAL (BGR) DE SUNARP

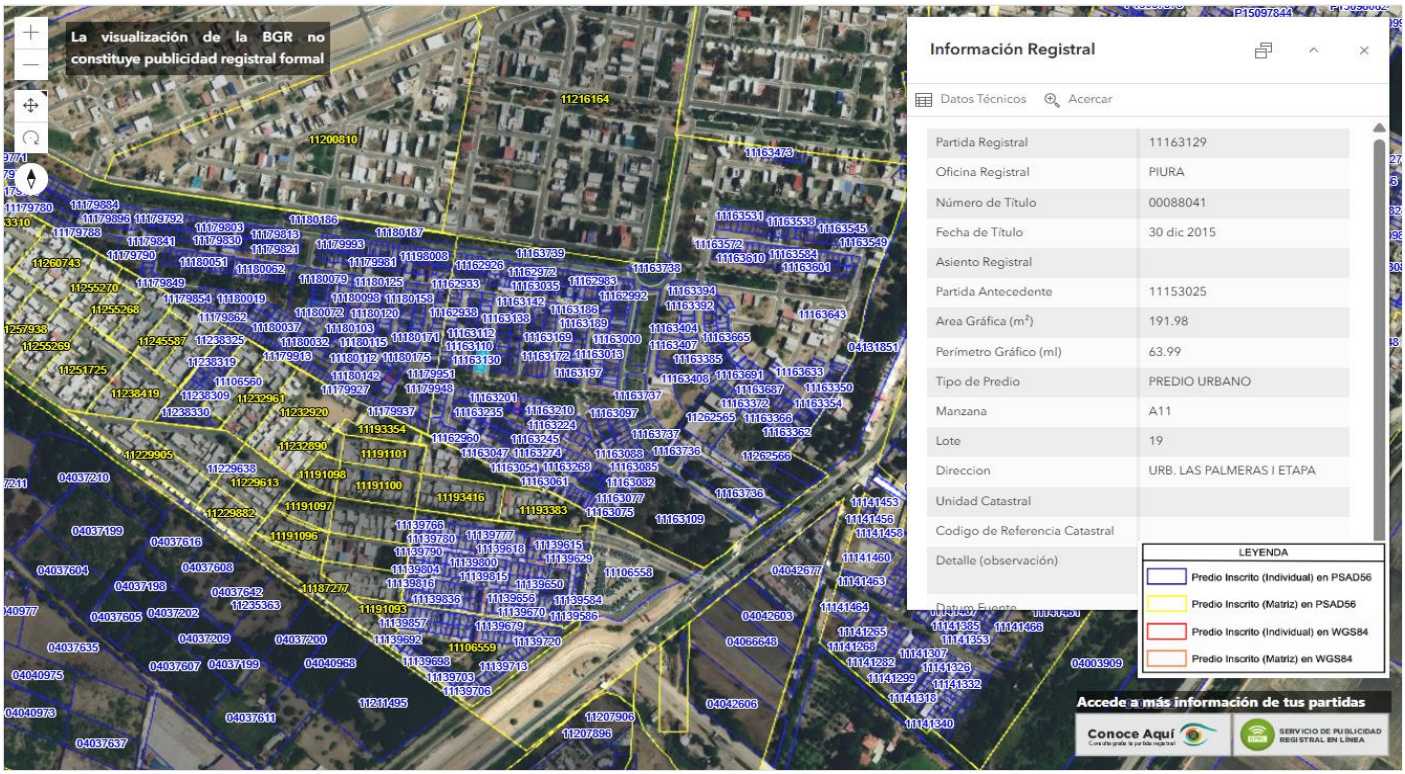

UBICACIÓN REFERENCIAL SEGÚN BASE GRÁFICA REGISTRAL (BGR) DE SUNARP

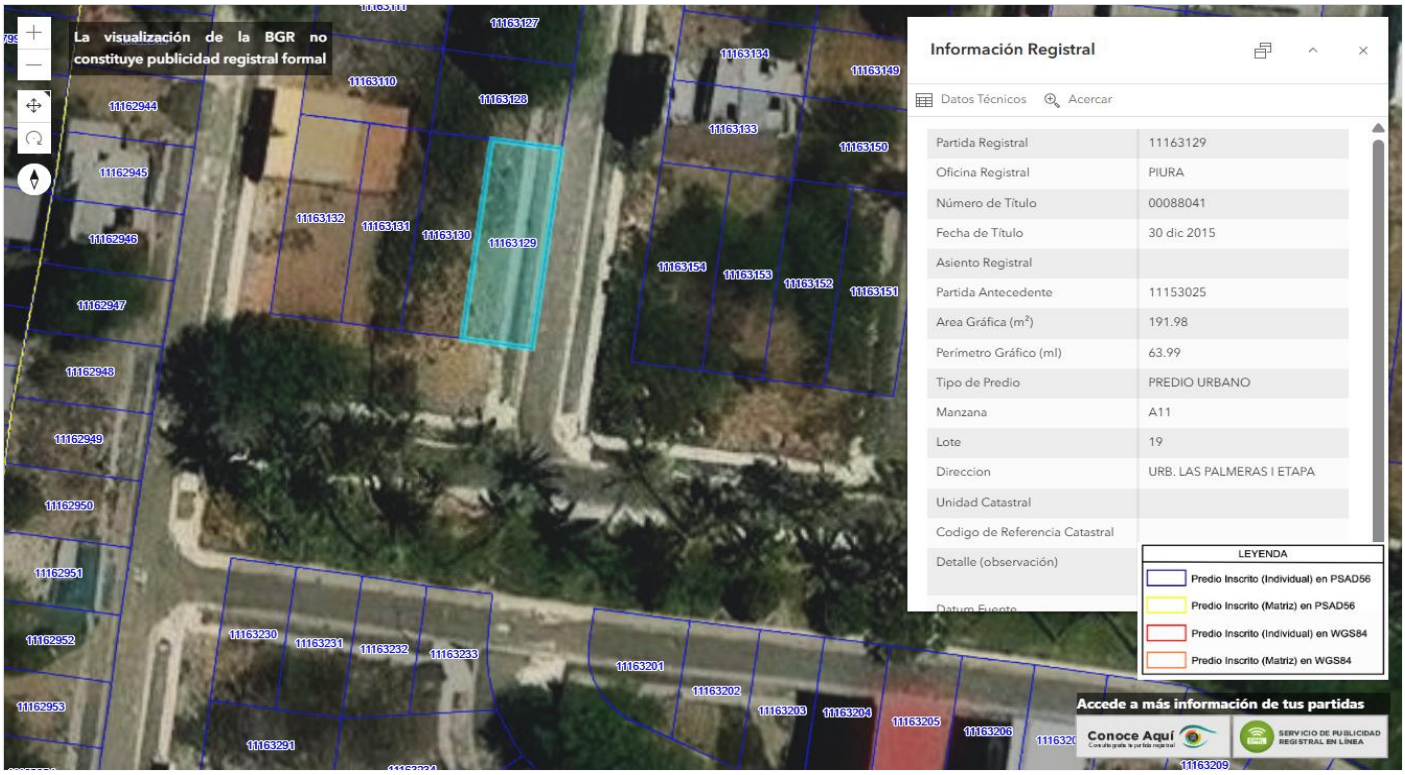

UBICACIÓN REFERENCIAL SEGÚN BASE GRÁFICA REGISTRAL (BGR) DE SUNARP

Layseca Asociados

N° de Solicitud Banco	**1364852**
N° de Servicio Tasadora	**60347-2026**
Fecha de Expedición	30-Abr-2026
Fecha de Caducidad	30-Abr-2027

ANEXO IV

PRESUPUESTO

PARTIDA DE LA	VALOR S/	% AVANCE	AVANCE TOTAL S/
Estructura	204,009.85	0.00%	0.00
Arquitectura	130,658.89	0.00%	0.00
Instalaciones Sanitarias	18,063.50	0.00%	0.00
Instalaciones Eléctricas	18,201.70	0.00%	0.00
Instalaciones Mecánicas	0.00		0.00
Sub total	**370,933.94**		**0.00**
Utilidad	11,128.05		
Gastos Generales	11,128.05		
IGV	**66,768.29**		**0.00**
TOTAL S/	**459,958.33**	**0.000%**	**0.00**

TOTAL US$	**131,944.44**		**0.00**

$3.486 Tipo de Cambio del mes