

Layseca Asociados

N° de Solicitud Banco	**1326668**
N° de Servicio Tasadora	**58168-2026**
Fecha de Expedición	26-Mar-2026
Fecha de Caducidad	26-Mar-2027

BANCO BBVA PERU

PRIMER CONSTRUYO

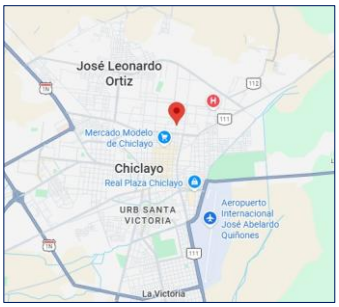

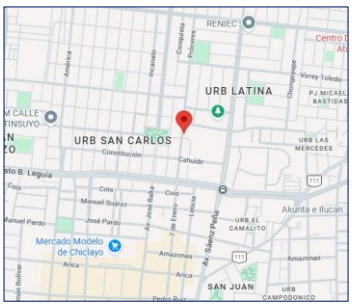



Tipo de Tasación	Hipotecaria	Nueva		**N° de Garantía**	-
Solicitante	BBVA CONTINENTAL	OF.	OFICINA UNO	FUNC.	SANDY CHAVEZ
Cliente	Davila Diaz Katherine Milagros				
Propietario (s)	Odar Cornejo Rolando Enrique, Odar Cornejo Antonio, Odar Cornejo Martha, Odar Cornejo Margot Alicia, Odar Ordoñez Gustavo Enrique, Odar Ordoñez Kattya Mirella, Odar Ordoñez Walter Alberto, Odar Ordoñez Jesus Manuel				
Fecha de inspección	30/01/2026				
Dirección Registral	Calle Los Proceres Num 340-342, Distrito Jose Leonardo Ortiz, Provincia Chiclayo, Departamento Lambayeque				
Dirección Municipal	Urb. San Carlos - Ca. Proceres 00340, Distrito Jose Leonardo Ortiz, Provincia Chiclayo, Departamento Lambayeque				
Dirección según inspección ocular	Calle Proceres 340 Urb. San Carlos, Distrito Jose Leonardo Ortiz, Provincia Chiclayo, Departamento Lambayeque				
Tipo de inmueble	Terreno	**Ocupante**	Desocupado		

Descripción	TIPO DE USO (*)	%	TIPO DE USO (*)	%
	Sin Uso	100%		

Zonificación	CV	**Material de construcción**	Ladrillo		
Año de construcción	-	**Obra finalizada**	SÍ		NO	X
	*De acuerdo a expediente documental y tipo de construcción				
Área de terreno	144.00 m2	**Área construida**	100.00 m2		
Declaratoria de fábrica	SÍ		NO	X	**Tipo de declaratoria**	TOTAL		PARCIAL	
Cargas	SÍ		NO	X	**Gravámenes**	SÍ		NO	X
Zona de Alta Peligrosidad	SÍ		NO	X	**Zona de Riesgo (Desastre natural)**	SÍ		NO	X
Predio Agrícola	SÍ		NO	X	**Predio Rústico**	SÍ		NO	X

VALORES TOTALES	MONEDA	VALOR TOTAL (REDONDEADO)	TERRENO	EDIFICACION PROYECTADA
VALOR COMERCIAL PROYECTADO	US$	226,000.00	127,440.00	98,067.49
	S/	783,542.00	441,834.48	339,999.99
VALOR DE REALIZACIÓN PROYECTADO	US$	181,000.00	101,952.00	78,453.99
	S/	627,527.00	353,467.58	271,999.99

VALORES INSCRITOS EN RR.PP.	MONEDA	VALOR TOTAL	TERRENO	EDIFICACIÓN
VALOR COMERCIAL	US$	127,440.00	127,440.00	
	S/	441,834.48	441,834.48	
VALOR DE REALIZACIÓN	US$	101,952.00	101,952.00	
	S/	353,467.58	353,467.58	

VALORES NO INSCRITOS EN RR.PP.	MONEDA	VALOR TOTAL	AVANCE DE OBRA	% AVANCE DE OBRA
VALOR COMERCIAL	US$			0.00%
	S/			

VALORES DE RECONSTRUCCIÓN	MONEDA	VALOR TOTAL (VSN PROYECTADO)	VALOR DE RECONSTRUCCIÓN (VSN DEL AVANCE)	(VSN PENDIENTE)	FECHA ESTIMADA DE FINALIZACIÓN
V. RECONSTRUCCIÓN (INCL. CONSTRUCCIONES DECLAR. Y NO DECLAR.)	US$	98,067.49		98,067.49	
	S/	339,999.99		339,999.99	1/09/2026

Tipo de cambio aplicado 3.467 Soles / Dólar

Observaciones

- La ubicación del inmueble se verifico mediante código de suministro eléctrico y recibo correspondiente.
- Se trata de un proyecto de construcción de vivienda, las áreas de terreno, áreas construidas, áreas ocupadas, etc. fueron obtenidas de la documentación proporcionada por el cliente.
- De acuerdo con la solicitud construyo, se proyecta una construcción de dos niveles; sin embargo, se precisa que la entidad financiera otorgará financiamiento únicamente para la ejecución del primer nivel.

Advertencias

- **Se encontraron errores de sumatoria en el presupuesto digital proporcionado (archivo Excel), se recomienda verificar y rectificar para el segundo construyo.**
- **Se han considerado montos que corresponden al 2do nivel en el presupuesto.**

	Si	No	
Inmueble en zona de riesgo		X	Ubicado en zona urbana, con habilitación urbana completa.

Valor comercial Tasación Anterior US$ S/ FECHA PERITO

LAYSECA ASOCIADOS SAC
REPEV Nº 2741-2013

PERITO	Arq. Maria Fernanda Miena Carbajal
REPEV	N° 3749-2016
CAP	N° 16376

PERITO	Ing. Manuel Barboza Oviedo
REPEV	N° 02668-2022
CIP	N° 258213

Layseca Asociados

N° de Solicitud Banco	**1326668**
N° de Servicio Tasadora	**58168-2026**
Fecha de Expedición	26-Mar-2026
Fecha de caducidad	26-Mar-2027

MEMORIA DESCRIPTIVA

1. ANTECEDENTES

Objeto y Propósito: Estimar el Valor Comercial del inmueble para fines de Garantía Hipotecaria

Alcance y Limitaciones: Durante la visita SI se dieron las facilidades para la inspección ocular y toma de registro fotográfico al interior del inmueble.

Reglamentación: Reglamento Nacional de Tasaciones - R.M. Nº 172-2016-VIVIENDA, Resolución Ministerial N° 424-2017-VIVIENDA (modificación), Resolución Ministerial N° 124-2020-VIVIENDA y Resolución S.B.S N° 11356-2008 para la determinación del valor de realización.

Metodología Empleada: Se utilizan los Métodos Directos (Comparación, Costos) o Indirectos establecidos en el Artículo 3. Inciso 3.1.5 del Título I del Reglamento Nacional de Tasaciones del Perú.

Documentación Proporcionada

X	Partida Registral	X	Predio Urbano	X	Planos		CRI
	Parámetros Urb.		Tasación anterior		Cuadro de acabados		Memoria Des.
	Otros	X	Presupuesto de obra				

Titulación e Inscripción

		Nº	Fecha	Oficina Registral
Principal	Partida Electrónica	02011642	20/01/2026	Chiclayo
Secundaria				
Secundaria				
Secundaria				

2. DATOS GENERALES

Cliente: Davila Diaz Katherine Milagros

Propietario(s): Odar Cornejo Rolando Enrique, Odar Cornejo Antonio, Odar Cornejo Martha, Odar Cornejo Margot Alicia, Odar Ordoñez Gustavo Enrique, Odar Ordoñez Kattya Mirella, Odar Ordoñez Walter Alberto, Odar Ordoñez Jesus Manuel

Fecha de Inspección: 30/01/2026

Ocupante: Desocupado

Georeferencias: Latitud -6.760888 Longitud -79.836221 (*) Datos obtenidos Google Maps

Ubicación según Partida Electrónica: Calle Los Proceres Num 340-342, Distrito Jose Leonardo Ortiz, Provincia Chiclayo, Departamento Lambayeque

Ubicación según el Predio Urbano: Urb. San Carlos - Ca. Proceres 00340, Distrito Jose Leonardo Ortiz, Provincia Chiclayo, Departamento Lambayeque

Ubicación Según la Inspección Ocular: Calle Proceres 340 Urb. San Carlos, Distrito Jose Leonardo Ortiz, Provincia Chiclayo, Departamento Lambayeque

3. CONDICIONES URBANISTICAS DEL ENTORNO

Características del Sector y del Entorno

Tipo de Zona	Urbana	Demanda / Interés	Media
Uso Predominante	Vivienda	Zonificación	CV
Desarrollo	Estacionario	Altura de Edificación	Nula
Nivel Socioeconómico	Estrato Medio	Velocidad de Cambio	Media
Tendencia del Desarrollo Urbano	Consolidado Homogeneo	Estado de Conservación	Bueno

Equipamiento del Entorno

	Nivel de Equipamiento		Nivel de Equipamiento
Comercial	Suficiente	Estacionamiento	Escaso
Escolar	Suficiente	Áreas Verdes	Suficiente
Asistencial	Suficiente	Zonas Recreativas	Escaso

Infraestructura de Servicio Urbano

	Dispone	Calidad	Estado de Conservación
Vías Asfaltadas	Completas	Medio	Bueno
Veredas	Completas	Medio	Bueno
Alcantarillado	Completas	Medio	Bueno
Agua Potable	Completas	Medio	Bueno
Alumbrado	Completas	Medio	Bueno

Vías Principales del Entorno: Av. Augusto B. Leguia, Av. Saenz Peña

4. CARACTERISTICAS DEL INMUEBLE

Terreno

Forma				Topografía				Posición			
Regular	X	Irregular		Plana	X	Pendiente		Interior		Exterior	X

Construcciones

Material Predominante	Edad Efectiva (años)	Estado de Conservación
Ladrillo	0	En Proyecto

Descripción General

N° de Pisos/ Sótanos del edificio	**Áreas Comunes**	**N° Unidades en el conjunto**
2 / 0	No	1
Nivel ocupado en el edificio.	**Ascensor**	**Conexión de Servicios**
Se ocuparán todos	No	Si
Obras Complementarias	**Mantenimiento**	**Vista**
No	Está en proyecto	Exterior

Descripción y Distribución Detallada del Inmueble: Se trata de un proyecto de construcción de vivienda de dos niveles del los cuales la entidad bancaria solo financiara el primer nivel. El proyecto se ejecutará sobre un terreno de geometría regular con un solo frente hacia calle Proceres en el distrito de José Leonardo Ortiz. El inmueble se sitúa en un entorno de uso predominantemente residencial con presencia de comercio vecinal, la zona cuenta con servicios básicos completos. Según los planos proporcionados el área a financiar contara con la siguiente distribución: 02 Cocheras, escalera, sala, comedor, cocina y habitación con baño interior.

Layseca Asociados

N° de Solicitud Banco	**1326668**
N° de Servicio Tasadora	**58168-2026**
Fecha de Expedición	26-Mar-2026
Fecha de Caducidad	26-Mar-2027

MEMORIA DESCRIPTIVA

Unidad Inmobiliaria	Linderos	Medida (Metros)
Por el Frente	Calle Proceres	12.00
Por la Derecha	Propiedad de terceros	12.00
Por la Izquierda	Propiedad de terceros	12.00
Por el Fondo	Propiedad de terceros	12.00
		48.00

TERRENO

Unidad Inmobiliaria	Unidad Métrica	A.M. Prop. Horiz/ Vert.	% Participación	Área Privativa	Obtención del Área	Observación
Terreno	m2			144.00	F. Reg/Part. Elect	
Total área de terreno				**144.00**		

Nota

CONSTRUCCION

Descripción	Unidad Métrica	Área Techada	Área sin Techar	Área Ocupada	Obtención del Área	Edificación Declarada
Piso 1	m2	100.00		100.00	Solicitud Construyo	No
Total áreas construidas		**100.00**	**0.00**	**100.00**		

Nota: De acuerdo con la solicitud construyo, se proyecta una construcción de dos niveles; sin embargo, se precisa que la entidad financiera otorgará financiamiento únicamente para la ejecución del primer nivel, es por ello que solo se considera el primer piso en el presente informe.

CARACTERISTICAS PRINCIPALES DE LA CONSTRUCCION

Calidad de la construcción: Muy Buena, Buena, Regular, Mala

Tipo de construcción: Definitiva, Parcial, Provisional, Autoconstrucción

Estructura general: Cimentación, Estructura, Muros, Techos, Cobertura, Inst. Eléctricas, Inst. Gas, Inst. Sanitarias

ACABADOS

Puertas	Tipo			
	Material			
	Sistema			
Ventanas	Marco			
	Vidrio			
	Sistema			
Mamparas	Marco			
	Vidrio			
	Sistema			
Muebles de cocina	Tipo			
	Material			
	Tableros			
	Lavaderos			
Baños	Tipo			
	Color			
	Grifería			
Closets				
Pisos				
Revestimientos				
Cerrajería				

Obras Complementarias e Instalaciones Fijas: Aire Acondicionado, Alarma, Ascensor, Intercomunicador, Sistema Hidroneumático; Cerco, Cisterna, Iluminación Especial, Piscina, Tanque Elevado

Otros y Comentarios: Se trata de un proyecto de construcción de vivienda, a la fecha no se han iniciado los trabajos .

Layseca Asociados

N° de Solicitud Banco	**1326668**
N° de Servicio Tasadora	**58168-2026**
Fecha de Expedición	26-Mar-2026
Fecha de Caducidad	26-Mar-2027

ANALISIS METODOLOGICO

METODO DE COSTOS O REPOSICION (OFERTA DE MERCADO PARA TERRENOS)

A. DATOS GENERALES DE REFERENCIAS DE MERCADO

	Ubicación / Descripción	Fuente Página Web	Teléfono	Nombre Contacto	Forma / Topografía	Zonif.	Distancia al bien (m)	Fecha
1	Casa ubicada en calle Conquista Urb. Latina, José Leonardo Ortiz * Se descontó el valor de la edificación	https://www.chiclayoinmobiliaria.com/propiedad/venta-de-casa-en-urbanizacion-latina-jose-leonardo-ortiz-chB6P	979464641	Chcilayo Inmobiliaria	Regular / Plana	CZ	460	26-Mar-26
2	Casa ubicada en calle Proceres Urb. Latina, José Leonardo Ortiz * Se descontó el valor de la edificación	https://www.remax.pe/web/search/property/propiedad-casa-en-venta-jose-leonardo-ortiz-chiclayo-lambayeque-1168172/	943884393	Victor Tello	Regular / Plana	CZ	200	26-Mar-26
3	Casa como terreno ubicada en calle Huáscar 323 Urb. San Carlos, José Leonardo Ortiz * Se descontó el valor de la edificación	https://www.facebook.com/share/1HSa8EJaGq/	-	Henry Perez	Regular / Plana	CZ	360	26-Mar-26
4	Edificio comercial de 5 pisos ubicado en calle España 931, José Leonardo Ortiz * Se descontó el valor de la edificación	https://www.remax.pe/web/search/property/propiedad-casa-en-venta-jose-leonardo-ortiz-chiclayo-lambayeque-1161925/	954535233	Rocio Carrasco	Regular / Plana	CZ	780	26-Mar-26
5	Casa antigua ubicada en urbanización San Carlos, José Leonardo Ortiz * Se descontó el valor de la edificación	https://www.panizoinmobiliaria.com/cc0001528-casa-urb-san-carlos/	932835188	Panizo Inmobiliaria	Regular / Plana	CZ	360	26-Mar-26

B. HOMOLOGACIÓN DE REFERENCIAS DE MERCADO DE TERRENOS

	Valor del Inmueble Referencial (US$)	Área (m2)	Valor Unitario Terreno (US$/m2)	Factores de HOMOLOGACIÓN						Factor Resultante	Valor Unit. Terreno Homologado (US$/m2)
				Ub.	Ent.	Sup.	Ser.	Zon.	F.N.		
1	140,703.66	160.00	879.40	1.00	1.00	0.99	1.00	0.98	0.99	0.96	844.22
2	139,139.00	160.00	869.62	1.00	1.00	0.99	1.00	0.98	0.99	0.96	834.83
3	76,434.96	95.90	797.03	1.00	1.00	1.06	1.00	0.98	0.99	1.03	820.94
4	163,088.50	160.00	1,019.30	1.00	1.00	0.99	1.00	0.98	0.99	0.96	978.53
5	91,951.83	100.00	919.52	1.00	1.00	1.05	1.00	0.98	0.99	1.03	947.10
	Valor Unitario Terreno Homologado Promedio [$/m²]		**885.12**	VUT Prom. Homologado ajustado[$/m²]							**885.00**


PLANO DE UBICACIÓN Y REFERENCIAS DE TERRENO



RESUMEN VALORES UNITARIOS

	Referencias	Ofertado	Homologado
COMPARABLES	140,703.66	879.40	844.22
	139,139.00	869.62	834.83
	76,434.96	797.03	820.94
	163,088.50	1,019.30	978.53
	91,951.83	919.52	947.10
	Promedio	US$ 896.97	US$ 885.12
	Máximo	US$ 1,019.30	US$ 978.53
	Mínimo	US$ 797.03	US$ 820.94
	Difer. Max Min	US$ 222.28	US$ 157.59

COMPORTAMIENTO DE VALORES UNITARIOS

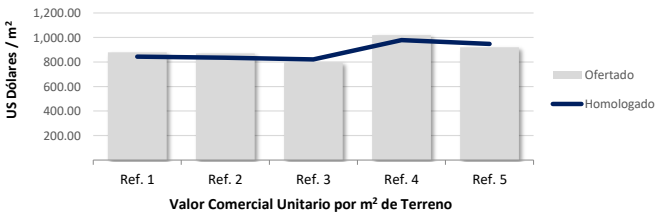

Layseca Asociados

N° de Solicitud Banco	**1326668**
N° de Servicio Tasadora	**58168-2026**
Fecha de Expedición	26-Mar-2026
Fecha de Caducidad	26-Mar-2027

ANALISIS METODOLOGICO

METODO DIRECTO DE COSTOS O REPOSICION

A. VALOR DE TERRENO (VT)

De acuerdo a la Investigación de Mercado de Terrenos con características similares al inmueble tasado se obtiene;

Unidad Inmobiliaria	Área de terreno (m2)	% de Participación	V.U. de Terreno (US$/m2)	Valor de Terreno (US$/m2)
Terreno	144.00	0.0%	885.00	127,440.00
		0.0%		
		0.0%		
		0.0%		
		0.0%		
		0.0%		
Subtotal Terreno (VT)	**144.00**			**127,440.00**

B. VALOR DE LAS EDIFICACIONES (VSNE Y VE)

De acuerdo a las características constructivas y a los acabados del inmueble observados en la inspección realizada se estima;

Región de la Edificación
Costa

Código	Partida	VUE1		VUE2		VUE3		VUE4		VUE5		VUE6	
		Clas.	Costo/m2	Clas.	Costo/m2	Clas.	Costo/m2	Clas.	Costo/m2	Clas.	Costo/m2	Clas.	Costo/m2
1	Muros y Columnas												
2	Techos												
3	Pisos												
4	Puertas y Ventanas												
5	Revestimientos												
6	Baños												
7	Instalaciones Eléctricas y Sanitarias												
	Costo Unitario de Edificación (S/)		**0.00**		**0.00**		**0.00**		**0.00**		**0.00**		**0.00**
Gastos Generales	**14%** (Obra Pequeña)												
Utilidad	**10%** Tipo de Cambio **S/. 3.467**												
	Valor Unitario de Edificación (S/)		**0.00**		**0.00**		**0.00**		**0.00**		**0.00**		**0.00**
	Valor Unitario de Edificación redondeado (US$)		**0.00**		**0.00**		**0.00**		**0.00**		**0.00**		**0.00**

Cálculo del Valor Similar a Nuevo o Valor de Reconstrucción de las Edificaciones (VSNE) y el Valor de las Edificaciones (VE)

Descripción	Área (m2)	VUE (US$/m2)	Valor Similar a Nuevo (US$)	Material Predominante	Edad (años)	Estado de Conservación	FD (*)	Valor de Edificación (US$)
Piso 1	100.00	980.67	98,067.49	Ladrillo	0	En Proyecto	1.00	98,067.49
Subtotal Edificaciones (VSNE)	**100.00**	US$	**98,067.49**	Subtotal Edificaciones (VE)		US$		**98,067.49**

C. VALOR DE ÁREAS COMUNES (VAC)

Según el Reglamento General de Tasaciones del Perú, para el valor de las Áreas Comunes, se asigna un % del valor de la edificación;

Descripción	% de Áreas Comunes	Valor Unitario de Áreas Comunes (US$/m2)	Valor de Reconstrucción Áreas Comunes (US$)	FD (*)	Valor de Áreas Comunes (US$)
Subtotal Áreas Comunes (VAC)		US$	**0.00**	US$	**0.00**

D. VALOR DE LAS INSTALACIONES Y OBRAS COMPLEMENTARIAS (VI + VOC)

Descripción	Cantidad	Unidad (u)	Valor Unitario (US$/u)	Valor de Reconstrucción (US$)	FD (*)	Valor de Inst. y Obras Complem. (US$)
Subtotal Instalaciones y Obras Complementarias (VI + VOC)			US$	**0.00**	US$	**0.00**

(*) Factor de Depreciación

E. VALOR TOTAL DEL PREDIO (VTP1) [Mediante el Método de Costos Directos = VT + VE + VAC + VI + VOC]	US$	**225,507.49**
F. VALOR DE RECONSTRUCCIÓN DEL INMUEBLE TASADO (VSN) [= VSNE + VSNAC + VSNVI + VSNVOC]	US$	**98,067.49**

Layseca Asociados

N° de Solicitud Banco	**1326668**
N° de Servicio Tasadora	**58168-2026**
Fecha de Expedición	26-Mar-2026
Fecha de Caducidad	26-Mar-2027

RESULTADOS

1. RESUMEN GENERAL DE TASACION

A. RESULTADOS DE LOS MÉTODOS DIRECTOS

	VTP (US$)	VU (US$/m2)	VTP (S/)
Método de Costos o Reposición	225,507.49	2,255.07	781,834.47
Método de Comparación o de Mercado	No considerado		

B. RESULTADO DEL MÉTODO INDIRECTO

Método de la Renta o Capitalización	No considerado		

2. VALOR COMERCIAL DEL INMUEBLE

A. VALOR COMERCIAL (VC)

Para determinar la conclusión del Valor Comercial del inmueble motivo de la presente tasación, se han tenido en cuenta las siguientes consideraciones

a.

b.

c.

d. El método que mejor refleja el Valor Comercial es por **Método Directo de Costos (O de Reposición)**

	Valor Comercial
Valor Comercial en Dólares (Moneda Extranjera)	
DOSCIENTOS VEINTISEIS MIL CON 00/100 DÓLARES AMERICANOS	**US$ 226,000.00**
Valor Comercial en Soles (Moneda Local)	
SETECIENTOS OCHENTA Y TRES MIL QUINIENTOS CUARENTA Y DOS CON 00/100 SOLES	**S/ 783,542.00**

VALOR DE REALIZACION

A. VALOR DE REALIZACIÓN INMEDIATA (VRI)

El Valor de Realización Inmediata, es el Valor Neto del inmueble que se esperaría recuperar como consecuencia de la eventual venta del bien en el menor tiempo posible y en las condiciones actuales del inmueble y el mercado. Se obtiene descontando los castigos y cargos por los conceptos indicados a continuación;

	Concepto de la Deducción	% de la Deducción	Importe (US$)
A	Gastos de Publicidad.	2.00%	4,520.00
B	Gastos de tasación del inmueble para la Realización.	0.20%	452.00
C	Comisiones de Ventas.	5.00%	11,300.00
D	Mantenimiento.	2.00%	4,520.00
E	Factor por la venta del inmueble (Realización) en un plazo de 60 días.	10.80%	24,408.00
F	Otras Deducciones (Sólo casos especiales)	0.00%	0.00
	Total Deducciones	**20.00%**	**US$ 45,200.00**

	Valor Realización Inmediata
En Dólares (Moneda Extranjera)	
CIENTO OCHENTA Y UN MIL CON 00/100 DÓLARES AMERICANOS	**US$ 181,000.00**
En Soles (Moneda Local)	
SEISCIENTOS VEINTISIETE MIL QUINIENTOS VEINTISIETE CON 00/100 SOLES	**S/ 627,527.00**

RESPONSABLE

EMPRESA TASADORA **LAYSECA ASOCIADOS S.A.C.**

REGISTRO REPEV **N° 2741-2013**

PERITO RESPONSABLE DE INSPECCION OCULAR **Ing. Johan Cuichap Aguilar**

LAYSECA ASOCIADOS SAC
REPEV Nº 2741-2013

PERITO	Arq. Maria Fernanda Mena Carbajal
PROFESION	Arquiteca
REPEV	N° 3749-2016
CAP	N° 16376

PERITO	Ing. Manuel Barboza Oviedo
PROFESION	Ingeniero Civil
REPEV	N° 02668-2022
CIP	N° 258213

OBSERVACIONES DEL PERITO

• La ubicación del inmueble se verifico mediante código de suministro eléctrico y recibo correspondiente.

• Se trata de un proyecto de construcción de vivienda, las áreas de terreno, áreas construidas, áreas ocupadas, etc. fueron obtenidas de la documentación proporcionada por el cliente.

• De acuerdo con la solicitud construyo, se proyecta una construcción de dos niveles; sin embargo, se precisa que la entidad financiera otorgará financiamiento únicamente para la ejecución del primer nivel.

CONDICIONANTES Y ADVERTENCIAS

a. Las áreas de terreno, áreas construidas, áreas libres, áreas ocupadas y perímetro del predio fueron obtenidas de la documentación registral, documentación municipal y planos, proporcionados por el propietario. Layseca Asociados S.A.C. no ha realizado mediciones en el predio ni revisada documentación distinta a la proporcionada por el propietario.

b. Layseca Asociados S.A.C. no asume responsabilidad sobre la veracidad, confiabilidad, exactitud, fidelidad, plenitud y precisión de la información proporcionada por el propietario, ni sobre las conclusiones erradas que eventualmente podrían haberse derivado de ella. La existencia de documentos adicionales no proporcionados, que puedan contener información diferente de la proporcionada, puede invalidar las conclusiones del presente informe sin responsabilidad alguna de Layseca Asociados S.A.C.

c. Este informe ha sido elaborado sobre la base de lo apreciado visiblemente durante la inspección ocular del predio. Layseca Asociados S.A.C. no asume responsabilidad por vicios ocultos en el predio ni por la calidad posesoria de las personas que se encuentren dentro del predio.

d. La interpretación de los documentos y sus condiciones, específicamente aplicada a la pericia, no constituye asesoría legal ni comercial especializada en la materia.

e. Las conclusiones del informe son válidas en su fecha de emisión y durante el periodo de vigencia establecido, siempre que no varíen significativamente las condiciones del mercado y de los bienes, en cuyo caso deberá requerirse una actualización de la valuación.

f. El objeto del presente informe de tasación es el de determinar el valor comercial del bien inmueble y no el servir de asesoría legal, técnica estructural, ni de otro tipo

Layseca Asociados

N° de Solicitud Banco	**1326668**
N° de Servicio Tasadora	**58168-2026**
Fecha de Expedición	26-Mar-2026
Fecha de Caducidad	26-Mar-2027

DOCUMENTACION GRAFICA



FACHADA



NUMERACION MEDIDOR



ENTORNO



ENTORNO



INTERIOR



INTERIOR



INTERIOR



INTERIOR

Layseca Asociados

N° de Solicitud Banco	**1326668**
N° de Servicio Tasadora	**58168-2026**
Fecha de Expedición	26-Mar-2026
Fecha de Caducidad	26-Mar-2027

DOCUMENTACION GRAFICA



INTERIOR



INTERIOR



INTERIOR



INTERIOR



INTERIOR



INTERIOR



INTERIOR



INTERIOR

sunarp
Superintendencia Nacional de los Registros Públicos

CERTIFICADO LITERAL DE

REGISTRO DE PROPIEDAD INMUEBLE

DOCUMENTO CON VALOR LEGAL PARA TODO TIPO DE TRÁMITE

Código de Verificación Digital


59414029

ZONA REGISTRAL N° II – SEDE CHICLAYO

Publicidad Nro. 2026 – 427335

Partida Registral N°: 02011642

20/01/2026 09:47:04

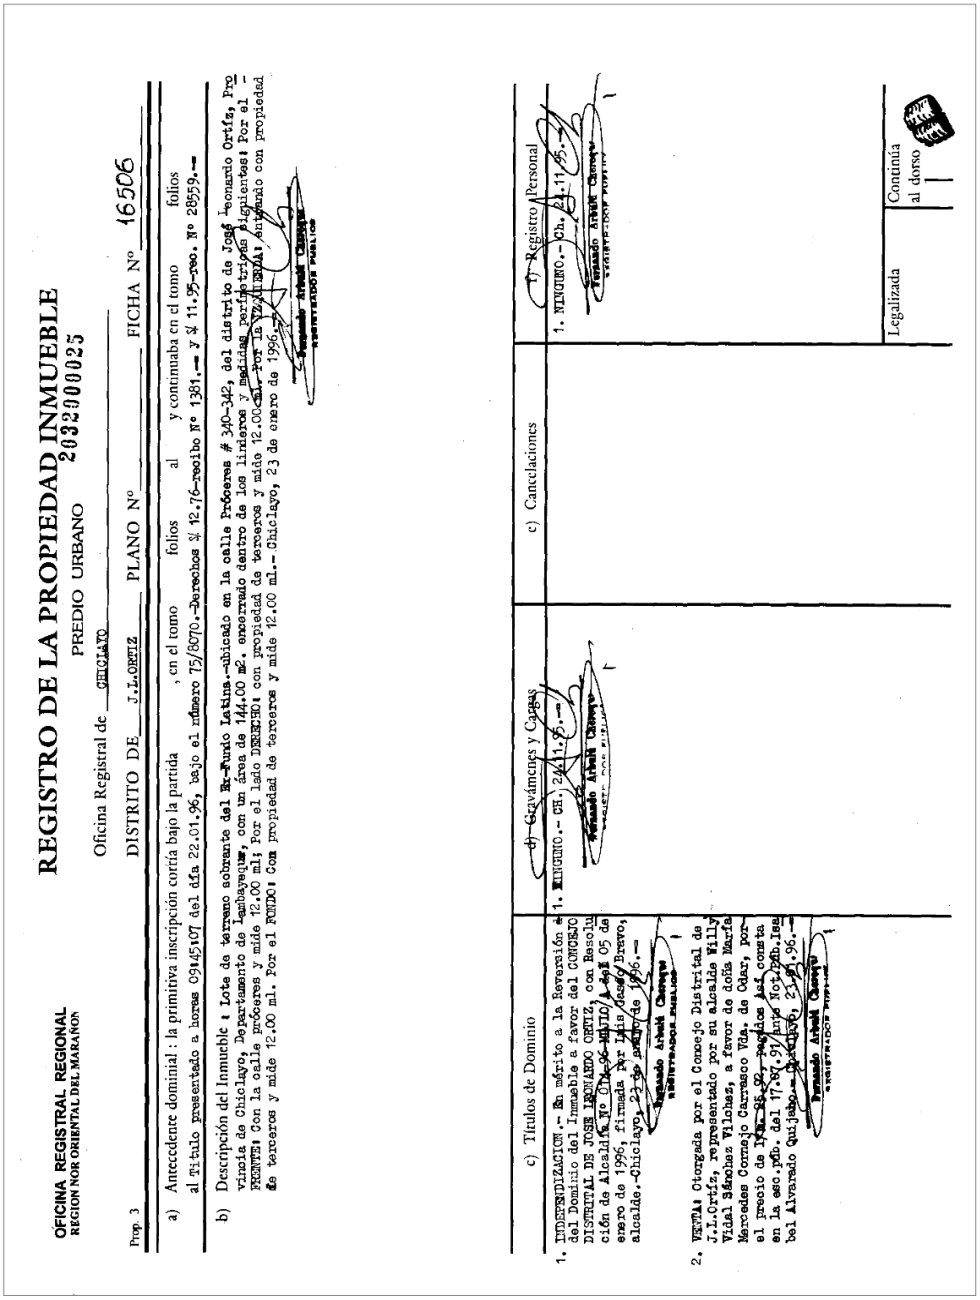

REGISTRO DE LA PROPIEDAD INMUEBLE 2032900025

OFICINA REGISTRAL REGIONAL
REGION NOR ORIENTAL DEL MARAÑON

PREDIO URBANO

Oficina Registral de CHICLAYO

DISTRITO DE J.L.ORTIZ PLANO N° FICHA N° 16506

Prop. 3

a) Antecedente dominial : la primitiva inscripción corría bajo la partida , en el tomo folios al y continuaba en el tomo folios al título presentado a horas 0945107 del día 22.01.96, bajo el número 75/8070.-Derechos S/ 12.76-recibo Nº 1381.- y S/ 11.95-ceo. Nº 28559.-

b) Descripción del Inmueble : Lote de terreno ubicado en la Urb.Pueblo Latino.-ubicado en la calle Próceres # 340-342, del distrito de José Leonardo Ortiz, Provincia de Chiclayo, Departamento de Lambayeque, con un área de 144.00 M2. encerrado dentro de los linderos y medidas perimétricas siguientes: Por el FRENTE: Con la calle próceres y mide 12.00 ml; Por el lado DERECHO: con propiedad de terceros y mide 12.00 ml.- Por la IZQUIERDA: colindando con propiedad de terceros y mide 12.00 ml. Por el FONDO: Con propiedad de terceros y mide 12.00 ml.- Chiclayo, 23 de enero de 1996.-

c) Títulos de Dominio

1. INDEPENDIZACION.- En mérito a la Rectificación de Área del Dominio del Inmueble a favor del CONSEJO DISTRITAL DE JOSE LEONARDO ORTIZ, con Resolución de Alcaldía Nº 016-96-MDJLO/A del 05 de enero de 1996, firmada por Luis Alberto Bravo, alcalde.-Chiclayo, 22 de enero de 1996.-

2. VENTA: Otorgada por el Consejo Distrital de J.L.Ortiz, representado por su alcalde Willy Vidal Sánchez Vilches, a favor de doña María Mercedes Cornejo Carrasco Vda. de Cuay, por el precio de S/. 38.00, según obra de autos, que consta en la esc.pub. del 17.07.91 ante Not.Pub.Ieo del Alvarado Quiroz.- Chiclayo, 23.01.96.-

c) Cancelaciones

d) Gravámenes y Cargas

1. HIPOTECA.- CH. 24.11.95.-

e) Registro Personal

1. HIPOTECA.- Ch. 24.11.95.-

Legalizada

Continúa al dorso

Layseca Asociados

N° de Solicitud Banco	**1326668**
N° de Servicio Tasadora	**58168-2026**
Fecha de Expedición	26-Mar-2026
Fecha de Caducidad	26-Mar-2027

DOCUMENTACION

PREDIO URBANO

SAT
SERVICIO DE ADMINISTRACIÓN TRIBUTARIA JOSÉ LEONARDO ORTÍZ

SERVICIO DE ADMINISTRACIÓN TRIBUTARIA DE JOSÉ LEONARDO ORTIZ

DECLARACIÓN JURADA DE AUTOVALUO AÑO: 2026

T.U.O LEY DE TRIBUTACIÓN MUNICIPAL (D.S N°156-2004-EF)

20260052448-2

PU PREDIO URBANO

1. IDENTIFICACIÓN DEL CONTRIBUYENTE

Código del Contribuyente: 00000002524 **DNI/RUC:**

Apellidos y Nombres / Razón Social: CORNEJO VDA. DE ODAR MARIA MERCEDES

Tipo de Persona: PERSONA NATURAL

Domicilio Fiscal: CA. PROCERES 00340 - URB. SAN CARLOS **%Propiedad:** 100.00

Condición Especial: **Fecha de Condición:**

2. REPRESENTANTE LEGAL

Apellidos y Nombres:

3. IDENTIFICACIÓN DEL PREDIO

Código Predio: 00000180645 **Clasificación Predio:** Casas Habitación y Departamentos

Nro. Habitantes: **Condición del Predio:** PROPIETARIO UNICO

Fecha de Adquisición: 01/01/1900 **Cod. Und. Catastral:** **N° Partida Electrónica:**

Ubicación: URB. SAN CARLOS - CA. PROCERES 00340

4. IDENTIFICACIÓN DEL DOCUMENTO

N° Declaración: 20260028206-2

5. DATOS DEL PREDIO

PISO	CLAS	MAT	CONS	ANT	MUROS	TECHO	PUERTA	VALOR UNIT.	INCRE 5%	DEPREC. %	VALOR UNIT. DEPREC.	ÁREA CONST. M2	VALOR DE CONSTRUCCIÓN
01	CAS	03	03	66	F	G	G	273.26	0.00	80.00	54.65	130.00	7,104.50

6. OTRAS INSTALACIONES

MAT	CONS	ANT	DESCRIPCIÓN	CANT.	UND.	VALOR UNIT.	DEPREC. %	VALOR UNIT. DEPREC.	VALOR DE OTRA INSTALACIÓN

7. DATOS DEL TERRENO

Área del Terreno: 144.00 **Arancel:** 254.00 **Frontis:** 0.00

8. DETERMINACIÓN DE AUTOVALÚO

Valor Terreno:	36,576.00
Valor Construido:	7,104.50
Valor Otras Instalaciones:	0.00
Valor Áreas Comunes:	0.00
Total Autovalúo:	43,680.50
Total Autovalúo Afecto:	43,680.50

9. ARBITRIOS

Barrido de Calles	35.28
Recojo de Residuos Sólidos	234.00
Parques y Jardines:	65.28
Serenazgo:	92.28
TOTAL ARBITRIOS	426.84

SERVICIO DE ADMINISTRACIÓN TRIBUTARIA SAT GERENCIA GENERAL

Los datos contenidos en el presente formato, tendrán efectos de Declaración Jurada de Autoevalúo para el ejercicio fiscal vigente, siempre y cuando no se presente una Declaración Jurada Sustitutoria, dentro del plazo establecido en el literal a) del Artículo 14 de la Ley de Tributación Municipal - DS Nº 156-2004-EF.

impreso por GERENCIA01 el 20/03/2026 - 05:08:47 p.m.

Layseca Asociados

N° de Solicitud Banco	**1326668**
N° de Servicio Tasadora	**58168-2026**
Fecha de Expedición	26-Mar-2026
Fecha de Caducidad	26-Mar-2027

ANEXO I

SUSTENTO DE UBICACIÓN

sunarp
Superintendencia Nacional de los Registros Públicos

ZONA REGISTRAL N° II - SEDE CHICLAYO
OFICINA REGISTRAL CHICLAYO
N° Partida: 02011642

INSCRIPCION DE REGISTRO DE PREDIOS
CALLE LOS PROCERES NUM 340-342
JOSE LEONARDO ORTIZ

REGISTRO DE PROPIEDAD INMUEBLE
RUBRO: TITULOS DE DOMINIO
C00001



FACHADA



NUMERACION DEL DEPARTAMENTO

RECIBO Nº S251-53391408 **Febrero-2026**

José leonardo ortíz, Chiclayo -

Para Consultas, su código **26012131**

CORNEJO VDA DE ODAR, MARIA MERCEDES

C.P.M SAN CARLOS Ca PROCERES 0340 0000
Ref.: PROCERES 340

2030601 -

Ensa

EMPRESA REGIONAL DE SERVICIO PÚBLICO DE ELECTRICIDAD DEL NORTE S.A.
San Martín N° 250 - Chiclayo
R.U.C. 20103117560

3. IDENTIFICACIÓN DEL PREDIO

Código Predio: 00000180645
Clasificación Predio: Casas Habitación y Departamentos
Nro. Habitantes:
Condición del Predio: PROPIETARIO UNICO
Fecha de Adquisición: 01/01/1900
Cod. Und. Catastral:
N° Partida Electrónica:
Ubicación: URB. SAN CARLOS - CA. PROCERES 00340


4. IDENTIFICACIÓN DEL DOCUMENTO

Layseca Asociados

N° de Solicitud Banco	**1326668**
N° de Servicio Tasadora	**58168-2026**
Fecha de Expedición	26-Mar-2026
Fecha de Caducidad	26-Mar-2027

ANEXO II

PLANO DE ZONIFICACIÓN Y VALIDACIÓN DE LOCALIZACIÓN (VISTA GOOGLE MAPS)

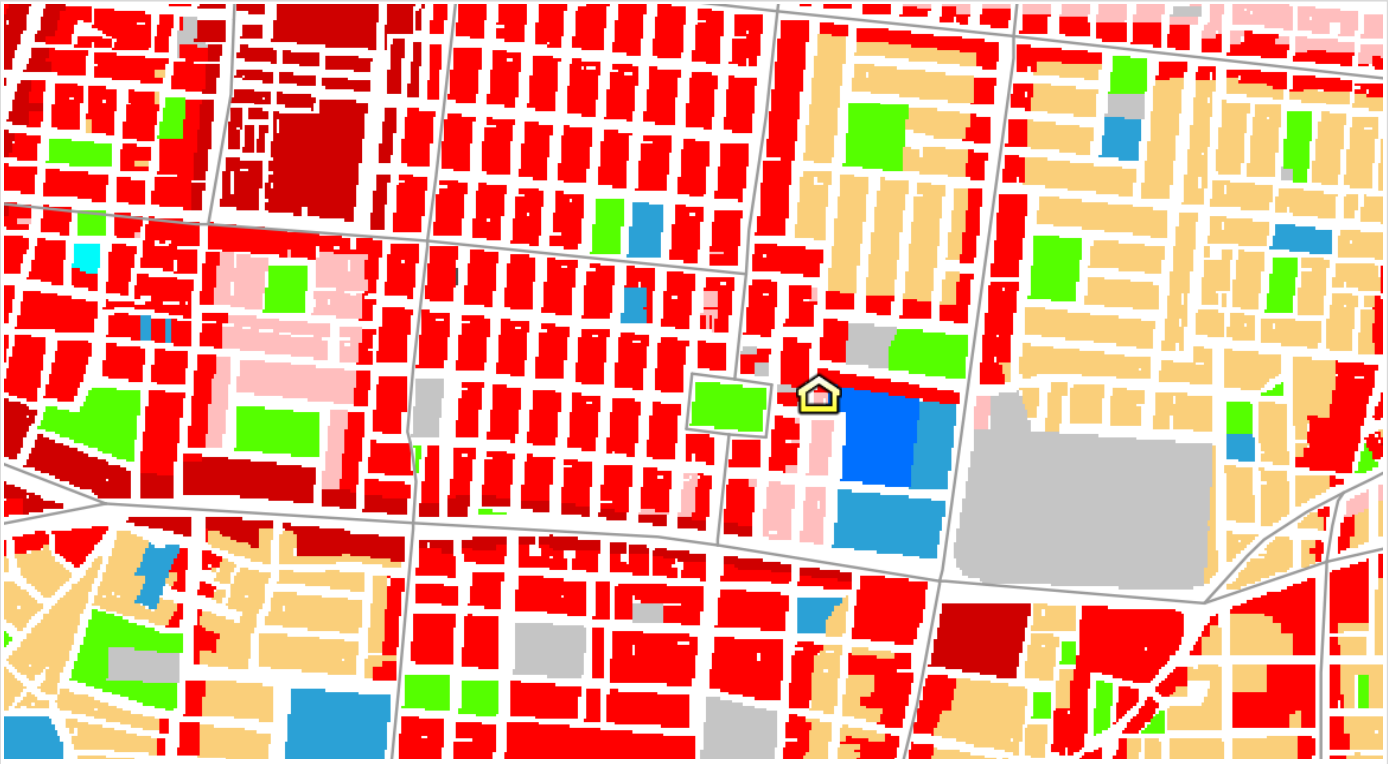

PLANO DE ZONIFICACIÓN



VALIDACIÓN DE LOCALIZACIÓN (VISTA GOOGLE MAPS)

PROYECTO DE VIVIENDA UNIFAMILIAR

Cliente: Sra. Katherine Dávila Díaz

Ubicación: Urb. Latina - Calle Próceres 340, J.L.O.

1. DATOS GENERALES

El presente proyecto corresponde al diseño arquitectónico de una vivienda unifamiliar desarrollada sobre un terreno de 144.00 m^2, con una edificación de dos niveles y un área techada total de 201.60 m^2.

2. DESCRIPCIÓN ARQUITECTÓNICA

Primer Nivel:
El primer nivel está destinado a las áreas sociales y de servicio, comprendiendo dos cocheras en la parte frontal, una sala, comedor integrado, cocina funcional, un baño de visitas y una escalera interna que conecta con el segundo nivel.

Segundo Nivel:
El segundo nivel alberga la zona privada, conformada por un dormitorio principal con walking closet y baño, dormitorios secundarios, un baño compartido y un hall o sala de estar.

3. ÁREAS DEL PROYECTO

Área de terreno: 144.00 m^2

Área techada total: 201.60 m^2

Número de niveles: 2

4. CRITERIOS DE DISEÑO

El diseño prioriza la funcionalidad, adecuada distribución de ambientes, iluminación y ventilación natural, así como la separación entre áreas sociales y privadas, garantizando confort y eficiencia en el uso del espacio.

1.1. Acabados:

- Pisos: Los pisos contarán con porcelanato de 0.60 * 0.60 m.
- Escaleras:
  Escalera principal: será de concreto revestida en porcelanato.
- Contra zócalos: Todos los ambientes llevarán contra zócalo de porcelanato de 0.10 * 0.60 cm, el color será el mismo que el del piso.
- Muros: Tarrajeo frotachado acabado liso en todos los muros interiores y exteriores.
- Zócalos: Baldosa cerámica celima h= 10 cm en baños con una altura de piso a techo.
- Cielo raso: Tarrajeo frotachado en todos los ambientes.

Carpintería:

- Puerta: Serán contraplacadas con bastidores de madera tornillo, marco con sección 3" x 2"; las puertas contraplacadas tendrán un espesor de 45 mm, se. Todas las puertas serán selladas con laca a la piroxilina y acabada en barniz mate color natural.
- Ventanas: En sistema directo con vidrio translucido de 5.5 ,8 y 10 mm con perfilería en aluminio.
- Cerrajería: Bisagras aluminizadas de 3" en puertas. Cada puerta llevara 3 bisagras con tornillos de aluminio. Las cerraduras serán cilíndricas tipo podo en todas las puertas y serán color acero.
- Mamparas: Se empleará vidrio translucido de 8 y 10 mm de espesor.
- Pinturas: Pintura Vence látex (Látex Vence látex) para interiores y exteriores. Cielo raso, en color Blanco.

Sanitarios:


- Lavatorio: Bowl Vivaldi blanco (FV), bowl Rossini blanco (Trebol).
- Inodoros: Inodoro Onepiece Trento blanco (FV), inodoro Milan blanco (FV).
- Accesorios: Papeleras, toalleras y jaboneras de aluminio.
- Grifería: Grifería monocomando Arizona (FV) y grifería de pared Scala Lever (FV)

Layseca Asociados

N° de Solicitud Banco	**1326668**
N° de Servicio Tasadora	**58168-2026**
Fecha de Expedición	26-Mar-2026
Fecha de Caducidad	26-Mar-2027

ANEXO IV

PLANOS

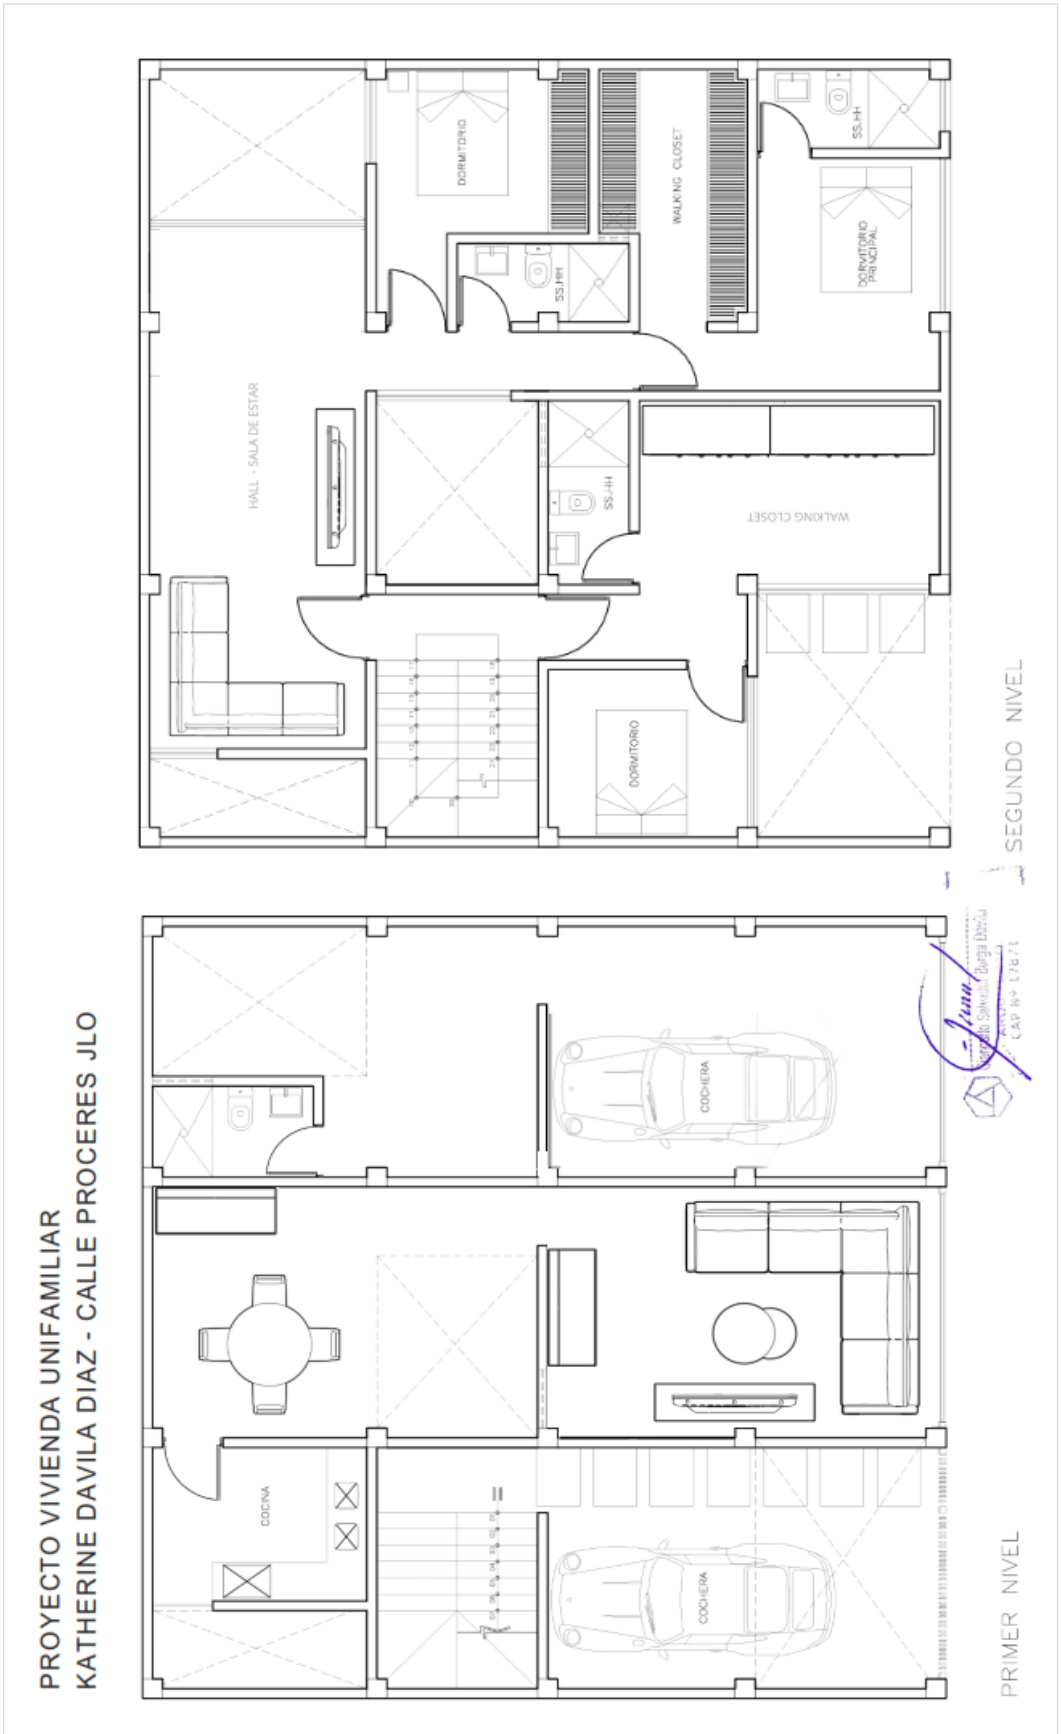

Layseca Asociados

N° de Solicitud Banco	**1326668**
N° de Servicio Tasadora	**58168-2026**
Fecha de Expedición	26-Mar-2026
Fecha de Caducidad	26-Mar-2027

ANEXO IV

SOLICITUD CONSTRUYO

BBVA

Solicitud Construyo

1. Nombre del cliente: Katherine Milagros Dávila Diaz.

2. Dirección del inmueble a edificar (indicar referencias): Calle Progreso 340-342, José Leonardo Ortiz

3. N° de Partida Electrónica / Copia Literal (documentación registral): 02011647.

4. Cuadro de áreas (diagrama por pisos, áreas construidas existentes y nuevas):

	ÁREAS TECHADAS (Existentes)	ÁREAS TECHADAS (Nuevas)
PRIMER PISO		100 mt²
SEGUNDO PISO		101.60 mt²
TERCER PISO		
CUARTO PISO		
ÁREA TOTAL		201.60 mt²

5. Detalle del financiamiento (indicar si se va a financiar todos los niveles, solo en casco gris, los primeros dos pisos, etc.)

Se financia solo el primer nivel.

6. Descripción del proyecto

Vivienda Unifamiliar de 2(dos) niveles

7. Presupuesto global por especialidades (Soles):

PARTIDAS DE LA CONSTRUCCIÓN	VALOR (S/.)
Estructura	114,658.39
Arquitectura	98 163.87
Instalaciones Sanitarias	18 543.51
Instalaciones Eléctricas	15 256.63
Instalaciones Mecánicas	30 924.62
Sub Total	277 551.02
Utilidad	8 326.53
Gastos Generales	4163.29
IGV	49 959.18
TOTAL	340 000.00

8. Fecha de finalización de obra estimada:

01/04/2026

KATHERINE M. DAVILA DIAZ

DNI° 70914503.

Scanned with CamScanner

PRESUPUESTO

Presupuesto **1101002** **PROYECTO VIVIENDA - UNIFAMILIAR**
Cliente **SRA: KATHERINE DAVILA DIAZ**

Lugar **URB LATINA -CALLE PROCERES 340 J.L.O**

Item	Descripción	Und.	Metrado	Precio S/.	Parcial S/.
01	**OBRAS PROVISIONALES, TRABAJOS PRELIMINARES, SEGURIDAD Y SALUD**				
01.01	**OBRAS PROVISIONALES Y TRABAJOS PRELIMINARES**				**10,215.30**
01.01.01	**CONSTRUCCIONES PROVISIONALES**				**6,924.80**
01.01.01.01	CERCO PERIMETRICO	m	80.00	18.36	1,468.80
01.01.01.02	ALMACEN CON TRIPLAY	m2	16.00	76	1,216.00
01.01.01.03	CASETA DE GUARDIANIA	m2	8.00	80	640.00
01.01.01.06	GUARDIANIA	mes	4.00	900	3,600.00
01.01.02	**INSTALACIONES PROVISIONALES**				**1,000.00**
01.01.02.01	AGUA PARA LA CONSTRUCCION	glb	1.00	550	550.00
01.01.02.02	ENERGIA ELECTRICA PROVISIONAL	glb	1.00	450	450.00
01.01.03	**TRABAJOS PRELIMINARES**				**225.00**
01.01.03.01	LIMPIEZA DEL TERRENO	m2	90.00	2.5	225.00
01.01.04	**MOVILIZACION DE MAQUINARIAS Y HERRAMIENTAS**				**635.00**
01.01.04.01	MOVILIZACION DE EQUIPOS	glb	1.00	635	635.00
01.01.05	**TRAZO NIVEL Y REPLANTEO PRELIMINAR**				**310.50**
01.01.05.01	TRAZO Y REPLANTEO INICAL DEL TERRENO	m2	90.00	3.45	310.50
01.02	**SEGURIDAD Y SALUD**				**1,120.00**
01.02.01	EQUIPOS DE PROTECCION INDIVIDUAL	glb	1.00	620	620.00
01.02.02	SEÑALIZACION TEMPORAL	glb	1.00	500	500.00
02	**ESTRUCTURAS**				
02.01	**MOVIMIENTO DE TIERRAS**				**15,652.10**
02.01.01	**NIVELACION DE TERRENO**				**585.00**
02.01.01.01	NIVELACION SUPERFICIAL	m2	90.00	6.5	585.00
02.01.02	**EXCAVACIONES**				**929.38**
02.01.02.01	EXCAVACIONES PLATEA	m3	62.00	14.99	929.38
02.01.03	**RELLENOS**				**9,822.52**
02.01.03.01	MATERIAL GRANULAR COMPACTADO- SUBZAPATA	m3	64.06	60.29	3,862.42
02.01.03.02	RELLENO MATERIAL PRESTAMO	m3	105.00	35	3,675.00
02.01.03.03	ARENILLA	m3	35.71	40	1,428.21
02.01.03.04	AFIRMADO	m3	21.42	40	856.89
02.01.04	**NIVELACION Y APISONADO**				**2,544.20**
02.01.04.01	COMPACTACION INTERIOR	m2	101.77	25	2,544.20
02.01.05	**ELIMINACION DE MATERIAL EXCEDENTE**				**1,771.00**
02.01.05.01	ELIMINACION DE MATERIAL EXCEDENTE +30% ESP.	m3	77.00	23	1,771.00
02.02	**OBRAS DE CONCRETO SIMPLE**				**4,138.61**
02.02.03	**SOLADOS**				**1,546.56**
02.02.03.01	CONCRETO F'C=100KG/CM2 PARA SOLADOS EN PLATEA	m2	53.70	28.8	1,546.56
02.02.06	**FALSO PISO**				**2,592.05**
02.02.06.01	CONCRETO F'C=140 KG/CM2 PARA FALSO PISO , E=4"	m2	74.57	34.76	2,592.05
02.03	**OBRAS DE CONCRETO ARMADO**				**114,658.39**
02.03.01	**CIMENTACION CORRIDA**				**17,183.52**
02.03.01.01	CONCRETO ZAPATAS f'c=210 kg/cm2	m3	32.22	380	12,243.60
02.03.01.02	ACERO CORRUGADO FY= 4200 kg/cm2 GRADO 60 - ZAPATAS	kg	1234.98	4	4,939.92
02.03.02	**VIGA DE CIMENTACION**				**8,798.41**
02.03.02.01	CONCRETO VIGAS CIMENTACION f'c=210 kg/cm2	m3	6.34	350	2,219.00
02.03.02.02	ENCOFRADO Y DESENCOFRADO DE VIGAS DE CIMENTACION	m2	50.73	52.12	2,644.05
02.03.02.03	ACERO CORRUGADO FY= 4200 kg/cm2 GRADO 60 - VIGAS DE CIMENTACION	kg	983.84	4	3,935.36
02.03.03	**SOBRECIMIENTOS REFORZADOS**				**7,329.45**
02.03.03.01	CONCRETO SOBRECIMIENTOS REFORZADOS f'c=175 kg/cm2	m3	6.34	350	2,219.00
02.03.03.02	ENCOFRADO Y DESENCOFRADO DE SOBRECIMIENTOS REFORZADOS	m2	82.43	44.63	3,678.85
02.03.03.03	ACERO CORRUGADO FY= 4200 kg/cm2 GRADO 60 - SOBRECIMIENTO REFORZADO	kg	357.90	4	1,431.60
02.03.04	**COLUMNAS**				**24,485.83**
02.03.04.01	CONCRETO COLUMNAS f'c=210 kg/cm2	m3	14.20	350	4,970.00
02.03.04.02	ENCOFRADO Y DESENCOFRADO DE COLUMNAS	m2	151.73	44.63	6,771.71
02.03.04.03	ACERO CORRUGADO FY= 4200 kg/cm2 GRADO 60 - COLUMNAS	kg	3186.03	4	12,744.12
02.03.05	**VIGAS**				**30,782.62**
02.03.05.01	CONCRETO VIGAS f'c=210 kg/cm2	m3	7.99	350	2,796.50
02.03.05.02	ENCOFRADO Y DESENCOFRADO DE VIGAS	m2	402.65	52.12	20,986.12
02.03.05.03	ACERO CORRUGADO FY= 4200 kg/cm2 GRADO 60 - VIGAS	kg	1750.00	4	7,000.00
02.03.06	**LOSAS**				
02.03.06.01	**LOSA MACIZA**				**5,038.88**
02.03.06.01.01	CONCRETO LOSA MACIZA f'c=210 kg/cm2	m3	3.25	402.65	1,308.61
02.03.06.01.02	ENCOFRADO Y DESENCOFRADO DE LOSA MACIZA	m2	19.21	101.38	1,947.51
02.03.06.01.03	ACERO CORRUGADO FY= 4200 kg/cm2 GRADO 60 - LOSA MACIZA	kg	445.69	4	1,782.76
02.03.06.02	**LOSA ALIGERADA**				**12,553.66**
02.03.06.02.01	CONCRETO LOSA ALIGERADA f'c=210 kg/cm2	m3	7.90	402.65	3,180.94
02.03.06.02.02	ENCOFRADO Y DESENCOFRADO DE LOSA ALIGERADA	m2	90.24	54.43	4,911.76
02.03.06.02.03	ACERO CORRUGADO FY= 4200 kg/cm2 GRADO 60 - LOSA ALIGERADA	kg	588.84	4	2,355.36
02.03.06.02.04	LADRILLO PARA TECHO DE 15X30X30	und	752.00	2.8	2,105.60
02.03.07	**ESCALERA**				**3,904.98**
02.03.07.01	CONCRETO ESCALERA f'c=210 kg/cm2	m3	2.36	402.65	950.25

02.03.07.02	ENCOFRADO Y DESENCOFRADO DE ESCALERA	m2	14.55	87.53	1,273.56
02.03.07.03	ACERO CORRUGADO FY= 4200 kg/cm2 GRADO 60 - ESCALERA	kg	420.29	4	1,681.16
02.03.08	**CISTERNA**				**4,581.05**
02.03.08.01	CONCRETO CISTERNA f'c=210 kg/cm2	m3	3.08	402.65	1,240.16
02.03.08.02	ENCOFRADO Y DESENCOFRADO DE CISTERNA	m2	31.44	57.13	1,796.17
02.03.08.03	ACERO CORRUGADO FY= 4200 kg/cm2 GRADO 60 - CISTERNA	kg	386.18	4	1,544.72
3	**ARQUITECTURA**				**98,163.87**
03.01.	**MUROS Y TABIQUES DE ALBAÑILERIA**				**22,257.89**
03.01.01	**MUROS DE LADRILLO KING KONG**				**18,917.89**
03.01.01.01	MURO LADRILLO K.K.DE ARCILLA 18 H (0.09x0.13x0.24) AMARRE DE SOGA JUNTA 1.5 cn	m2	362.62	52.17	18,917.89
03.01.02	**BARANDAS Y PARAPETOS**				**3,340.00**
03.01.02.01	BARANDA ESCALERA INTERIOR	glb	1.00	3340	3,340.00
3.3	**REVOQUES Y REVESTIMIENTOS**				**27,583.92**
03.03.01	**TARRAJEO NTERIORES**				**13,549.02**
03.03.01.01	TARRAJEO EN MURO: INTERIOR E=1.5cm, C:A; 1:5	m2	526.38	25.74	13,549.02
03.03.02	**TARRAJEO EXTERIORES**				**656.37**
03.03.02.01	TARRAJEO EN MURO: FACHADAE=1.5cm, C:A; 1:5	m2	25.50	25.74	656.37
03.03.03	**TARRAJEO EN COLUMNAS**				**2,862.43**
03.03.03.01	TARRAJEO DE COLUMNAS, E=1.5cm, C:A; 1:5	m2	104.24	27.46	2,862.43
03.03.04	**TARRAJEO EN VIGAS**				**984.17**
03.03.04.01	TARRAJEO DE VIGAS E=1.5cm, C:A; 1:5	m2	35.84	27.46	984.17
03.03.05	**VESTIDURA DE DERRAMES**				**2,623.53**
03.03.05.01	VESTIDURA DE DERRAMES, C:A 1:5	m	95.54	27.46	2,623.53
03.03.06	**TARRAJEO EN FONDO DE ESCALERA**				**380.64**
03.03.06.01	TARRAJEO EN FONDO DE ESCALERA E=1.5cm, C:A; 1:5	m2	10.40	36.6	380.64
03.03.07	**PREPARACION DE GRADAS**				**936.96**
03.03.07.01	TARRAJEO PARA GRADAS C:A, 1:5	m2	25.60	36.6	936.96
03.03.08	**CIELO RASOS**				**4,277.66**
03.03.08.01	TARRAJEO DE CIELORASO E=1.5cm, C:A 1:5	m2	108.57	39.4	4,277.66
03.03.09	**TARRAJEO CON IMPERMEABILIZANTE**				**581.15**
03.03.09.01	TARRAJEO E=1.5cm, C:A 1:5	m2	14.75	39.4	581.15
03.03.07	**PREPARACION DE DESCANSO**				**732.00**
03.03.07.01	TARRAJEO PARA GRADAS C:A, 1:5	m2	20.00	36.6	732.00
3.03	**PISOS Y PAVIMENTOS**				**20,601.03**
03.03.01	**CONTRAPISOS**				**5,634.81**
03.03.01.01	CONTRAPISO DE 2"	m2	137.00	41.13	5,634.81
03.03.02	**PISOS**				**12,625.53**
	PISOS 1 NIVEL				**8,619.52**
03.03.02.01	PISO CERAMICO 45X45 SSHH	m2	3.48	65.4	227.59
03.03.02.02	COCHERA 60X60 AT	m2	13.18	89.5	1,179.61
03.03.02.03	PISO PORCELANATO 120X25 TIPO DEC ESCALERA - COCHERA	m2	13.98	55.6	777.29
03.03.02.04	PISO PORCELANATO INGRESO	m2	5.80	45.5	263.90
03.03.02.05	PISO PORCELANATO RECIBIDOR,SALA,COMEDOR,KITCHEN	m2	26.44	89.9	2,376.96
03.03.02.06	PISO PORCELANATO CUARTO LIMPIEZA	m2	1.70	45.5	77.35
03.03.02.07	PISO PORCELANATO RECTIFICADO 60X60 SALA- COMEDOR	m2	14.98	86.2	1,291.28
03.03.02.08	PISO PORCELANATO ELEANE PEDRA 59X59 INGRESO-RECIBO	m2	4.78	145.6	695.97
03.03.02.09	PISO PORCELANATO PATIO 60X60	m2	5.33	65.5	349.12
03.03.02.10	TABLON GOLDE 20X60 DORMITORIOS	m2	14.44	95.6	1,380.46
	PISOS 2 NIVEL				**4,006.01**
03.03.02.01	PISO PORCELANATO 45X45 STAR TV ,PASADIZO , HALL	m2	20.23	65.4	1,323.04
03.03.02.02	SSHH 203 PORCELANATO	m2	3.21	65.4	209.93
03.03.02.03	PISO PORCELANATO 120X25 TIPO DEC ESCALERA	m2	13.98	55.6	777.29
03.03.02.04	PISO PORCELANATO ESTUDIO	m2	6.02	45.5	273.91
03.03.02.05	PISO PORCELANATO SALON DE JUEGOS	m2	6.43	55.2	354.94
03.03.02.10	TABLON GOLDE 20X60 DORMITORIO	m2	11.16	95.6	1,066.90
03.04.03	**ZOCALOS Y CONTRAZOCALOS**				**6,346.70**
03.04.03.01	**ZOCALOS 1 NIVEL**				**1,359.05**
03.04.03.01.01	ZOCALO DE PORCELANATO 30 X 60 EN SSHH	m2	22.74	41.5	943.71
03.04.03.01.02	ZOCALO DE PORCELANATO TIPO LADRILLO BLANCO 30 X 60 COCINA	m2	7.29	41.5	302.54
03.04.03.01.03	ZOCALO DE CERAMICA NORMAL 45X45 LAVANDERIA	m2	2.93	38.5	112.81
03.04.03.02	**ZOCALOS 2 NIVEL**				**2,212.79**
03.04.03.02.01	ZOCALO DE PORCELANATO 30 X 60 EN SSHH 1	m2	19.99	55.5	1,109.45
03.04.03.02.02	ZOCALO DE PORCELANATO 30 X 60 EN SSHH 2	m2	19.88	55.5	1,103.34
03.04.03.03	**CONTRAZOCALOS 1 NIVEL**				**1,334.32**
03.04.03.03.01	CONTRAZOCALO PORCELANATO 120X25 TIPO DEC ESCALERA - COCHERA	m	9.60	32.5	312.00
03.04.03.03.02	CONTRAZOCALO PORCELANATO RECIBIDOR,SALA,COMEDOR,KITCHEN	m	22.10	27.02	597.14
03.04.03.03.03	CONTRAZOCALO TABLON GOLDE 10X60 DORMITORIOS	m	19.98	21.28	425.17
03.04.03.04	**CONTRAZOCALOS 2 NIVEL**				**1,440.55**
03.04.03.04.01	CONTRAZOCALO PORCELANATO 10X60 STAR TV , HALL	m	26.22	27.02	708.46
03.04.03.04.02	CONTRAZOCALO SALON DE JUEGOS	m	9.98	21.28	212.37
03.04.03.04.03	CONTRAZOCALO ESTUDIO	m	9.23	21.28	196.41
03.04.03.04.04	CONTRAZOCALO TABLON GOLDE 10X60 DORMITORIOS	m	13.25	24.4	323.30
3.04	**CARPINTERIA DE MADERA**				**15,030.00**
03.04.01	**PUERTAS**				**11,550.00**
03.04.01.01	PUERTA CONTRAPLACADA PRINCIPAL	und	2.00	2400	4,800.00
03.04.01.02	CONTRA PUERTA	und	1.00	2500	2,500.00
03.04.01.03	PUERTA CONTRAPLACADA INTERIOR	und	5.00	850	4,250.00
3.05	**CERRAJERIA**				
03.05.01	**CERRADURAS**				**330.00**
03.05.01.01	CERRADURA FORTE BLINDADA 1000 EN PUERTA INGRESO	und	1.00	110	110.00
03.05.01.02	CERRADURA FORTE BLINDADA 1000 EN PUERTA INTERIOR	und	2.00	110	220.00
03.05.02	**SISTEMAS O MECANISMOS**				**3,150.00**
03.05.02.01	SISTEMA CORREDIZO AUTOMATIZADO	und	1.00	3150	3,150.00
03.05.03	**VIDRIOS**				**3,229.00**
03.05.03.01	MAMPARA EN CRISTAL TEMPLADO DE 10 mm	m2	8.60	320	2,752.00

03.05.03.02	VENTANAS EN CRISTAL TEMPLADO DE 6 mm	m2	3.18	150	477.00
03.05.04	**PINTURAS**				**9,676.63**
03.05.04.01	PINTURA LATEX EN MUROS INTERIORES Y EXTERIORES	m2	120.47	35.5	4,276.69
03.05.04.02	PINTURA LATEX EN VIGAS	m2	28.26	48.6	1,373.44
03.05.04.03	PINTURA LATEX EN COLUMNAS	m2	38.56	48.6	1,874.02
03.05.04.04	PINTURA LATEX EN CIELORASO	m2	44.29	48.6	2,152.49
03.06.05	**VARIOS, LIMPIEZA Y JARDINERIA**				**1,414.20**
03.06.05.01	SEMBRADO DE GRASS	m2	16.12	35	564.20
03.06.05.02	LIMPIEZAFINAL DE LA OBRA	glb	1.00	850	850.00
4	**INSTALACIONES SANITARIAS**				**18,547.51**
04.01.01	**SUMINISTRO E INSTALACION DE APARATOS SANITARIOS Y ACCESORIOS**				**3,555.00**
04.01.01.01	SUMINISTRO E INSTALACION DE INODORO ONE PIECE BLANCO TREBOL	pza	4.00	520	2,080.00
04.01.01.02	SUMINISTRO E INSTALACION DE LAVATORIO OVALIN BLANCO (SOBREPUESTO O EMPC	pza	4.00	185	740.00
04.01.01.03	SUMINISTRO E INSTALACION LAVADERO RECO INOX. DOS POZAS C/ ESCURRIDERO	pza	1.00	550	550.00
04.01.01.04	SUMINISTRO E INSTALACION DE LAVATORIOC/ PEDESTAL BLANCO TREBOL	pza	1.00	185	185.00
4.02	**SISTEMA DE AGUA FRIA**				**4,646.77**
04.02.01	**SALIDA DE AGUA FRIA PVC**				**1,144.94**
04.02.01.01	SALIDA AGUA FRIA TUBERIA PVC	pto	19.00	60.26	1,144.94
04.02.02	**REDES DE DISTRIBUCION C/T PAVCO SAP**				**1,529.96**
04.02.02.01	SUMINISTRO E INSTALACION DE TUBERIA PVC SAP C-10 ROSCADA DE 1/2"	m	49.42	11.83	584.64
04.02.02.02	SUMINISTRO E INSTALACION TUBERIA PVC SAP C-10 ROSCADA DE 3/4"	m	55.27	12.41	685.90
04.02.02.03	SUMINISTRO E INSTALACION DE TUBERIA PVC SAP C-10 ROSCADA DE 1"	m	17.60	14.74	259.42
04.02.03	**REDES DE ALIMENTACION**				**654.19**
04.02.03.01	SUMINISTRO E INSTALACION TUBERIA PVC SAP C-10 ROSCADA DE 3/4"	m	10.87	12.41	134.90
04.02.03.02	SUMINISTRO E INSTALACION DE TUBERIA PVC SAP C-10 ROSCADA DE 1"	m	35.23	14.74	519.29
04.02.04	**VALVULAS**				**1,317.68**
04.02.04.01	SUMINISTRO E INSTALACION DE VALVULA DE COMPUERTA GALVANIZADA PESADA DE	und	4.00	89.21	356.84
04.02.04.02	SUMINISTRO E INSTALACION DE VALVULA DE COMPUERTA GALVANIZADA PESADA DE	und	1.00	161.61	161.61
04.02.04.03	SUMINISTRO E INSTALACION VALVULA COMPUERTA GALVANIZADA PESADA DE 1" ELE	und	1.00	130.21	130.21
04.02.04.04	SUMINISTRO E INSTALACION DE VALVULA CHECK DE BRONCE DE 1" ELECTROBOMBA	und	1.00	181.98	181.98
01.02.04.05	SUMINISTRO E INSTALACION DE VALVULA CHECK DE BRONCE DE 3/4" CISTERNA	und	1.00	103.98	103.98
04.02.04.06	SUMINISTRO E INSTALACION DE VALVULA DE PIE 1" CISTERNA	und	1.00	189.72	189.72
04.02.04.07	SUMINISTRO E INSTALACION DE VALVULA FLOTADORA 3/4" CISTERNA	und	1.00	193.34	193.34
4.03	**ALMACENAMIENTO DE AGUA**				**2,235.09**
01.03.01	**ALMACENAMIENTO**				**1,167.57**
01.03.01.01	SUMINISTRO E INSTALACION DE TANQUE DE AGUA DE ETERNIT DE 1100 LITROS INCLU	und	1.00	1167.57	1,167.57
01.03.02	**EQUIPOS ELECTRONICOS Y METALICOS**				**1,067.52**
01.03.02.01	SUMINISTRO E INSTALACION DE EQUIPO DE BOMBEO PRESION CONSTANTE Y VELOC	und	1.00	1067.52	1,067.52
4.04	**SISTEMA PARA AGUA CALIENTE**				**3,831.85**
04.04.01	**SALIDA DE AGUA CALIENTE**				**200.72**
04.04.01.01	SALIDA AGUA CALIENTE TUBERIA CPVC	pto	2.00	100.36	200.72
04.04.02	**REDES DE DISTRIBUCION AGUA CALIENTE**				**1,060.97**
04.04.02.01	SUMINISTRO E INSTALACION DE TUBERIA CPVC SAP C-10 DE 1/2"	m	34.23	17.55	600.74
04.04.02.02	SUMINISTRO E INSTALACION DE TUBERIA CPVC SAP C-10 DE 3/4"	m	34.50	13.34	460.23
04.04.03	**VALVULAS GALVANIZADAS**				**1,340.16**
04.04.03.01	SUMINISTRO E INSTALACION DE VALVULA COMPUERTA DE BRONCE DE 1/2" CONTROL	und	12.00	111.68	1,340.16
04.04.04	**EQUIPOS DE PRODUCCION DE AGUA CALIENTE**				**1,230.00**
04.04.04.01	SUMINISTRO E INSTALACION DE THERMA SOLE DE 80 LITROS	und	1.00	1230	1,230.00
4.05	**SISTEMA DE DRENAJE PLUVIAL**				**1,534.95**
04.05.01	**SALIDAS DRENAJE PLUVIAL**				**508.08**
04.05.01.01	SALIDA DE DESAGUE PLUVIAL TUBERIA PVC 3"	pto	8.00	63.51	508.08
04.05.02	**REDES DE RECOLECCION**				**1,026.87**
04.05.02.01	SUMINISTRO E INSTALACION DE TUBERIA PVC SAP 3"	m	48.46	21.19	1,026.87
4.06	**DESAGUE Y VENTILACION**				**2,743.85**
04.06.01	**SALIDAS DESAGUE**				**653.04**
04.06.01.01	SALIDA DESAGUE DE PVC SAL	pto	9.00	72.56	653.04
04.06.02	**REDES DE DERIVACION**				**1,291.82**
04.06.02.01	SUMINISTRO E INSTALACION DE TUBERIA PVC SAL 2"	m	41.29	14.88	614.40
04.06.02.02	SUMINISTRO E INSTALACION DE TUBERIA PVC SAP 3"	m	17.96	21.19	380.57
04.06.02.03	SUMINISTRO E INSTALACION DE TUBERIA PVC SAP 4"	m	65.53	4.53	296.85
04.06.03	**CAMARAS DE INSPECCION**				**190.02**
04.06.03.01	CAJA DE REGISTRO 12"X24"	pza	1.00	190.015	190.02
4.07	**PRUEBAS HIDRAULICAS**				**608.98**
04.07.01	PRUEBA HIDRAULICA PARA AGUA FRIA	glb	1.00	304.49	304.49
04.07.02	PRUEBA HIDRAULICA PARA AGUA CALIENTE	glb	1.00	304.49	304.49
05	**INSTALACIONES ELECTRICAS Y MECANICAS**				**15,256.63**
5.01	INSTALACIONES ELECTRICAS				**880.00**
05.01.02	INSTLACION EXTERNA	glb	1.00	880	880.00
05.02	**SALIDA PARA ELECTRICIDAD Y FUERZA**				**3,550.00**
05.02.01	SALIDAS PUNTOS	glb	1.00	3550	3,550.00
05.02.02	**CANALIZACION Y/O TUBERIA OTROS**				**2,961.41**
05.02.02.01	TUBERIA PVC-SAP 20 mm (3/4")	m	667.18	4.2	2,802.16
05.02.02.02	TUBERIA PVC-SAP 20 mm (1")	m	24.35	6.54	159.25
05.02.03	**CONDUCTORES EN TUBERIAS**				**5,329.62**
05.02.03.01	CABLE 2.5 mm2 THW-AWG	m	667.50	3.50	2,336.25
05.02.03.02	CABLE 4 mm2 THW-AWAG	m	778.72	3.5	2,725.52
05.02.03.03	CABLE 6 mm2 THW-AWAG	m	24.35	11	267.85
05.02.04	**TABLEROS PRINCIPALES**				**250.00**
05.02.04.01	TABLERO GENERAL METALICO	pza	1.00	250	250.00
05.02.05	**TABLEROS DISTRIBUCION**				**167.00**
05.02.05.01	TABLERO SD	pza	1.00	85	85.00
05.02.05.02	TABLEROTD-02	pza	1.00	82	82.00
05.03	**POZO A TIERRA**				**1,200.00**
05.03.01	POZO DE TIERRA	und	1.00	1200.00	1,200.00
06	INSTALACION DE COMUNICACIONES				**918.61**

06.01	TUBERIA PVC-SAP 20 mm (3/4")	m	139.74	6.57	918.61
	COSTO DIRECTO				**277,551.02**
	GASTOS GENERALES				**4,163.27**
	UTILIDAD 4%				**8,326.53**
	IGV				**49,959.18**
	TOTAL				**340,000.00**

SON : SON TRESCIENTOS CUARENTA MIL 00/100 NUEVOS SOLES

Fecha : 15 de Marzo 2026

